MONTAGEM T

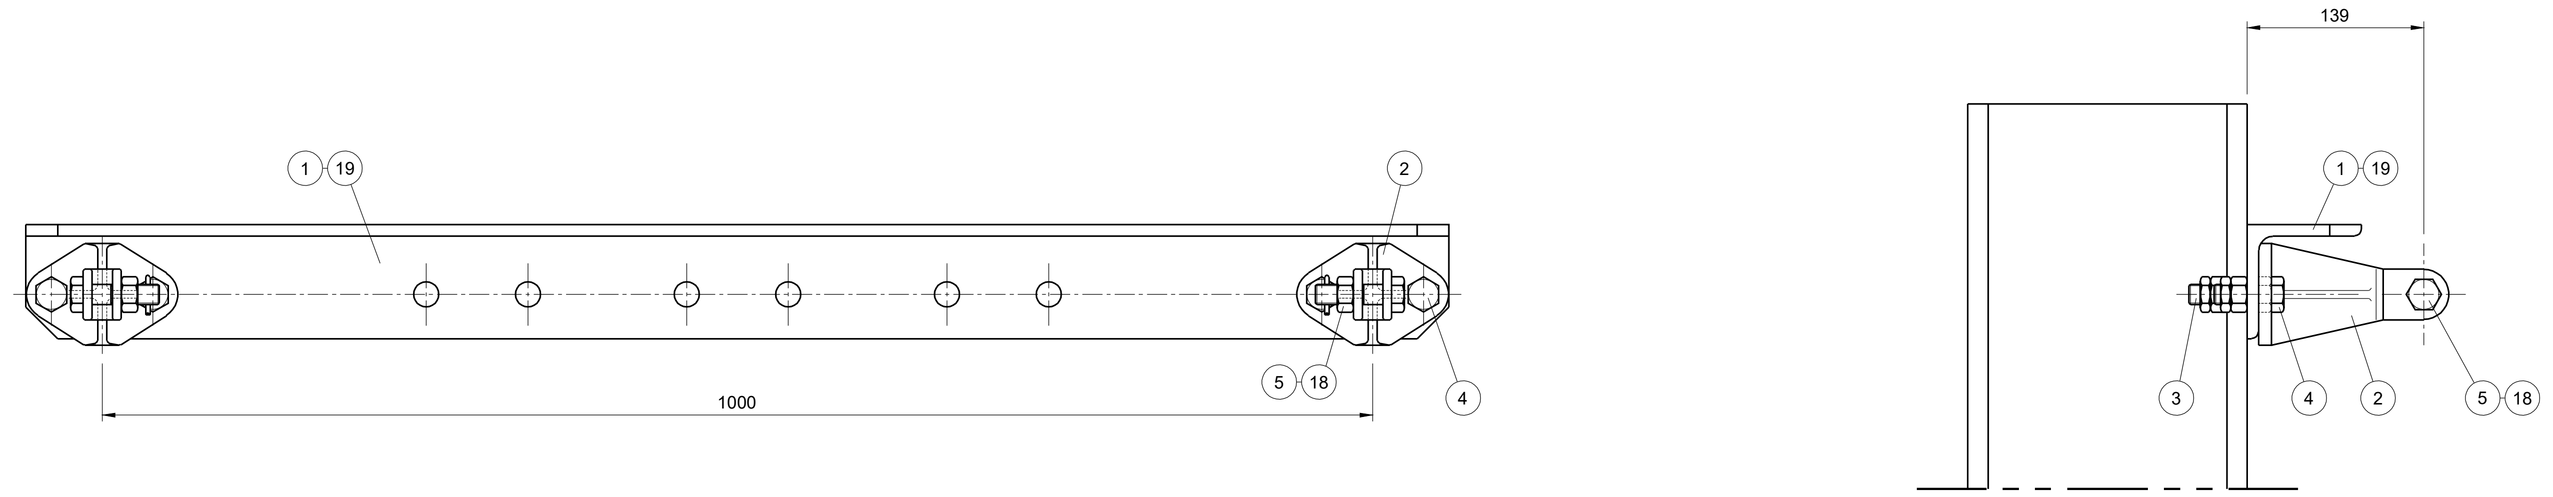

MONTAGEM TR

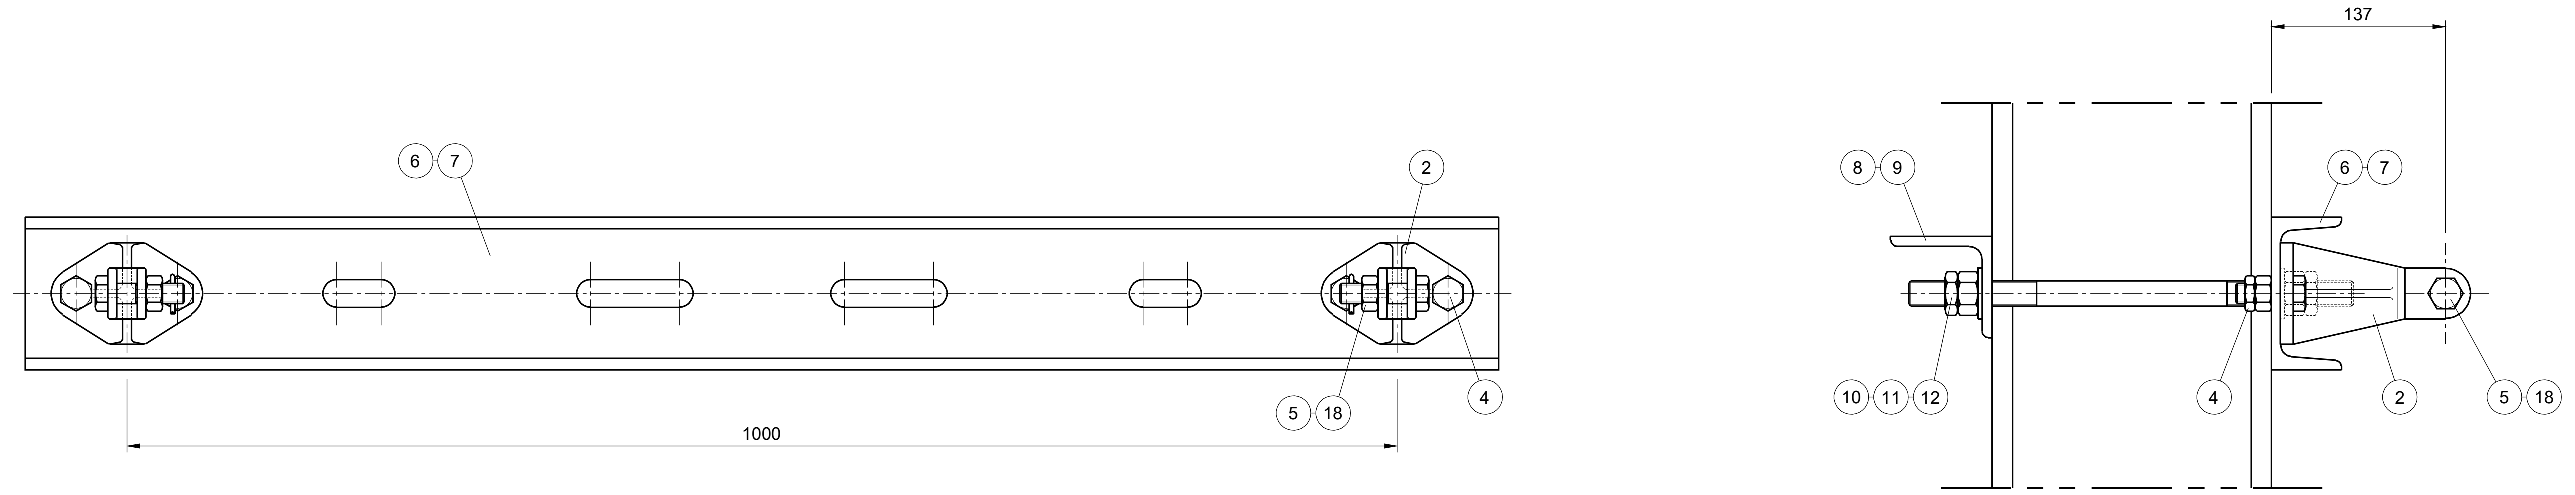

MONTAGEM C

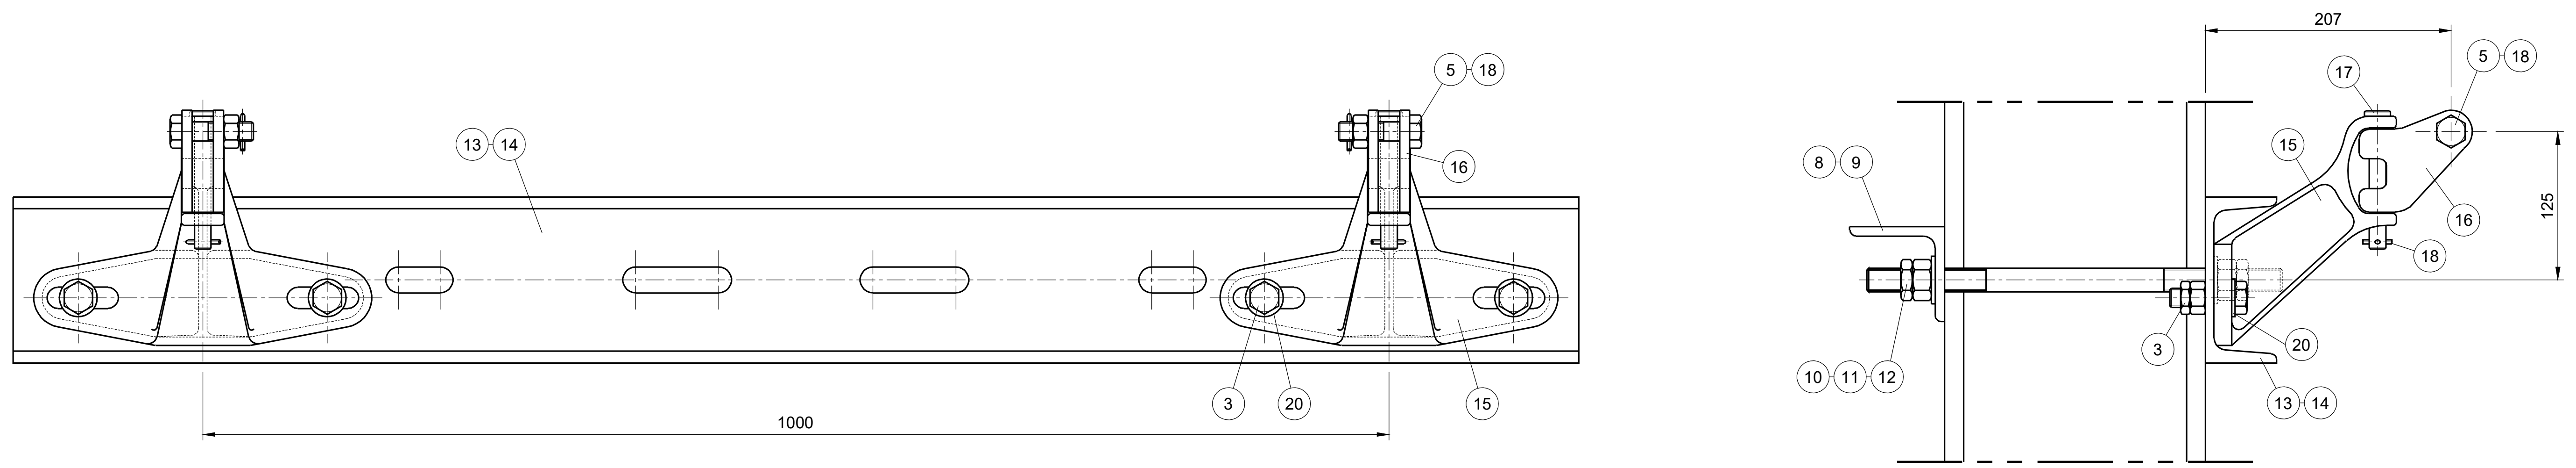

POSIÇÕES DE MONTAGEM

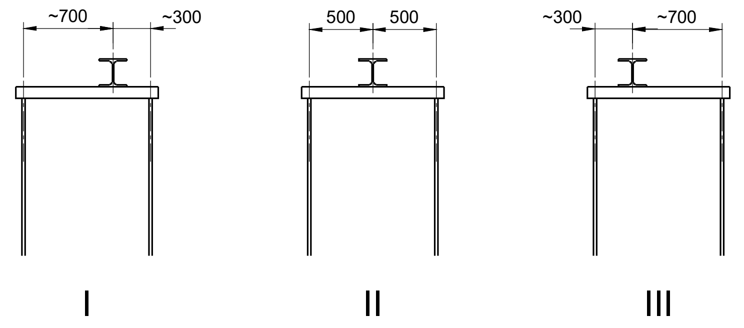

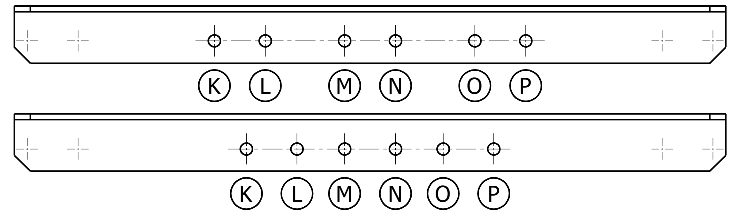

Ref. 1 (Postes 180 a 240)

Ref. 19 (Postes 260 a 450)

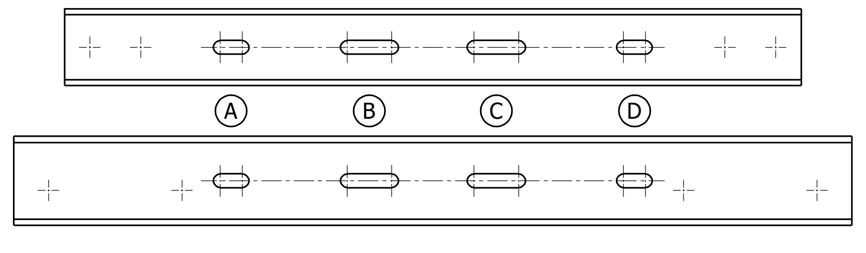

Ref. 6 (Postes 180 a 240)

Ref. 13 (Postes 180 a 240)

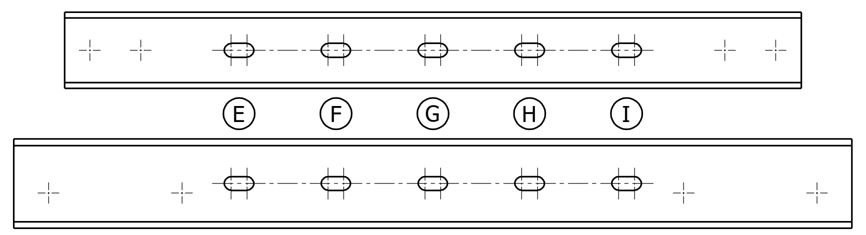

Ref. 7 (Postes 260 a 450)

Ref. 14 (Postes 260 a 450)

POSIÇÃO de MONTAGEM	FURAÇÃO A UTILIZAR		
	Ref. 1/19	Ref. 6/13	Ref. 7/14
I	O + P	C + D	G + I
II	M + N	B + C	F + H
III	K + L	A + B	E + G

NOTAS:
1 - Para postes com aparelho tensor ver Des. C-2576
2 - Para postes duplos ver Des. C-8292
3 - Para montagem em pórtico (lado da via) ver:
Des. E-6134 (postes duplos)
Des. E-6135 (postes simples)

	04.300.04	4	4	4	-	-	-	-	-	Anilha M16		33124025	20	19A		
02.116.09	**02.106.20**	-	-	-	-	-	-	1	-	Cantoneira L90x90x9 (L=1120)	42044/2	75143071	19	123B		Ref. 2
	05.601.02	4	4	4	2	2	2	2	2	Chaveta V4x40		33114247	18	291B		
	05.600.01	2	2	2	-	-	-	-	-	Cavilha para Pé de Consola	45008	75115035	17	307		Ref. b/1
	05.300.37	2	2	2	-	-	-	-	-	Articulação para Pé de Consola	42002	75151006	16	515		Ref. 3
	05.300.35	2	2	2	-	-	-	-	-	Pé de Consola Articulado	42002	75117008	15	514A		Ref. 1
	02.209.07	1	1	-	-	-	-	-	-	Perfil U140x60x7 (L=1320)	42038/2	75141028	14	217B		Ref. 2
	02.209.06	-	-	1	-	-	-	-	-	Perfil U140x60x7 (L=1320)	42038/2	75141027	13	217A		Ref. 1
	04.407.12	2	-	-	2	-	-	-	-	Perno roscado M20x550/100 c/ 2Hu+2Hm+2anilhas		75115648	12	18V		
	04.407.07	-	2	-	-	2	-	-	-	Perno roscado M20x450/100 c/ 2Hu+2Hm+2anilhas		75115646	11	18Q		
	04.407.03	-	-	2	-	-	2	-	-	Perno roscado M20x350/100 c/ 2Hu+2Hm+2anilhas		75115644	10	18K		
02.114.02	**02.104.18**	1	1	-	1	1	-	-	-	Cantoneira L80x80x8 (L=410)	42040/2	75143041	9	121B		Ref. 4
02.114.02	**02.104.13**	-	-	1	-	-	1	-	-	Cantoneira L80x80x8 (L=350)	42040/2	75143036	8	121A		Ref. 3
	02.207.04	-	-	-	1	1	-	-	-	Perfil U120x55x7 (L=1160)	42040/2	75141021	7	213B		Ref. 6
	02.207.03	-	-	-	-	-	1	-	-	Perfil U120x55x7 (L=1160)	42040/2	75141020	6	213A		Ref. 5
	04.102.01	2	2	2	2	2	2	2	2	Parafuso M16x60/38 c/ Furo e Hu		75115402	5	16D8		
	04.101.11	-	-	-	4	4	4	4	4	Parafuso M16x45/38 c/ Hu+Hm		33144358	4	16D3		
	04.101.13	4	4	4	-	-	-	2	2	Parafuso M16x55/38 c/ Hu+Hm		33144384	3	16D6		
	05.400.05	-	-	-	2	2	2	2	2	Suporte de Fixação do Tirante	42001	75116100	2	512		Ref. 1
02.116.09	**02.106.19**	-	-	-	-	-	-	-	1	Cantoneira L90x90x9 (L=1120)	42044/2	75143070	1	123A		Ref. 1
		QUANTIDADE								DESIGNAÇÃO	Nº DESENHO	NOMENCLAT.	Nº REF.	CÓDIGO (MN.CAT.003)	PESO Kg	OBSERVAÇÕES
		Postes HEA ou HEB 340 a 450	Postes HEA ou HEB 260 a 320	Postes HEA ou HEB 180 a 240	Postes HEA ou HEB 340 a 450	Postes HEA ou HEB 260 a 320	Postes HEA ou HEB 180 a 240	Postes HEA ou HEB 260 a 450	Postes HEA ou HEB 180 a 240							
		c	b	a	c	b	a	b	a							
		C			TR			T								

MONTAGEM

Notas e historial de Alterações

B	Introdução da Ref. 20, de códigos, nomenclaturas e correções na tabela de peças	João Caldas	04/2014
A	-	-	09/1993
Alterações	Designação	Assinatura	Data

Logótipos e informação complementar
Projetista
REFER ENGINEERING
Data
23-04-2014
N.º Projetista

E-6180

Levantou
Desenhou Araújo
Projetou
Verificou André Frederico

REFER
ACADEMIA REFER
INOVAÇÃO E CONHECIMENTO

Especialidade Técnica
CATENÁRIA E ENERGIA

Título do Desenho
CONSOLAS DUPLAS
FIXAÇÃO DOS TIRANTES E PÉS DE CONSOLA

ESTE DESENHO APENAS SE CONSIDERA VÁLIDO DESDE QUE ESTEJAM PREENCHIDOS OS CAMPOS DE APROVAÇÃO E INSERIDO O RESPETIVO NUMERO SAP

Departamento de Catenária e Energia
Marco Santos

Escalas
1:5 e 1:10

Tipo		N.º SAP		N.º de Ordem no Projeto		Versão
222	-	10002000915	-	-	-	01

O Diretor de Estudos e Projetos
Luís Cipriano Ferreira
Data
23-04-2014