MONTAGEM A

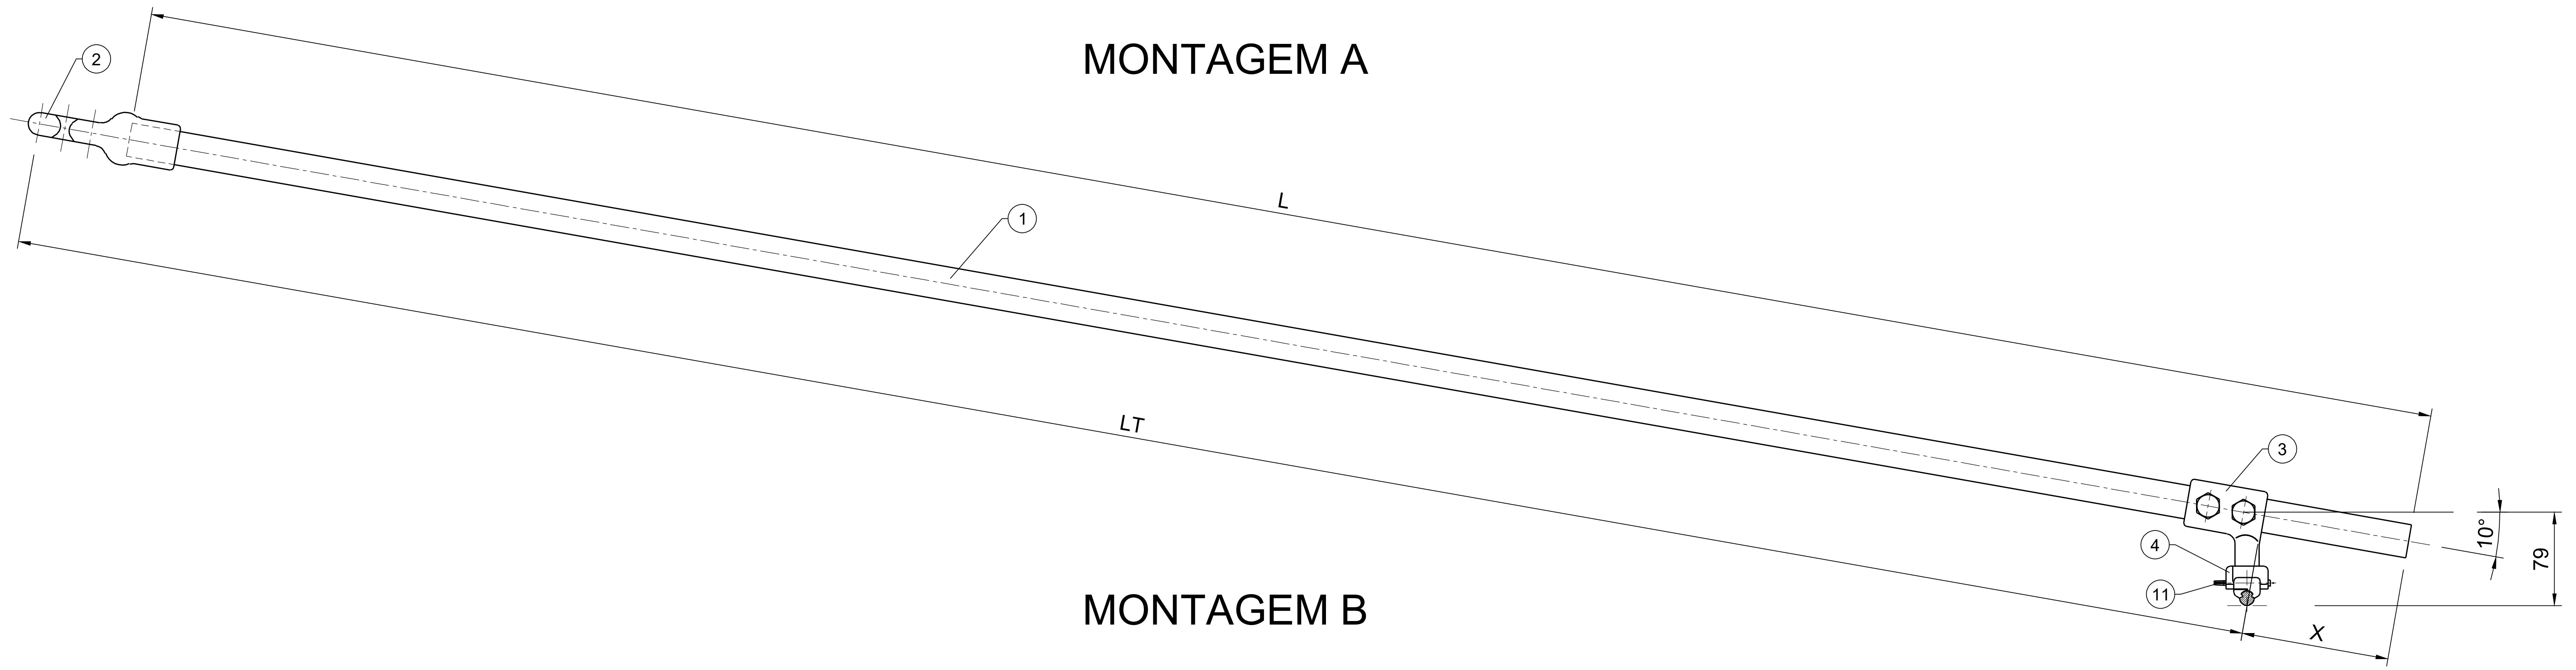

MONTAGEM B

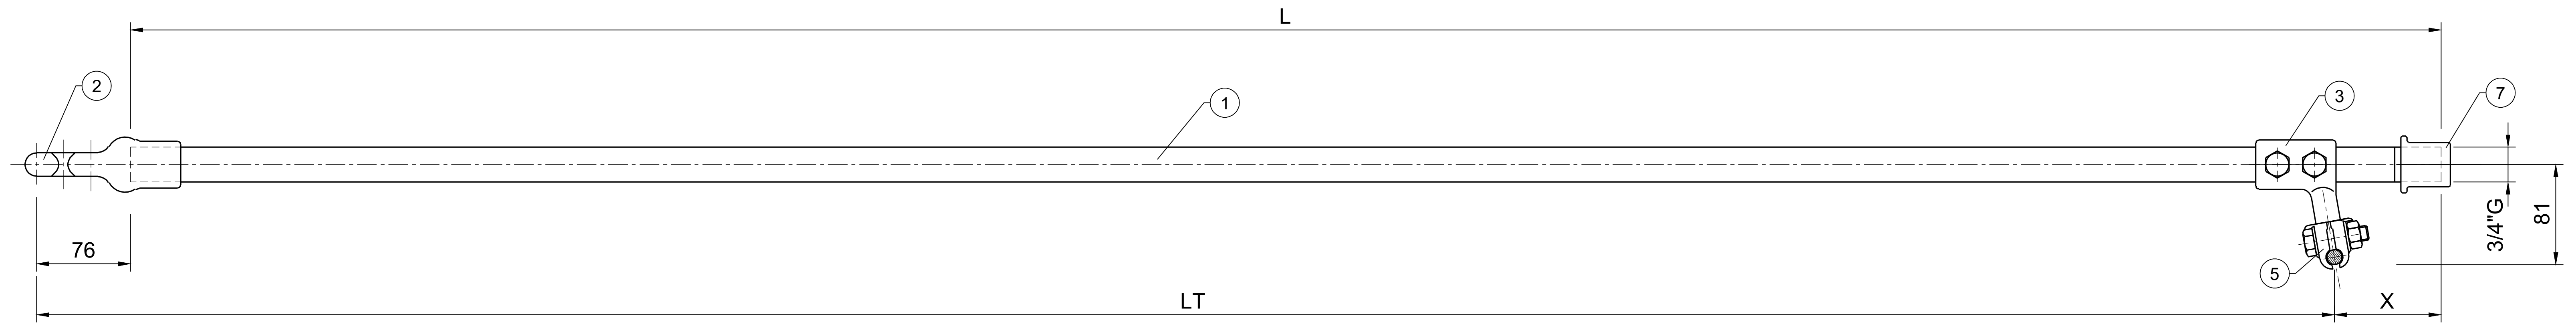

MONTAGEM C

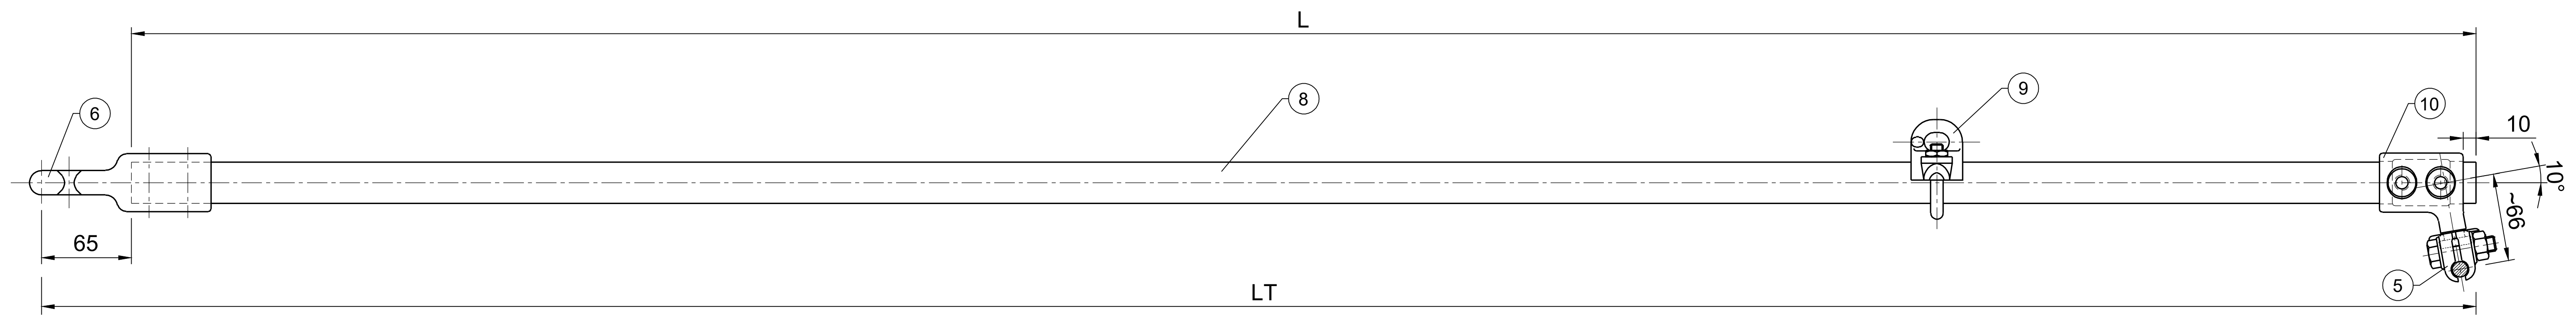

X { Max.= 100
Med.= 62
Min.= 25

LT = L-14 (X = 62)

	QUANTIDADE			DESIGNAÇÃO	Nº DESENHO	NOMENCLAT.	Nº REF.	CÓDIGO (MN.CAT.003)	PESO Kg	OBSERVAÇÕES
	C	B	A							
05.601.02	-	-	1	Chaveta V4x40		33114247	11	291B		
05.300.27+04.205.02	1	-	-	Coronha com manga de aperto p/ antibalançante 24x32	C-6401	75117058 75115458	10	558C+558B		Ref. 3 Ref. 2
05.301.05	1	-	-	Aperta tubo com olhal p/ antibalançante 24x32	42015	75161107	9	524		Ref. 1
02.502.03	1	-	-	Tubo em aço 24x32 (l=variável)		15105170	8	10C		
	-	1	-	Tampão fêmea 3/4" G		33506020	7	**719**		
05.300.18	1	-	-	Gancho com parafuso de ponto p/ tubo 24x32	42005	75112020	6	536A		Ref. 2
05.100.08	1	1	-	Pinça para antibalançante p/ F.C. sobrelevado	42019	75112125	5	348		Ref. 2
05.100.07	-	-	1	Griffe para antibalançante ou braço de chamada	44001	75162062	4	343		Ref. 4
05.300.26+04.205.02	-	1	1	Coronha com manga de aperto p/ antibalançante 19x26	C-6401	75117056 75115458	3	558A+558B		Ref. 1 Ref. 2
05.300.17	-	1	1	Gancho roscado p/ tubo 19x26	42005	75112010	2	537		Ref. 1
02.502.01	-	1	1	Tubo em aço 19x26 (l=variável)		15105163	1	10A		

MONTAGEM

Notas e historial de Alterações

Alterações	Designação	Assinatura	Data
A	Substituição das peças ref. 10 e 11, introdução de nomenclaturas e correções na tabela de peças	João Caldas	02/2014

Logótipos e informação complementar
Projetista
REFER ENGINEERING
Data
21-02-2014
N.º Projetista
E-6185

Levantou
Desenhou Miranda
Projetou
Verificou André Frederico

REFER
ACADEMIA REFER
INOVAÇÃO E CONHECIMENTO

Especialidade Técnica
CATENÁRIA E ENERGIA

Título do Desenho
ANTIBALANÇANTE
DIRETO E SOBRELEVADO

ESTE DESENHO APENAS SE CONSIDERA VÁLIDO DESDE QUE ESTEJAM PREENCHIDOS OS CAMPOS DE APROVAÇÃO E INSERIDO O RESPETIVO NUMERO SAP

Departamento de Catenária e Energia
Marco Santos

Escalas
1:5

Tipo		N.º SAP		N.º de Ordem no Projeto		Versão
222	-	10002000919	-	-	-	01

O Diretor de Estudos e Projetos
Luís Cipriano Ferreira
Data
21-02-2014

297 x 841