297 x 631

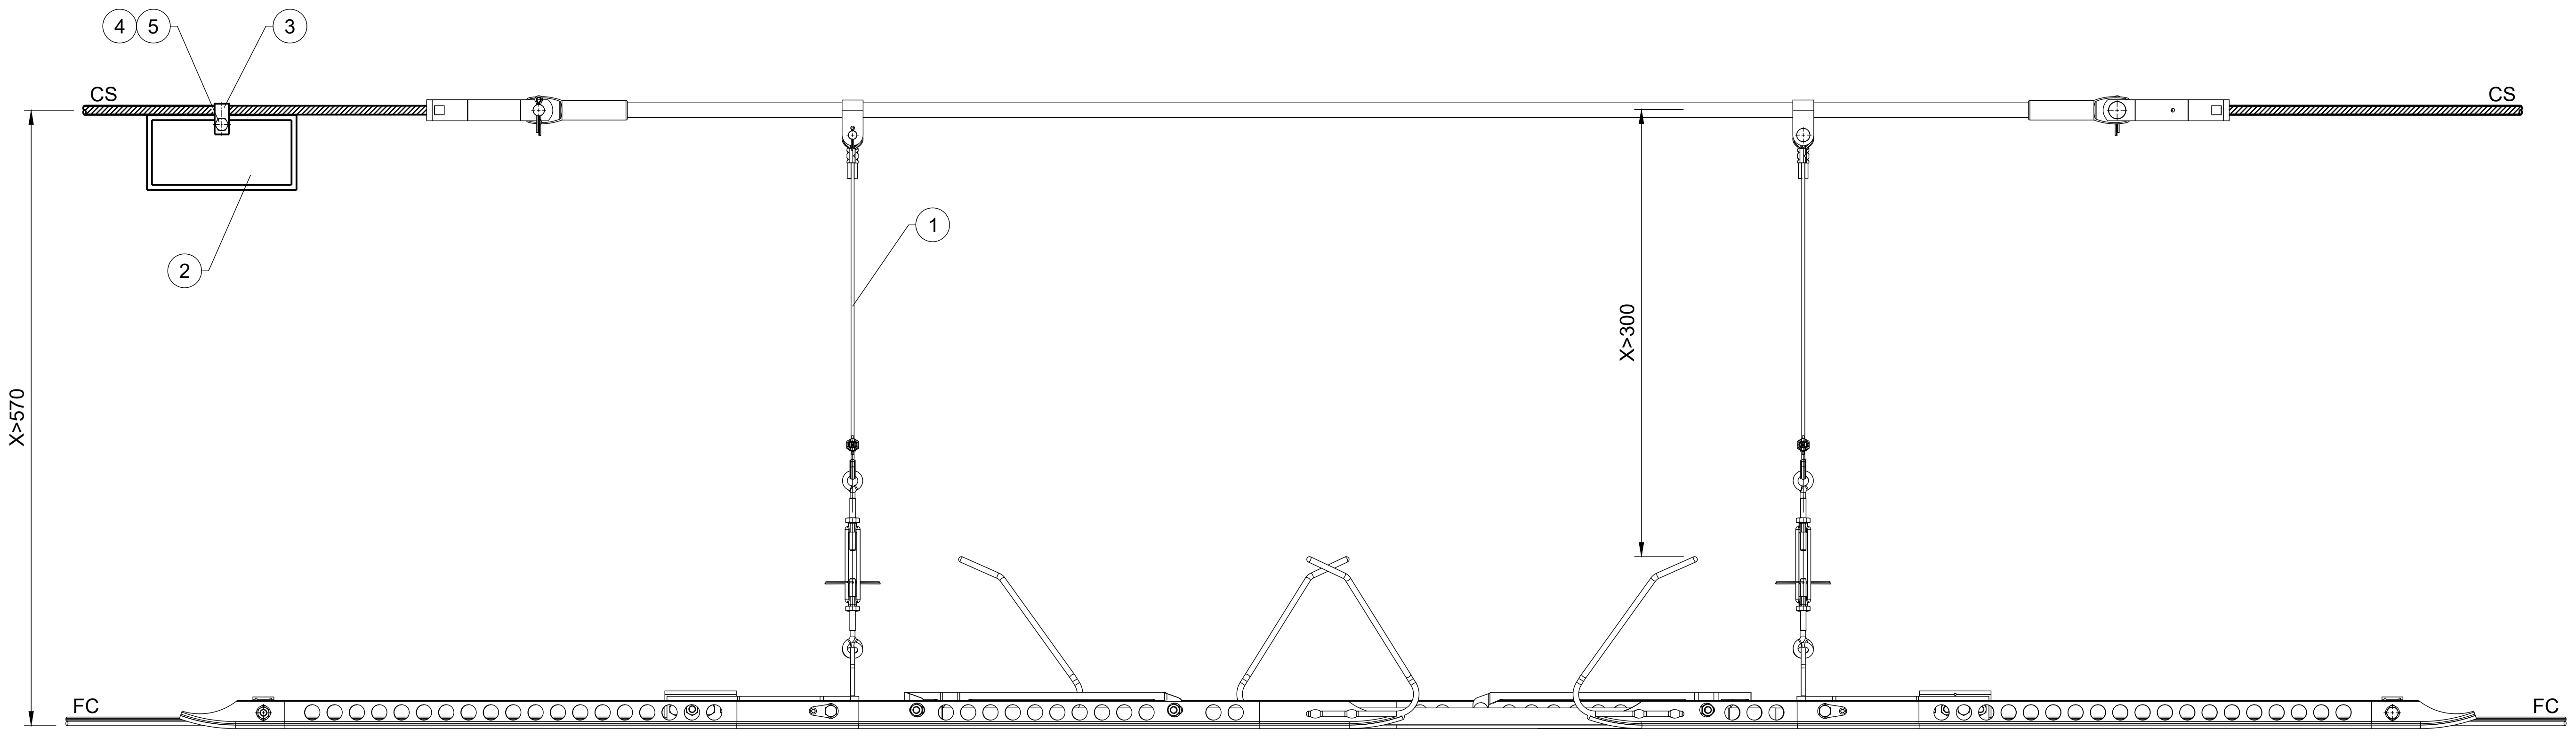

Quant.	DESIGNAÇÃO		DESENHO	NOMENCLAT.	REF.ª	CÓDIGO (GR.MN.CAT.003)	OBSERVAÇÕES
1	Chaveta V3.2x40	Cód. 291C		33114238	5	05.601.01	
1	Parafuso M10x30/26 c/ furo+Hu	Cód. 17A		75115481	4	04.204.01	
1	Cavaleiro p/ cabo Bz 65 mm²	Cód. 293B	44005	75167112	3	05.702.01	Ref. 11
1	Placa p/ identificação do isolador de secção	Cód. 383	E-6199	75121014	2	07.400.01	
1	Isolador de secção simétrico 25 kV Arthur Flury	Cód. 654	EC-379	75175019	1	07.100.01	

Notas e historial de alterações

Alterações	Designação	Assinatura	Data
B	Alteração da amarração do elemento isolante.	João Caldas	10-2022
A	Alteração da nomenclatura.	Feliciano Fernandes	07-2009

Logótipos e informação complementar

Projetista

Data
20-10-2022
N.º Projetista

EC-216

Levantou

Desenhou João Caldas

Projetou

Verificou Marco Santos

Infraestruturas de Portugal

Direção de Engenharia e Ambiente

Unidade de Catenária e Energia de Tração

Especialidade Técnica

CATENÁRIA E ENERGIA DE TRAÇÃO

Título do Desenho

ISOLADOR DE SECÇÃO SIMÉTRICO 25 kV
ARTHUR FLURY
MONTAGEM

Este desenho é propriedade da Infraestruturas de Portugal S.A.
A reprodução parcial ou integral está sujeita à autorização prévia da Infraestruturas de Portugal S.A.

ESTE DESENHO APENAS SE CONSIDERA VÁLIDO DESDE QUE ESTEJAM PREENCHIDOS OS CAMPOS DE APROVAÇÃO E INSERIDO O RESPETIVO NUMERO SAP

O Responsável por
Catenária e Energia de Tração
Marco Santos

O Responsável por
Estudos e Projetos Ferroviários
Fernando Vendas

O Diretor de Engenharia e Ambiente
José Alves Monteiro
Data
20-10-2022

Escalas
-

Tipo		N.º SAP		N.º de Ordem no Projecto		Versão
222	-	10002001247	-	-	-	02