NOTA: Para postes duplos ver Desº C-5214, Refª I

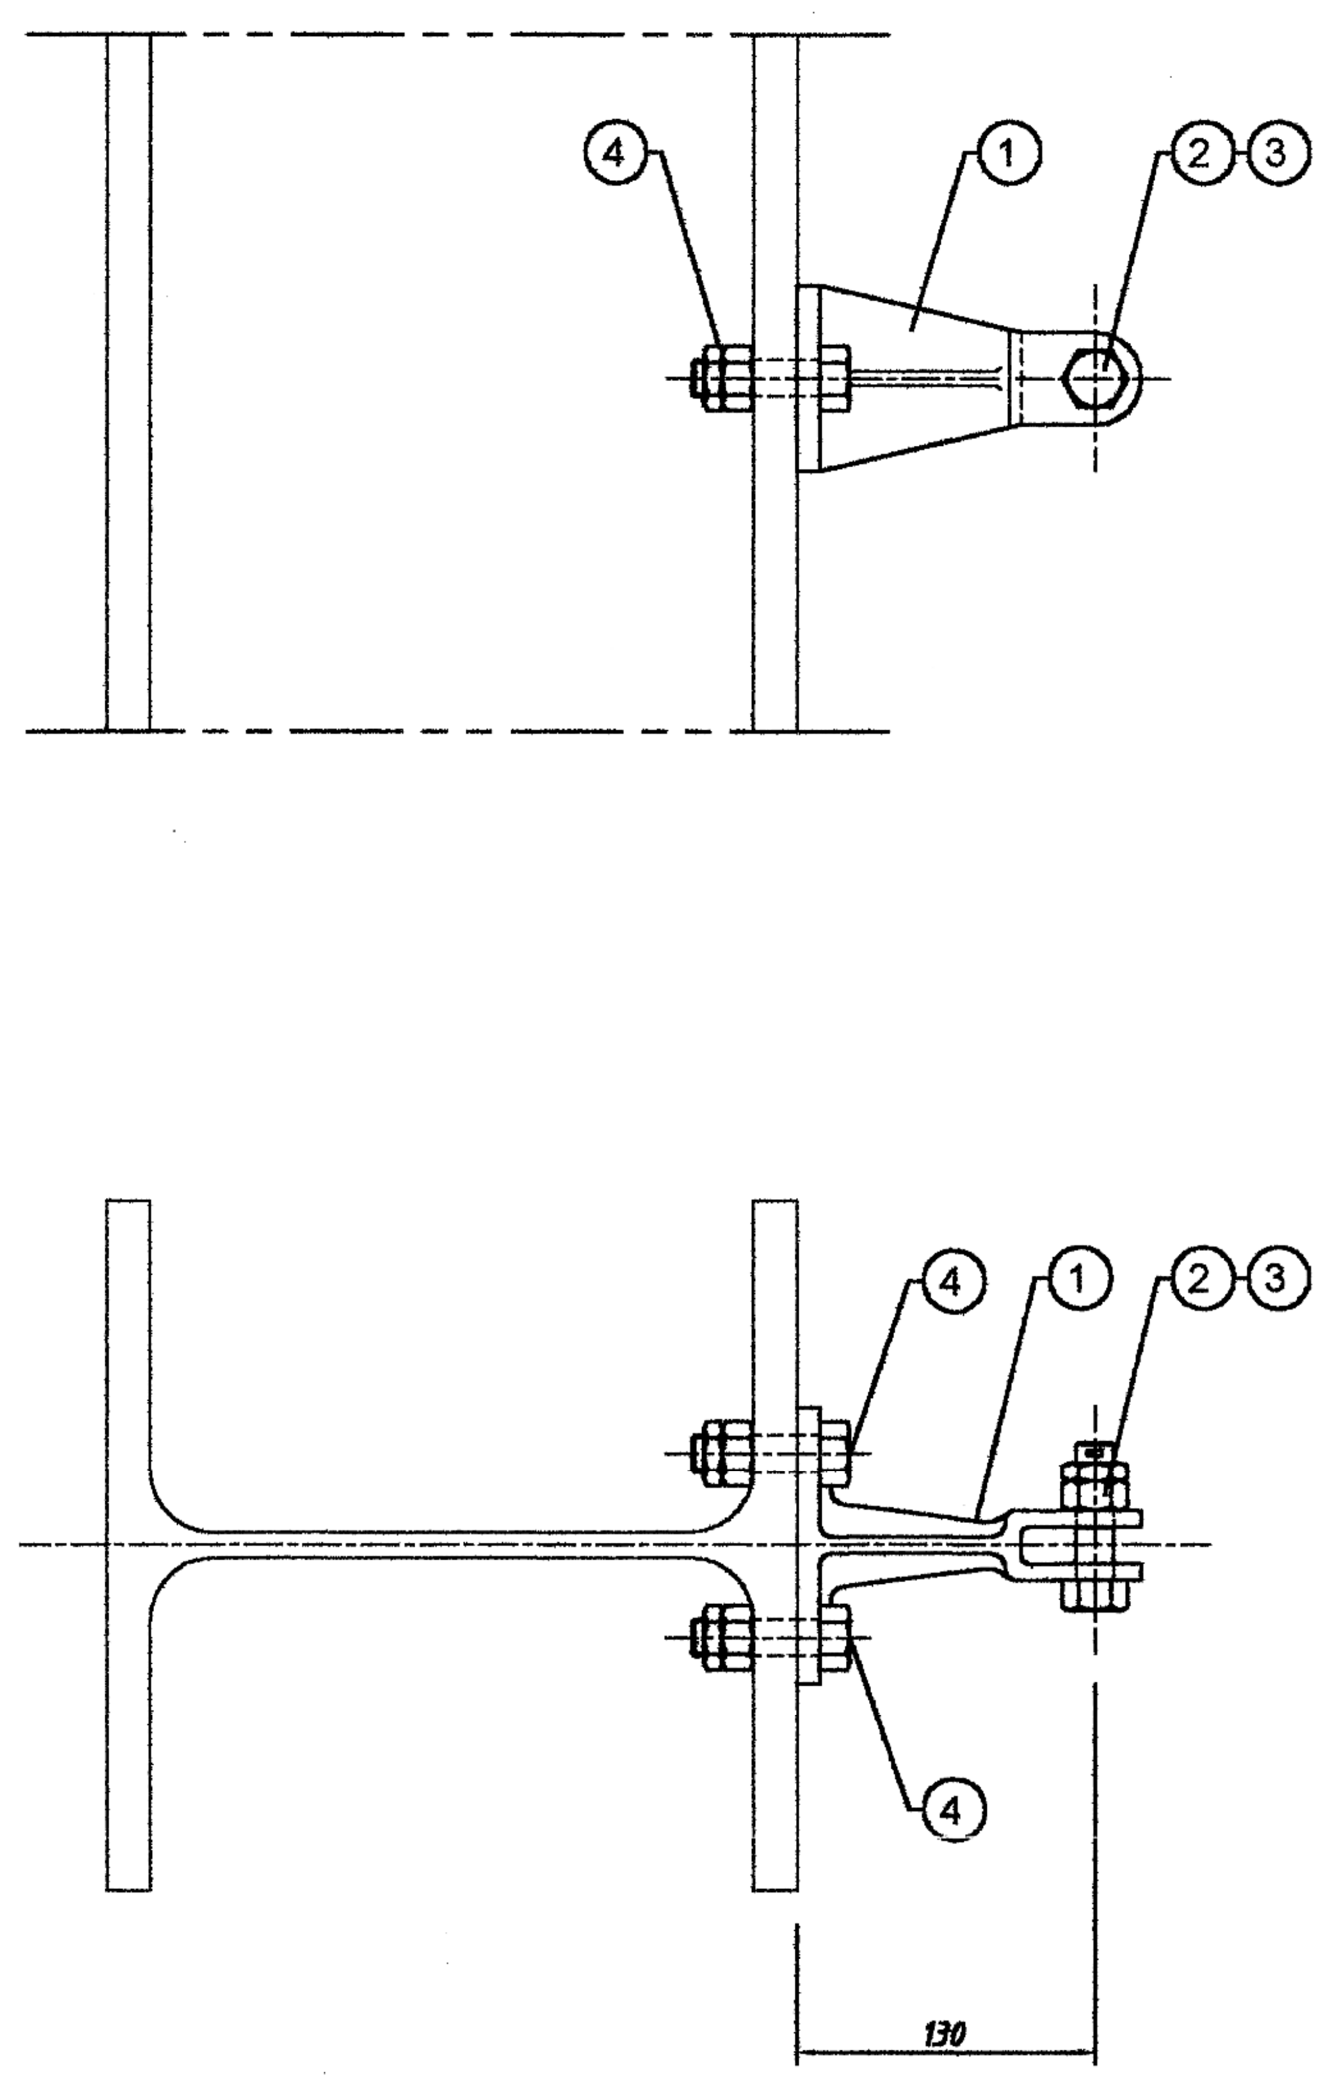

MONTAGEM I

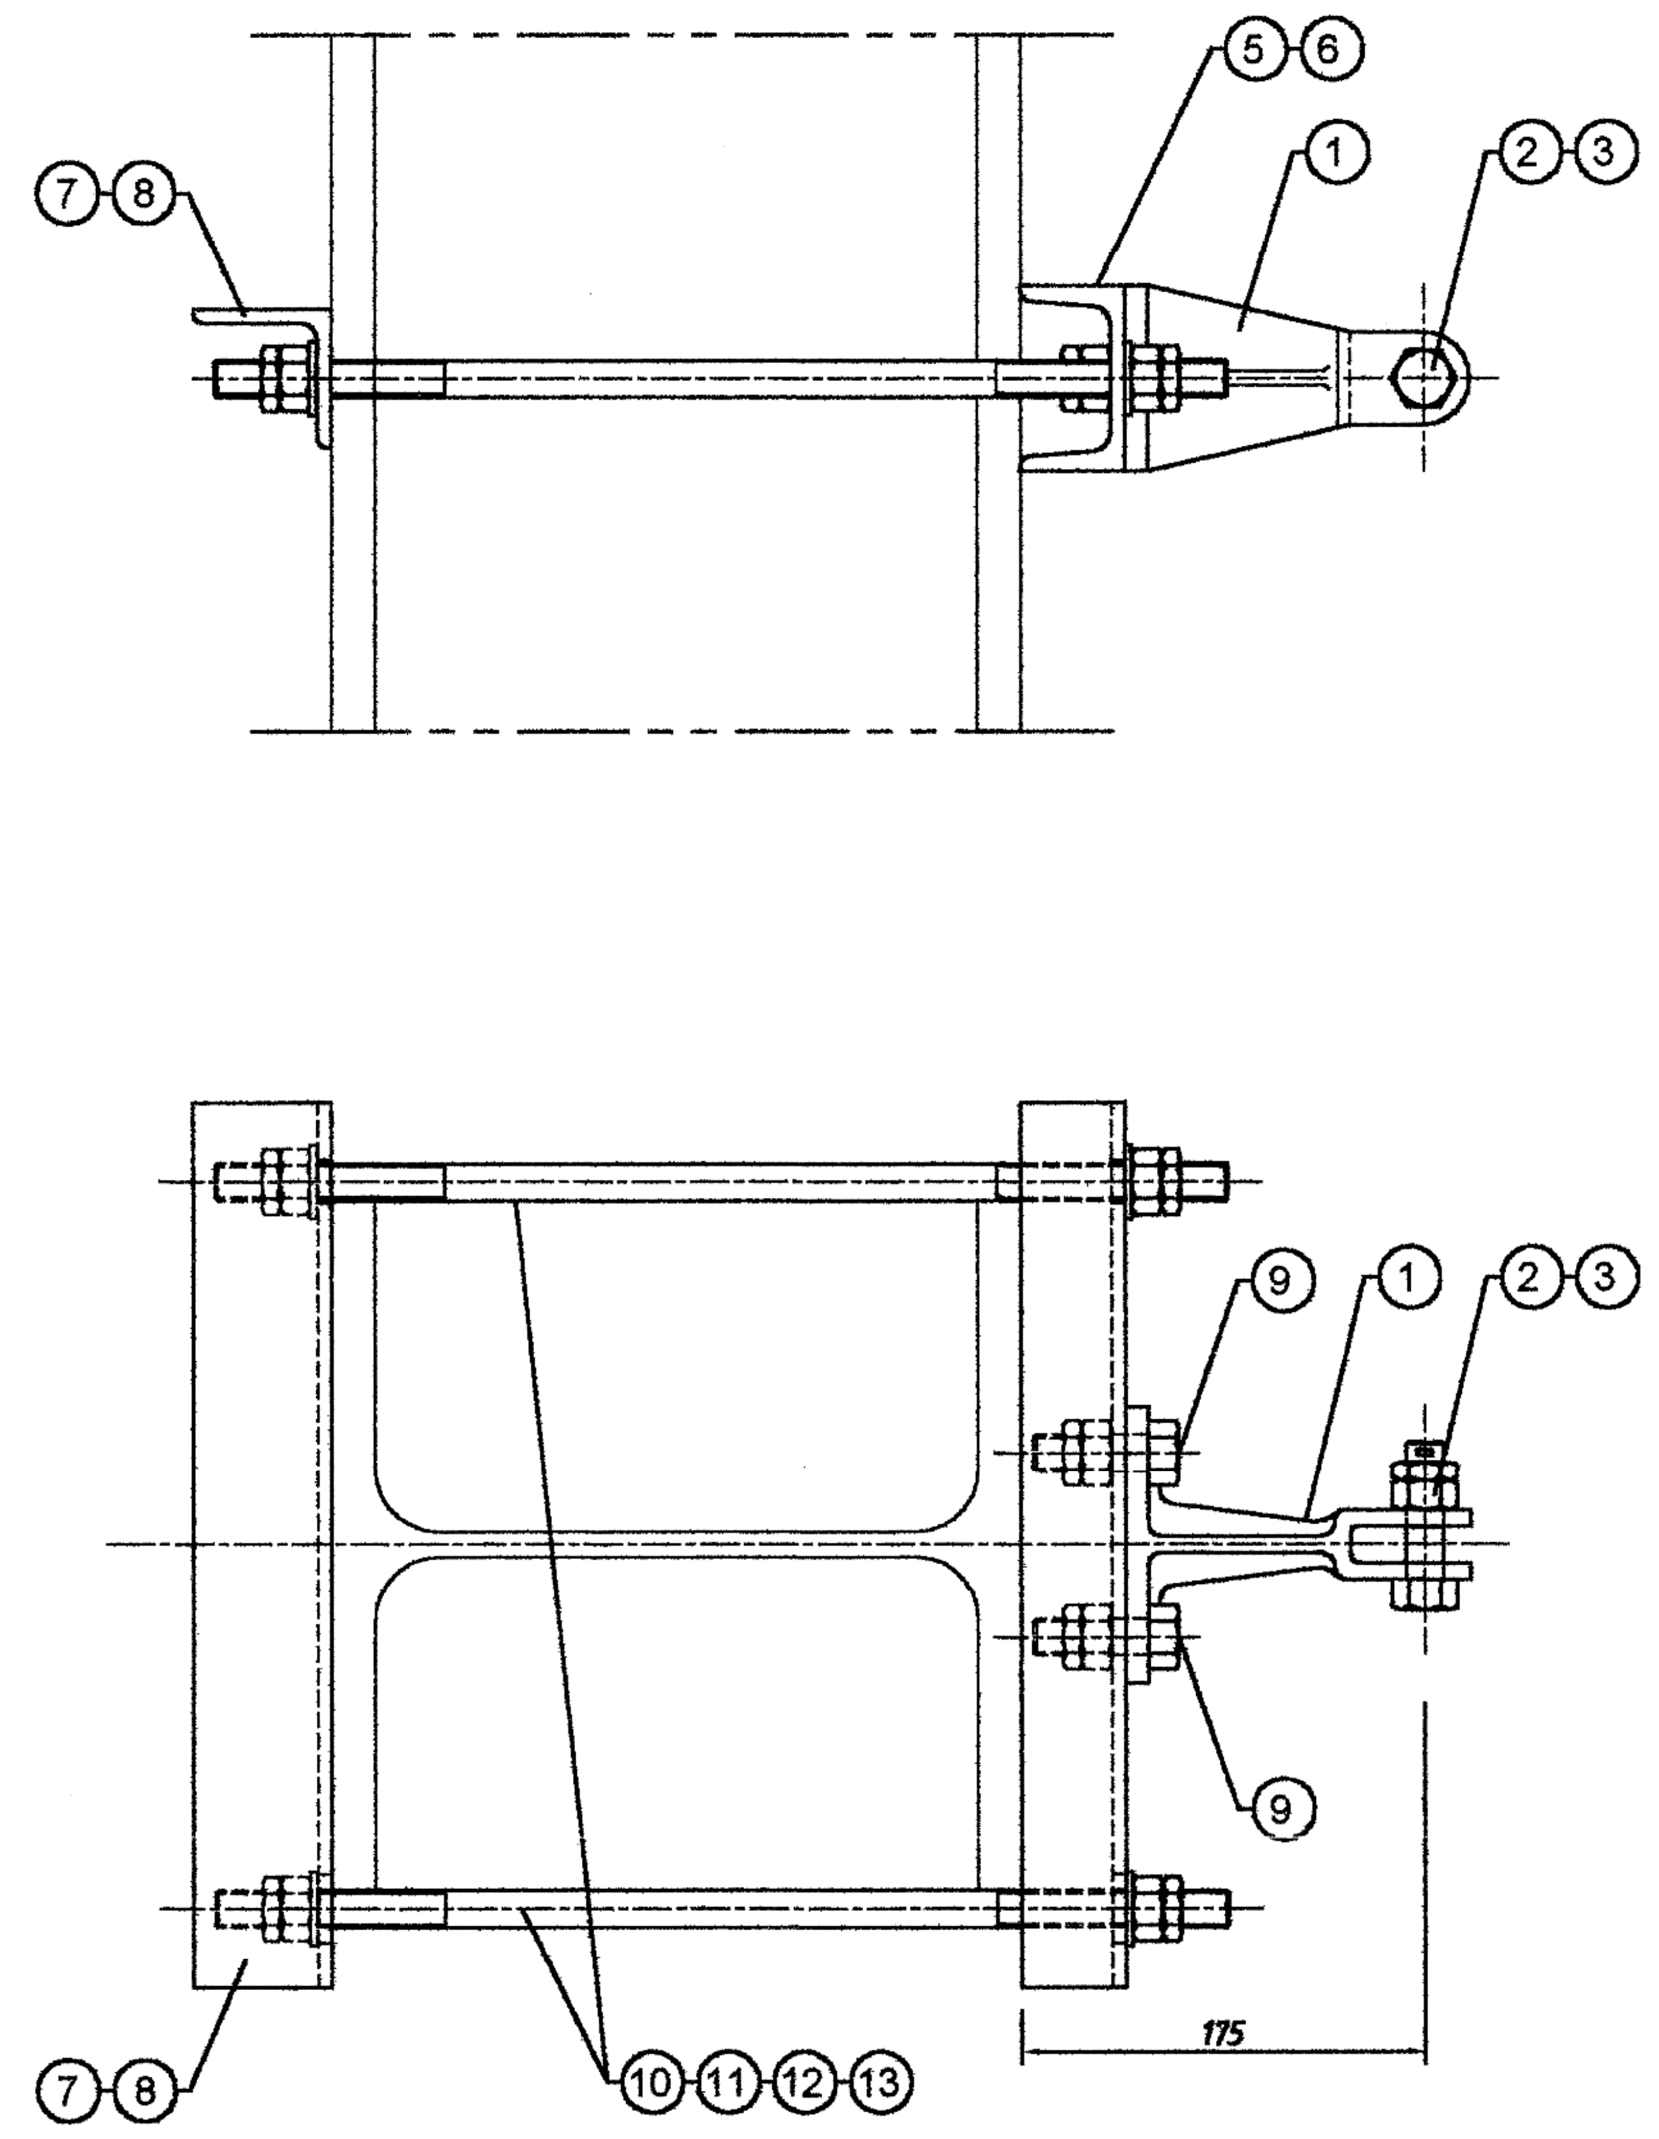

MONTAGEM II

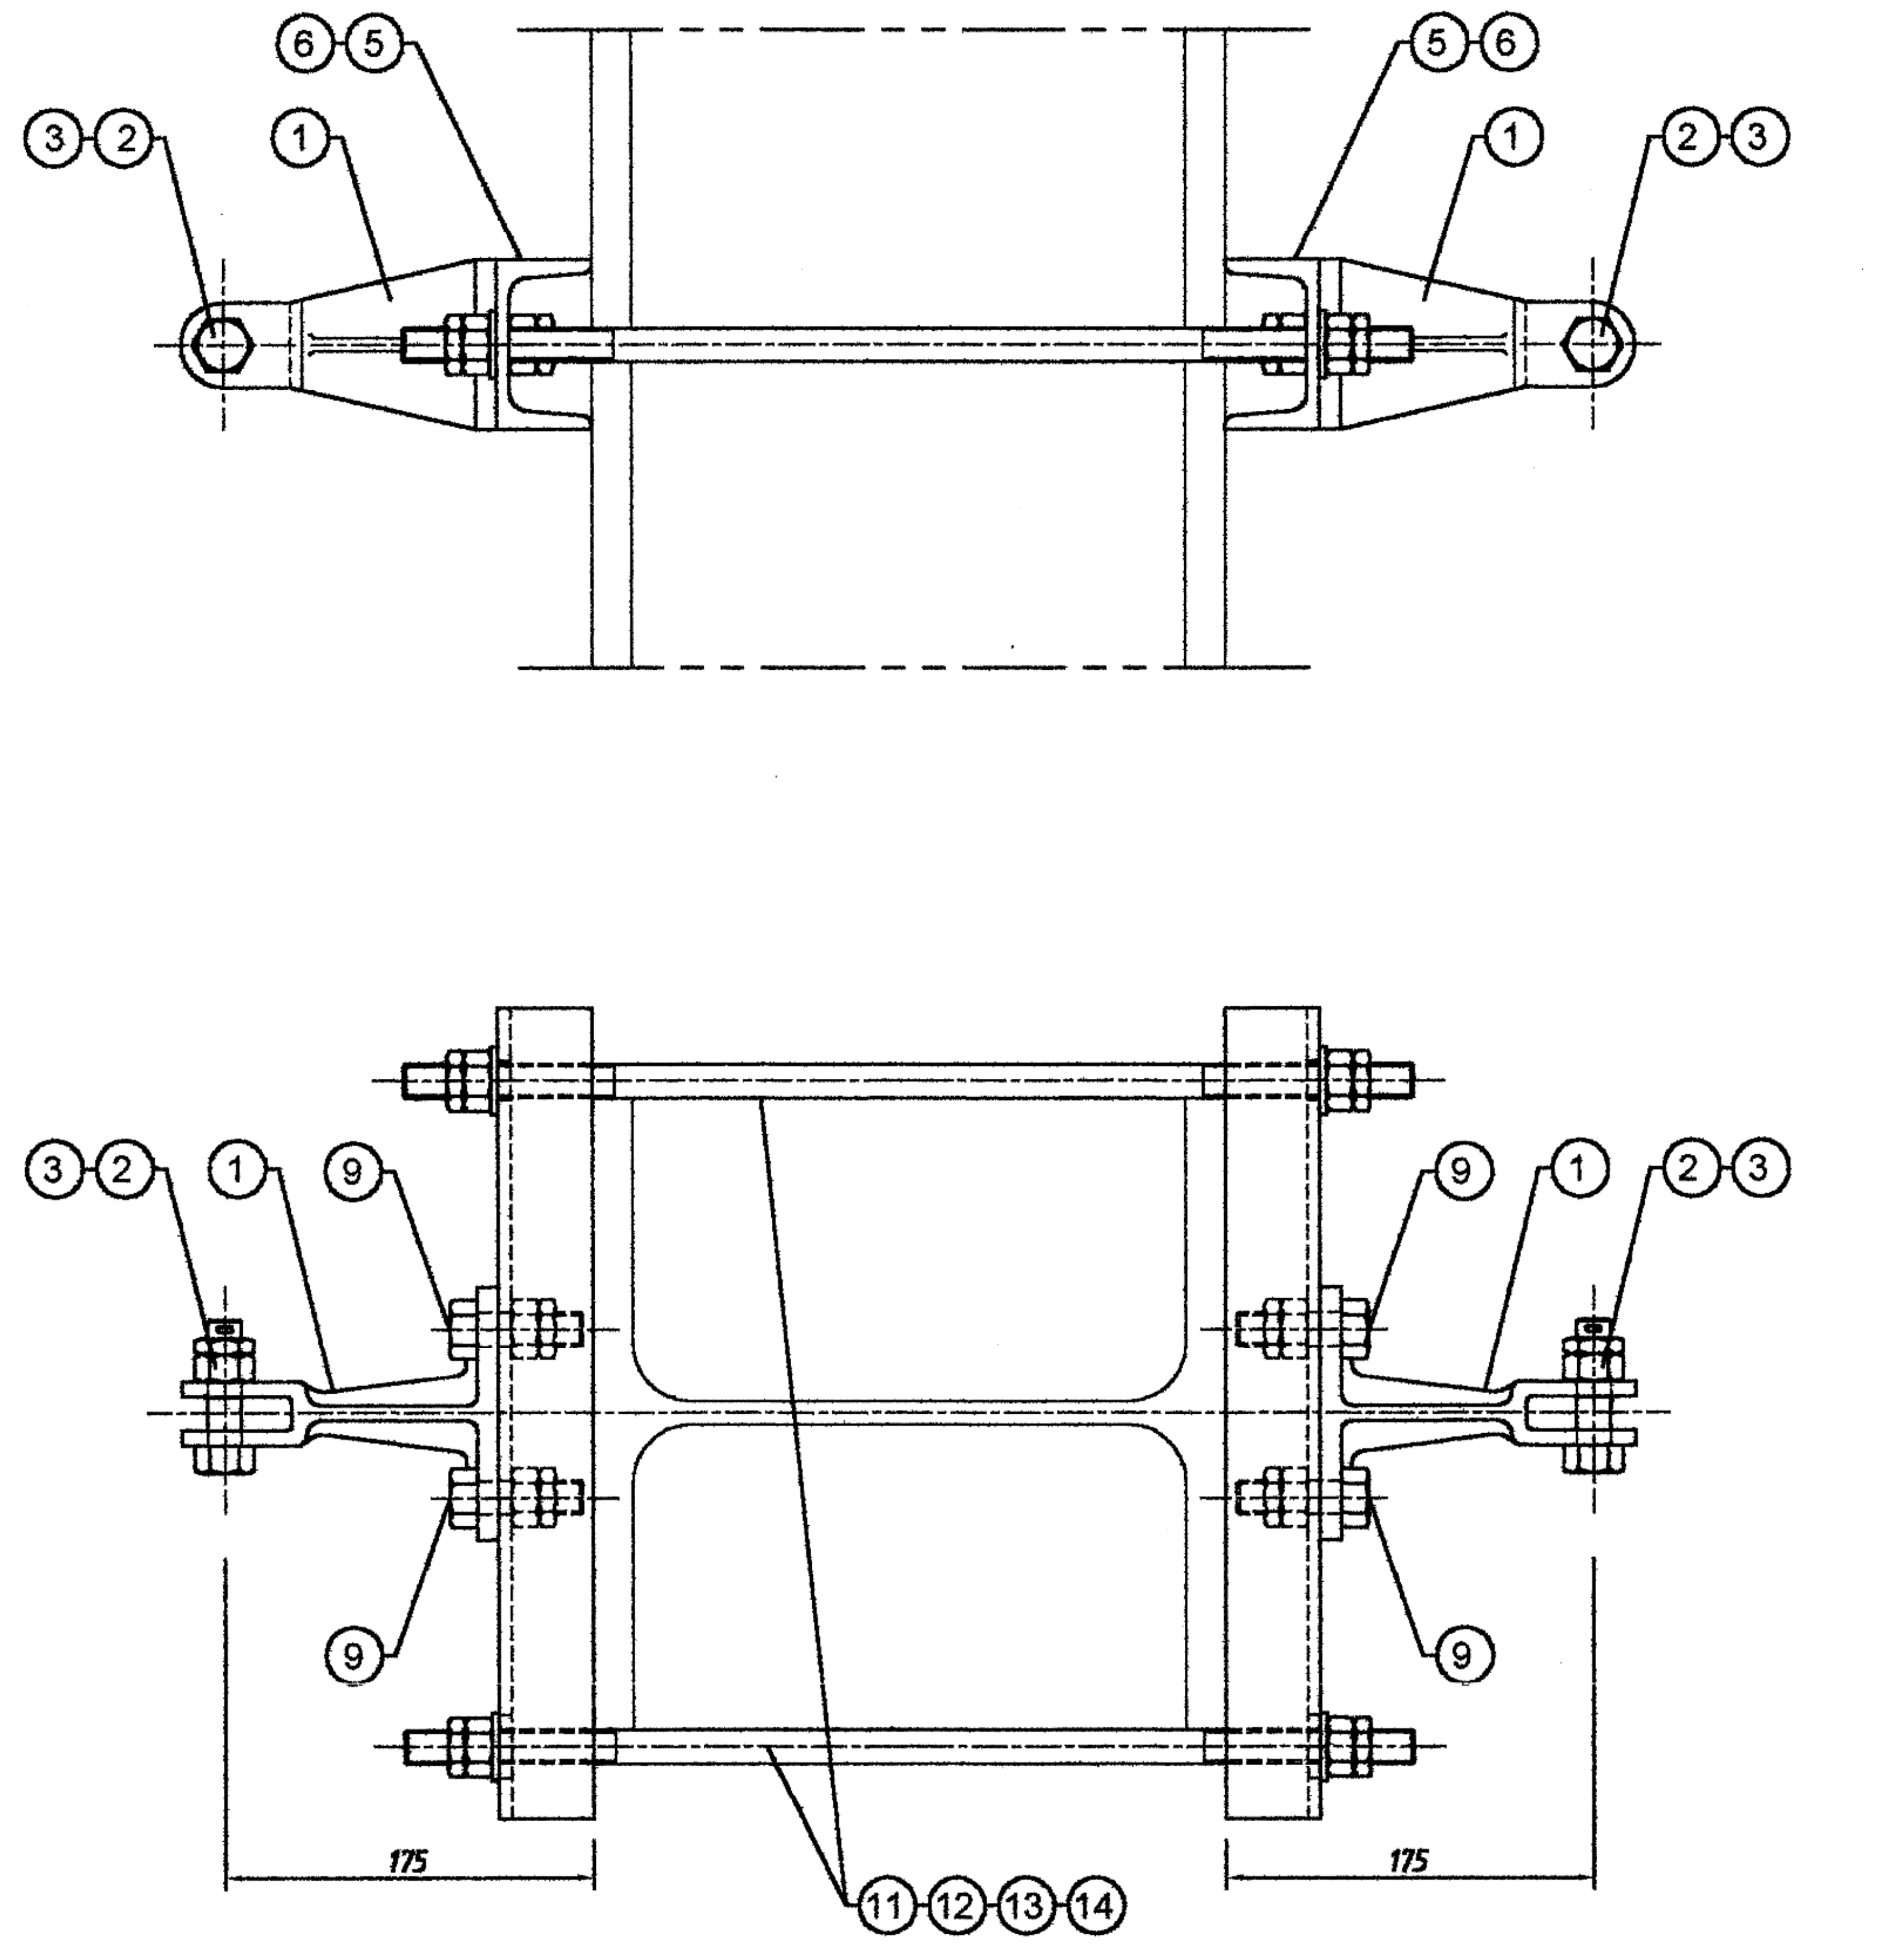

MONTAGEM III

Postes 38 a 45	Postes 34 a 36	Postes 24 a 32	Postes 16 a 22	Postes 38 a 45	Postes 34 a 36	Postes 24 a 32	Postes 16 a 22		DESIGNAÇÃO			Nº DES.	NOMENCL.	N.º REFª	CÓDIGO (IT-C-046)	PESO Kg	OBSERVAÇÕES
III				II				I									
d	c	b	a	d	c	b	a										
2	-	-	-	-	-	-	-	-	Peno roscado M16x650/100		04.403.09		75115617	14	18H2		
-	2	-	-	2	-	-	-	-	Peno roscado M16x600/100		04.403.08		75115621	13	18H1		
-	-	2	-	-	2	-	-	-	Peno roscado M16x500/100		04.403.06		75115619	12	18F		
-	-	-	2	-	-	2	-	-	Peno roscado M16x450/100		04.403.05		75115618	11	18E		
-	-	-	-	-	-	-	2	-	Peno roscado M16x350/100		04.403.03		75115614	10	18C		
4	4	4	4	2	2	2	2	-	Parafuso M16x50x38 c/Hu+Hm		04.101.12		33144359	9	16D4		
-	-	-	-	1	1	1	-	-	Cantoneira L60x6 (l=385)	02.112.02	02.100.12	42002	75143020	8	112B		Refª 6
-	-	-	-	-	-	-	1	-	Cantoneira L60x6 (l=305)	02.112.01	02.100.08	42002	75143010	7	112A		Refª 5
2	2	2	-	1	1	1	-	-	Ferro U80x45x6 (l=385)		02.203.04	42020	75141014	6	211B		Refª 2
-	-	-	2	-	-	-	1	-	Ferro U80x45x6 (l=305)		02.203.03	42020	75141012	5	211A		Refª 1
-	-	-	-	-	-	-	-	2	Parafuso M16x55x38 c/Hu+Hm		04.101.13		33144384	4	16D6		
2	2	2	2	1	1	1	1	1	Chaveta V4 x40		05.601.02		33114247	3	291B		
2	2	2	2	1	1	1	1	1	Parafuso M16x60/38 c/Hu e furo		04.102.01		75115402	2	16D8		
2	2	2	2	1	1	1	1	1	Suporte de fixação do tirante da consola		05.400.05	42001	75116100	1	512		Refª 1

Quantidades

Montagens

Alterações	Designação	Assinatura	Data
A	Introdução de nomenclaturas e informatização do desenho.		07/2002

FERBRITAS

Levantou		
Calculou		
Desenhou		03/2002
Coloborou		
Verificou		

Nº ____________________

REFER EP
INFRAESTRUTURAS - ENGENHARIA
CATENÁRIA ENERG.TRAC. - APOIO TÉCNICO

CATENÁRIA

FIXAÇÃO DO TIRANTE DE CONSOLA

DESº Nº **E-6179**

Escalas: 1:5

Data: 09/1990

O Responsável pelo Apoio Técnico

O Responsável pela Cat. e Energ.Tracção

O Responsável pela Engenharia