MONTAGEM A

(Tubo 24x32)

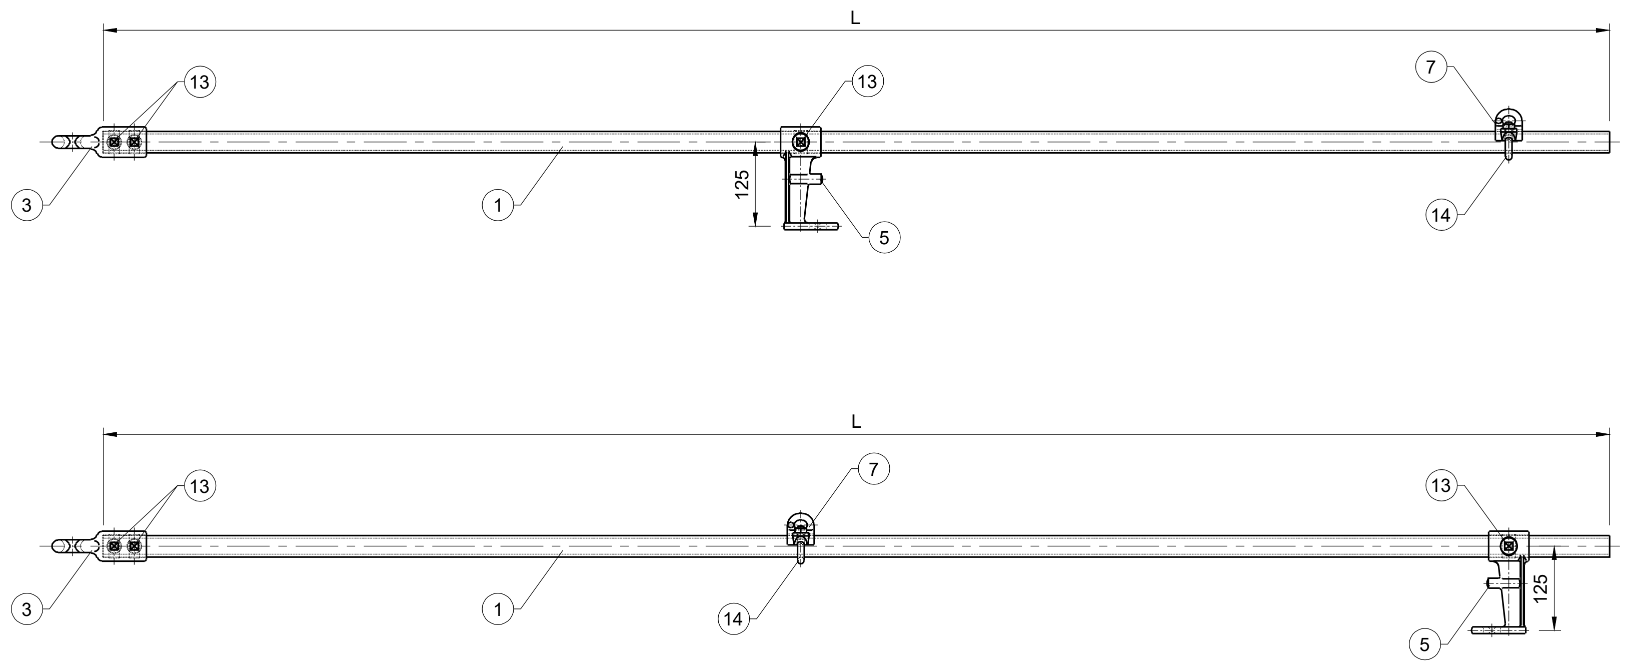

MONTAGEM B

(Tubo 34x42)

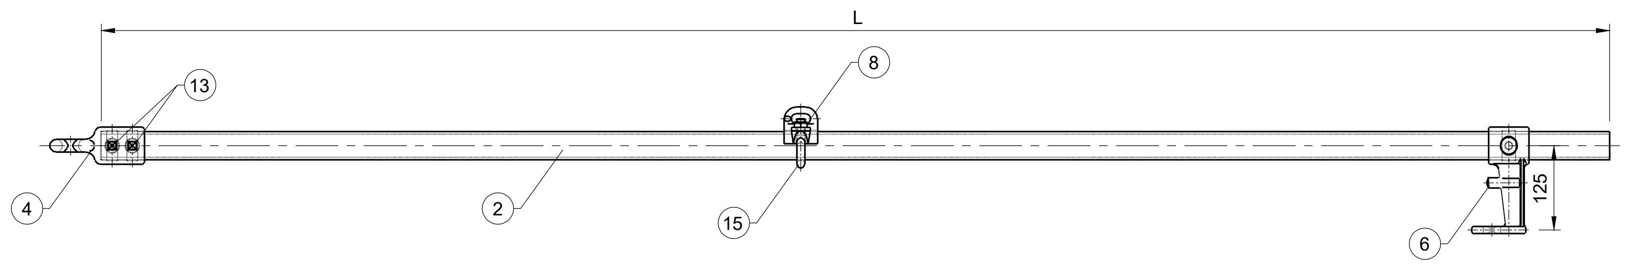

MONTAGEM E

(Tubo 24x32)

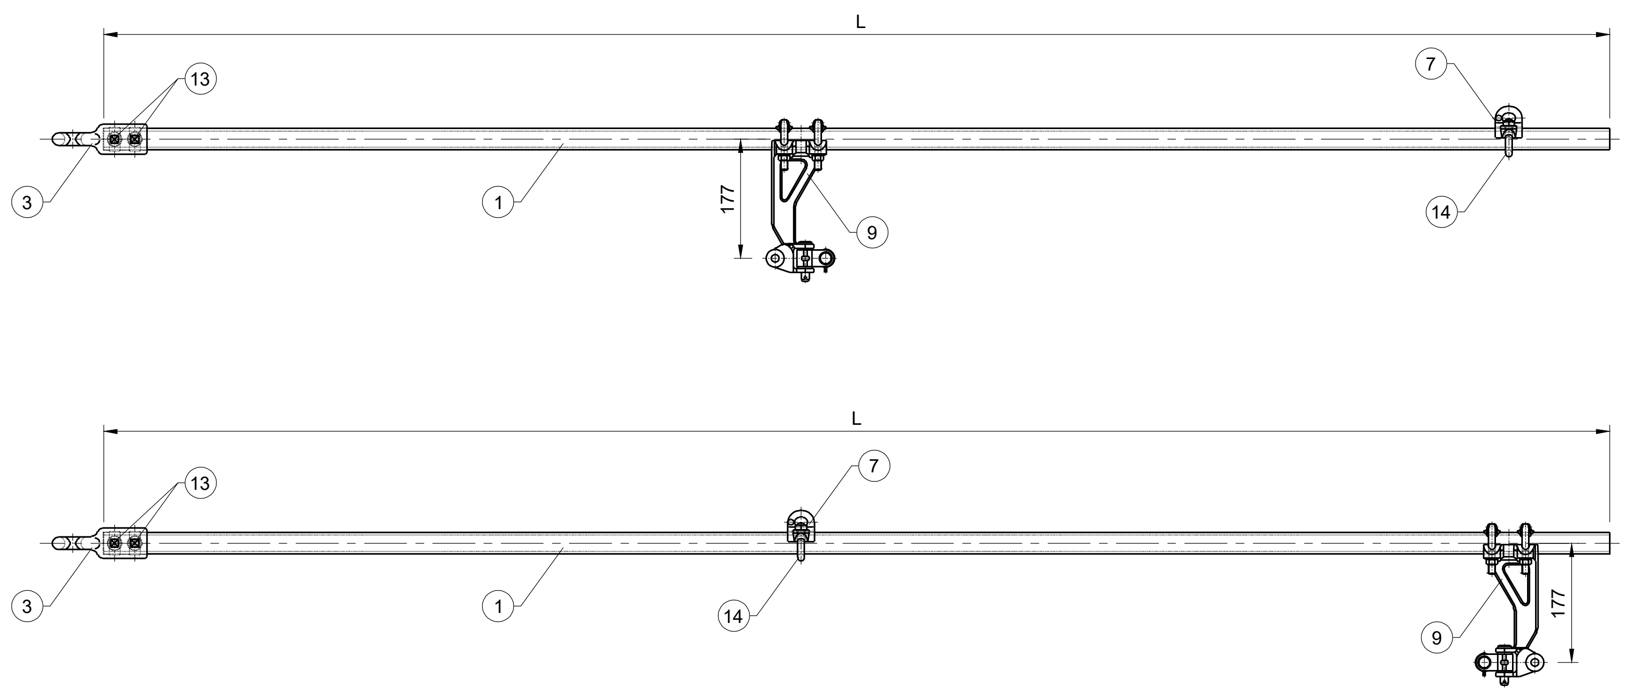

MONTAGEM F

(Tubo 34x42)

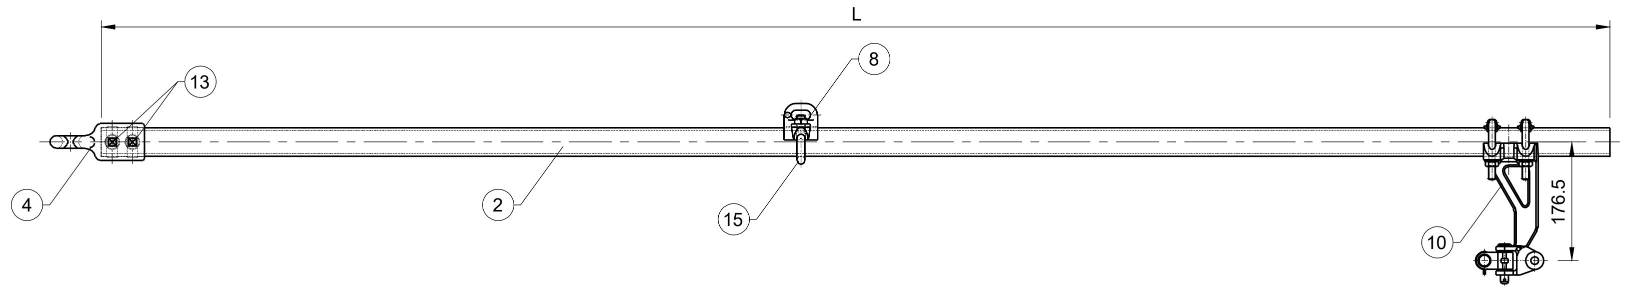

MONTAGEM G

(Tubo 24x32)

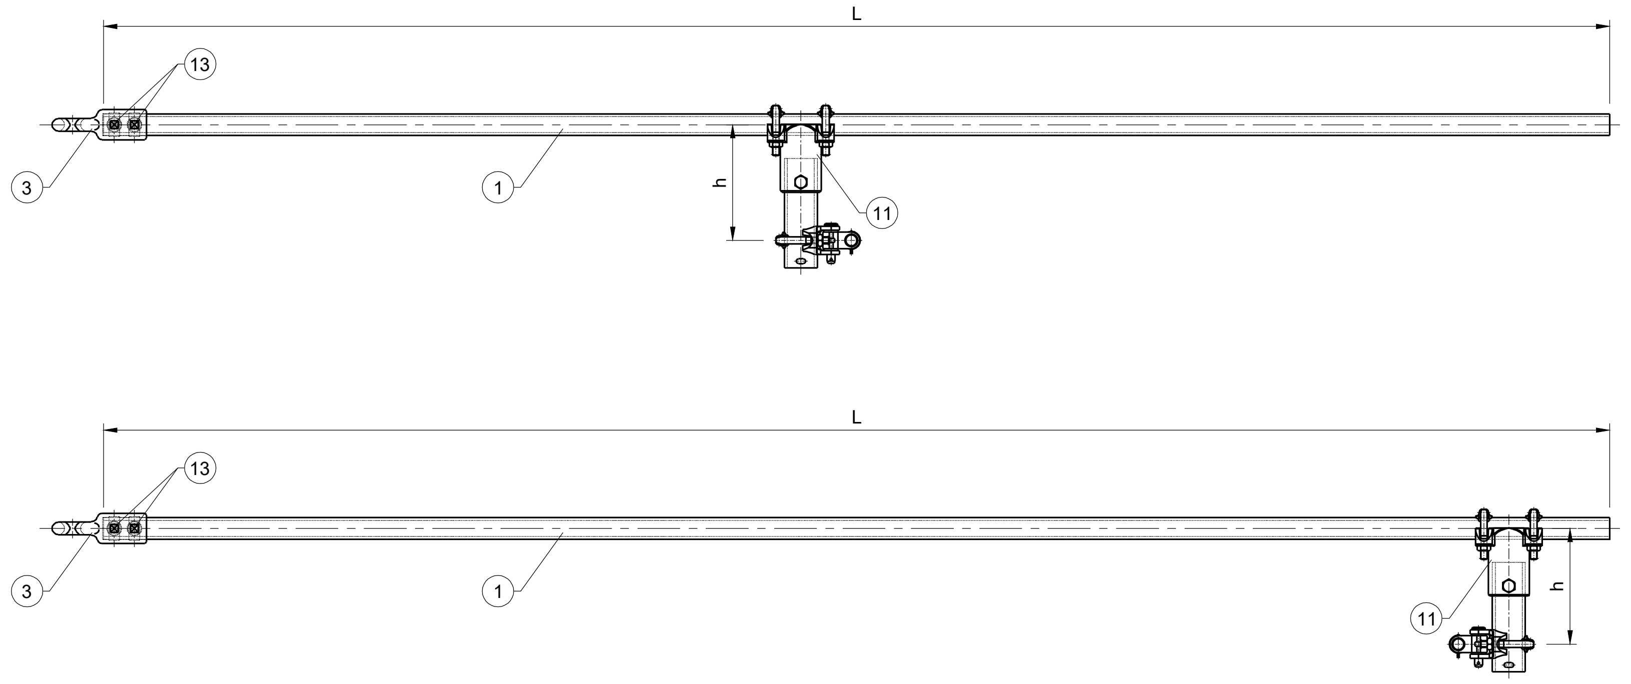

MONTAGEM H

(Tubo 34x42)

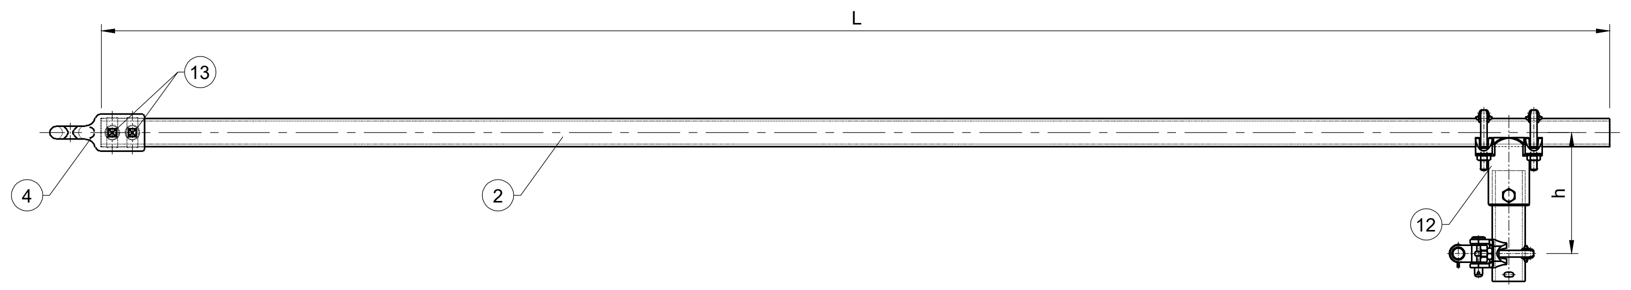

NOTA:

A cota h será definida no Caderno de Montagem.

H	G	F	E	B	A	DESIGNAÇÃO	DESENHO	NOMENCLAT.	REF.ª	CÓDIGO (GR.MN.CAT.003)	OBSERVAÇÕES
-	-	1	-	1	-	Braçadeira M12 c/ 2Hu Cod. 432D	EC-242	75112210	15	05.500.05	Ref.ª 4
-	-	-	1	-	1	Braçadeira M10 c/ 2Hu Cod. 432C		75112204	14	05.500.01	Ref.ª 3
2	2	2	2	3	3	Parafuso de cabeça quadrada, ponta chanfrada e côncava Cod. 442	43013	75115456	13	04.205.01	Ref.ª 4
1	-	-	-	-	-	Suporte de fixação reg. p/ braço de chamada p/ tubo 34x42 Cod. 628	E-7199	75116114	12	05.300.42	Mont. IIIA
-	1	-	-	-	-	Suporte de fixação reg. p/ braço de chamada p/ tubo 24x32 Cod. 672	EC-113	75116116	11	05.300.41	Mont. IIA
-	-	1	-	-	-	Suporte de fixação p/ braço de chamada p/ tubo 34x42 Cod. 627	E-7199	75116113	10	05.300.40	Mont. II
-	-	-	1	-	-	Suporte de fixação p/ braço de chamada p/ tubo 24x32 Cod. 642	EC-113	75116115	9	05.300.39	Mont. I
-	-	1	-	1	-	Aperta tubo c/ olhal p/ tubo 34x42 Cod. 525	42014	75161115	8	05.301.06	Ref.ª 1
-	-	-	1	-	1	Aperta tubo c/ olhal p/ tubo 24x32 Cod. 524	42015	75161107	7	05.301.05	Ref.ª 1
-	-	-	-	1	-	Aperta tubo c/ articulação p/ tubo 34x42 Cod. 518B	42013	75161063	6	05.301.04	Ref.ª 1
-	-	-	-	-	1	Aperta tubo c/ articulação p/ tubo 24x32 Cod. 518A	42012	75161055	5	05.301.03	Ref.ª 1
1	-	1	-	1	-	Gancho c/ parafuso de ponto p/ tubo 34x42 Cod. 536B	42005	75112030	4	05.300.19	Ref.ª 3
-	1	-	1	-	1	Gancho c/ parafuso de ponto p/ tubo 24x32 Cod. 536A		75112020	3	05.300.18	Ref.ª 2
qb	-	qb	-	qb	-	Tubo de aço 34x42 (L=variável) Cod. 10F		15105193	2	02.502.07	
-	qb	-	qb	-	qb	Tubo de aço 24x32 (L=variável) Cod. 10C		15105170	1	02.502.03	

QUANTIDADES

Zonas Neutras Seccionadas e AMV's tangenciais (H, G)

LP10 E LP12 (F, E)

Situações especiais (Braços de chamada LP1 a LP4) (B, A)

MONTAGEM

Notas e historial de alterações

Alterações	Designação	Assinatura	Data
D	Retiradas as Montagens C e D e introdução das Montagens G e H.	João Caldas	07-2020
C	Introdução das Montagens E e F.	Feliciano Fernandes	04-2010

Logótipos e informação complementar

Projetista

Data
28-07-2020
N.º Projetista

E-6183

Levantou

Desenhou João Caldas

Projetou

Verificou Marco Santos

Infraestruturas de Portugal

Direção de Engenharia e Ambiente

Unidade de Catenária e Energia de Tração

Especialidade Técnica

CATENÁRIA E ENERGIA DE TRAÇÃO

Título do Desenho

ANTIBALANÇANTE PARA CONSOLA

ESTE DESENHO APENAS SE CONSIDERA VÁLIDO DESDE QUE ESTEJAM PREENCHIDOS OS CAMPOS DE APROVAÇÃO E INSERIDO O RESPETIVO NUMERO SAP

O Responsável por
Catenária e Energia de Tração
Marco Santos

O Responsável por
Estudos e Projetos Ferroviários
Fernando Vendas

O Diretor de Engenharia e Ambiente
José Alves Monteiro
Data
28-07-2020

Escalas	Tipo		N.º SAP		N.º de Ordem no Projeto		Versão
1:10	222	-	10002000917	-	-	-	02