Montagens
a e **b**

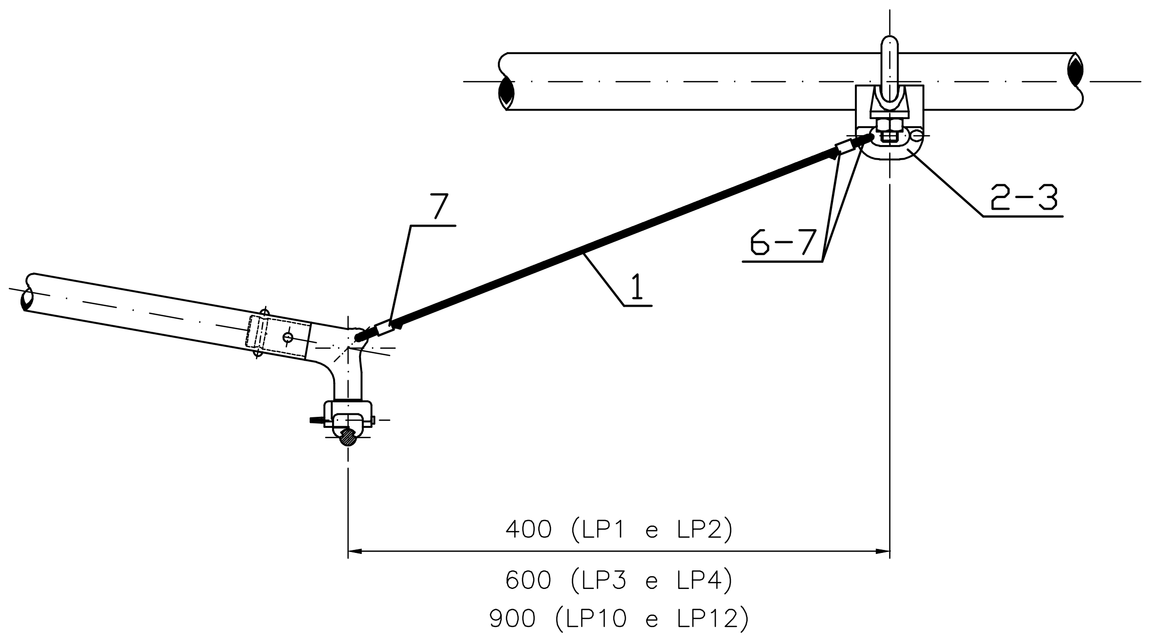

Montagens
c e **d**

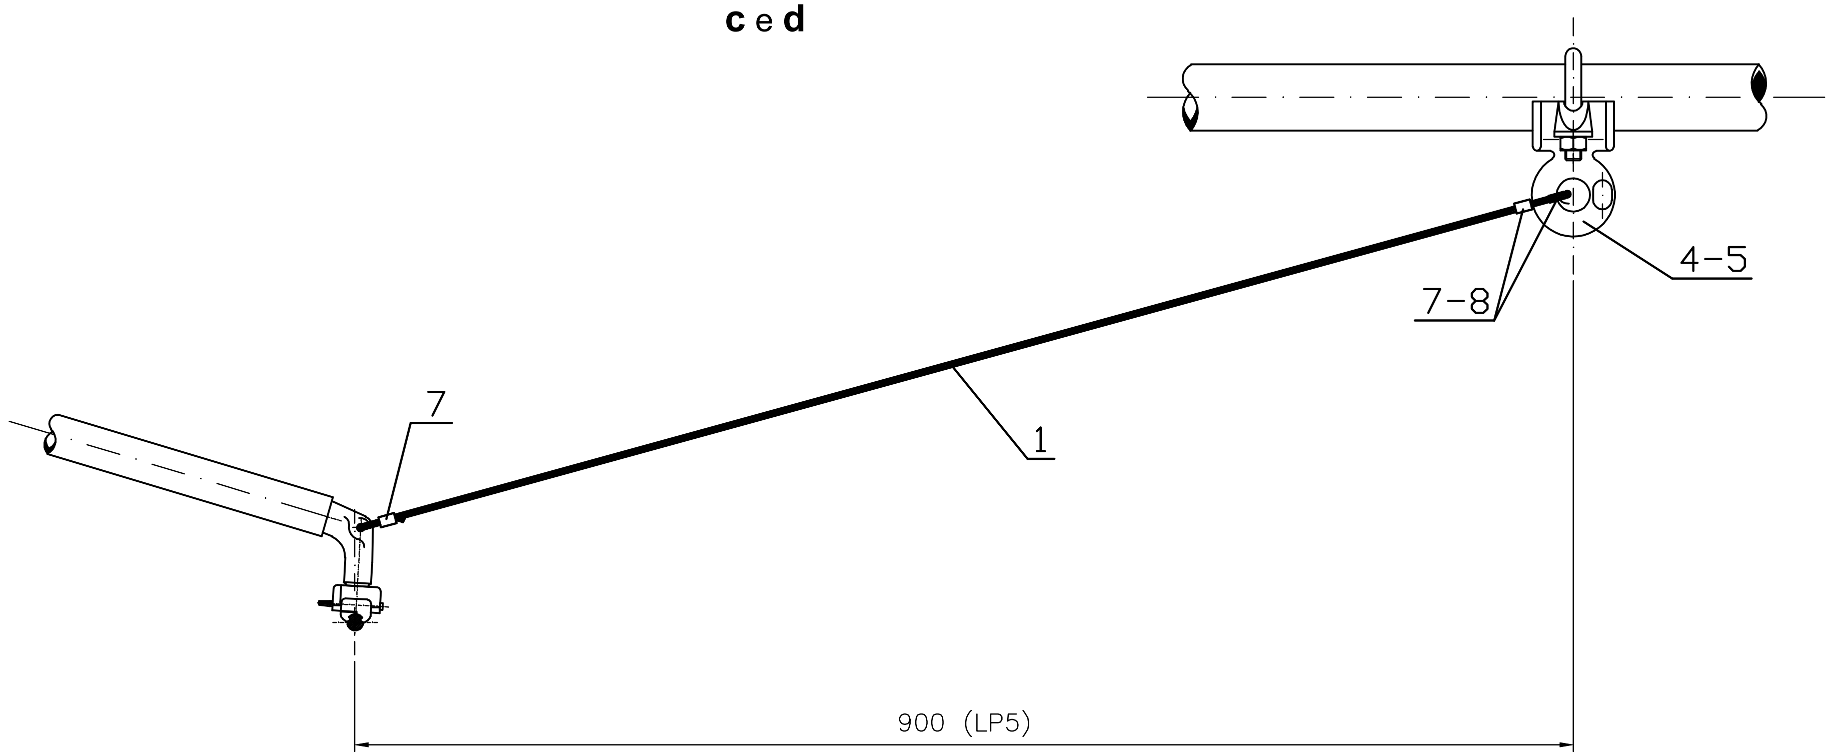

d	c	b	a	DESIGNAÇÃO		N. DO DESENHO	NOMENCLAT.	N.º REFª	CÓDIGO (MT.CA.003)	PESO Kg	OBSERVAÇÕES
1	1	–	–	Sapatilho de 10 (LP5)	05.701.02	44021	75167012	8	294D		Refª D
2	2	2	2	Manga de aperto de 10	05.102.01	44021	75161260	7	295A		Refª 1
–	–	1	1	Sapatilho de 10	05.701.01	44021	75167010	6	294A		Refª A
1	–	–	–	Aperta tubo com olhal 40x49	05.301.08	42011	75161119	5	523		
–	1	–	–	Aperta tubo com olhal 30x38	05.301.07	42010	75161111	4	522		
–	–	1	–	Aperta tubo com olhal 34x42	05.301.06	42014	75161115	3	525		
–	–	–	1	Aperta tubo com olhal 24x32	05.301.05	42015	75161107	2	524		
1	1	1	1	Condutor de cobre duro ø4	01.100.03		75184153	1	9Q		

QUANTIDADES

d	c	b	a
LP5		LP1 a LP4 LP10 e LP12	
Consola		Consola p/ plataformas altas e 2 vias	Consola normal

E-6187

Notas e historial de Alterações

Alterações	Designação	Assinatura	Data
C	Introdução das Ref. 6, 7 e 8 e adaptação às catenárias LP10 e LP12	Feliciano Fernandes	01/2011
B			02/1999
A			09/1997

Logótipos e informação complementar

Levantou

Desenhou

Projectou

Verificou
Ouro Chambel
André Frederico

REFER *EPE*

Direcção Geral de Exploração da Infraestrutura

Direcção de Engenharia da Infraestrutura

Especialidade Técnica
CATENÁRIA

Título do Desenho
ANTIVENTO PARA CONSOLA

ESTE DESENHO APENAS SE CONSIDERA VÁLIDO DESDE QUE ESTEJAM PREENCHIDOS OS CAMPOS DE APROVAÇÃO E INSERIDO O RESPECTIVO NUMERO SAP

O Responsável por
Catenária e Energia de Tracção
Pissarra dos Santos

Escalas
1:5

Tipo		N.º SAP		N.º de Ordem no Projecto		Versão
222	-	10002000921	-	-	-	01

O Director de Engenharia
José Carlos Clemente
Data
13-01-2011

297 x 631