(*)- Fixação do Aparelho Tensor

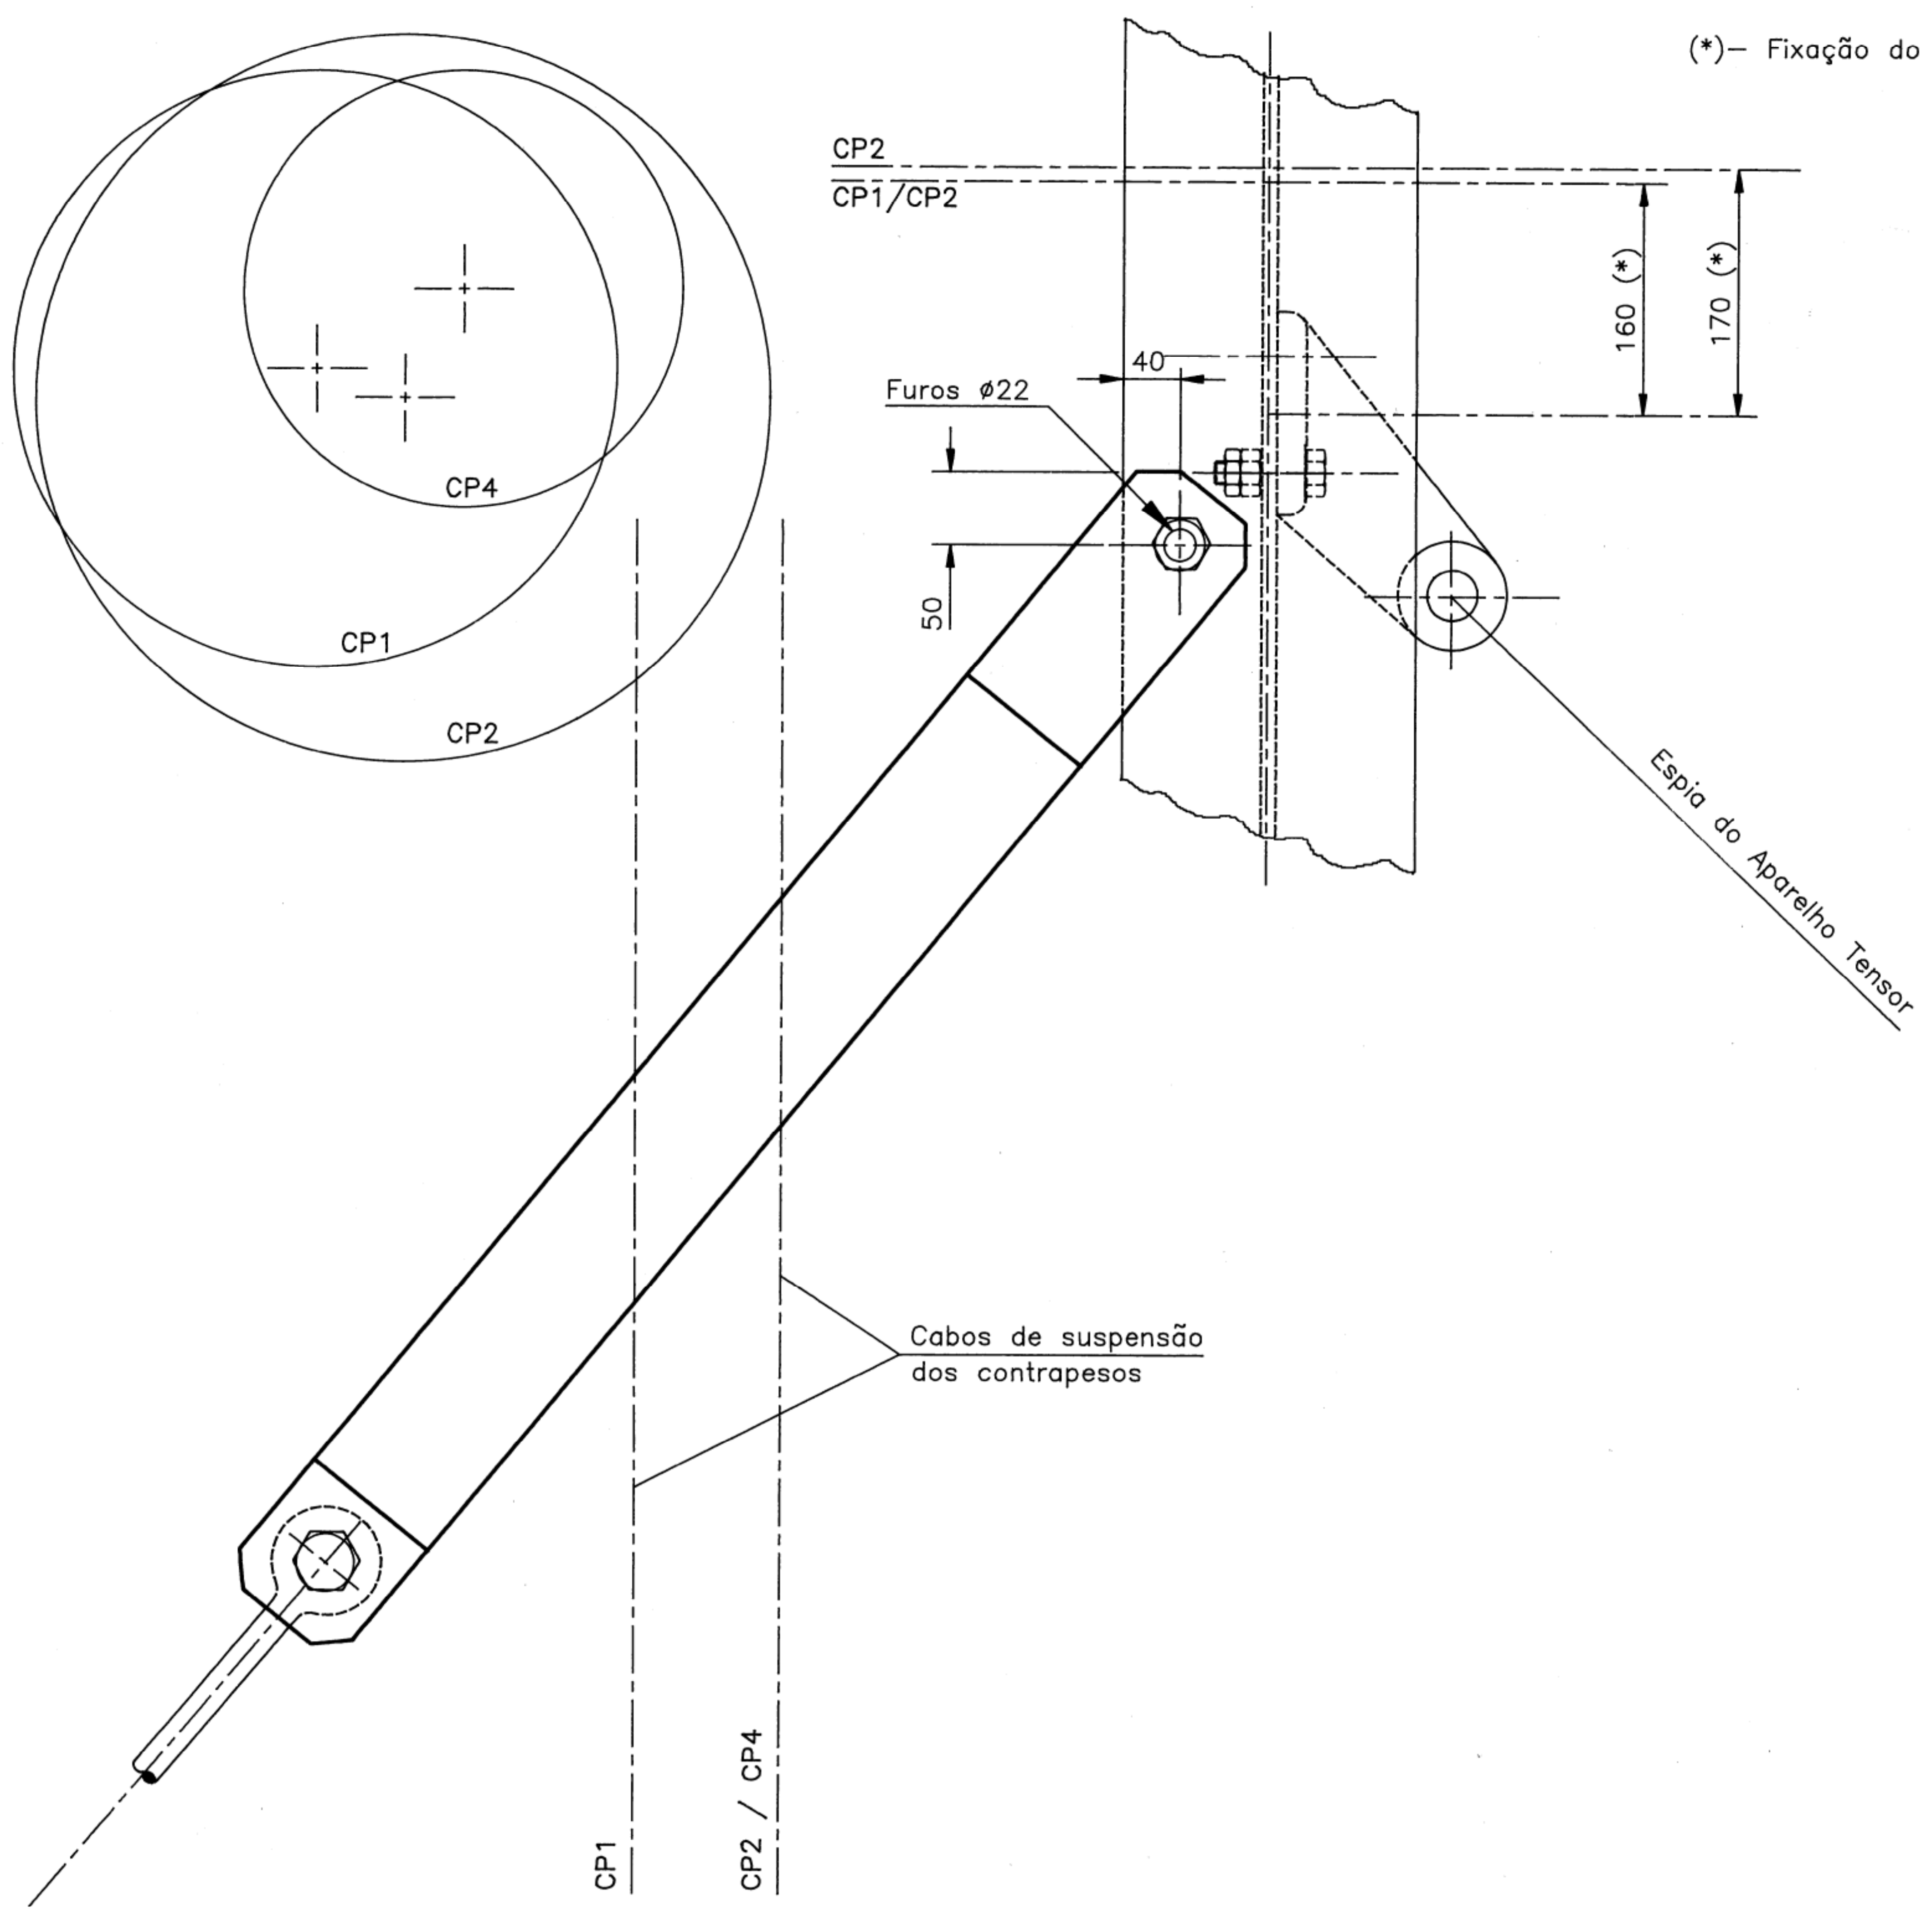

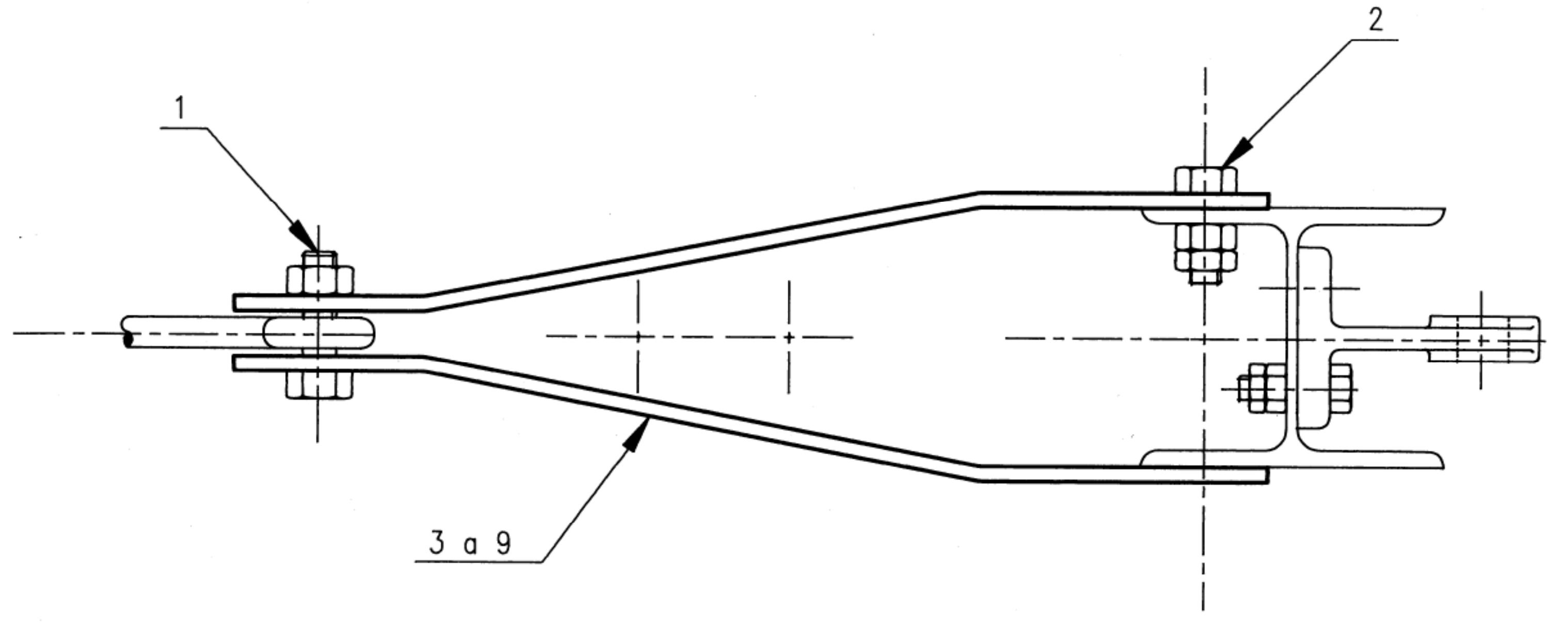

3 A 9

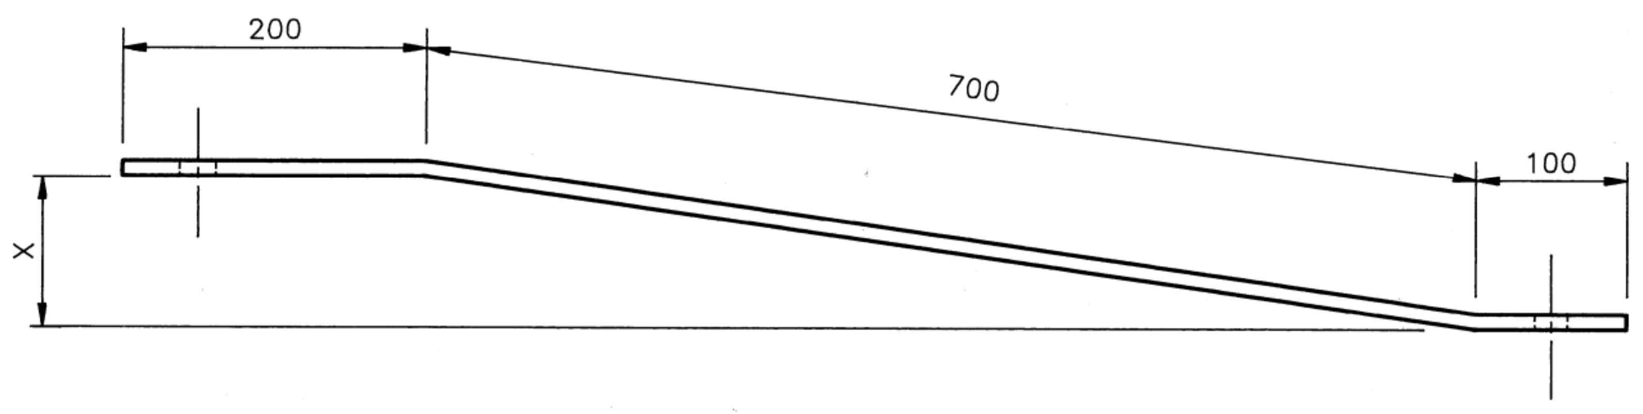

Refa	X
3	75
4	95
5	115
6	135
7	155
8	185
9	210

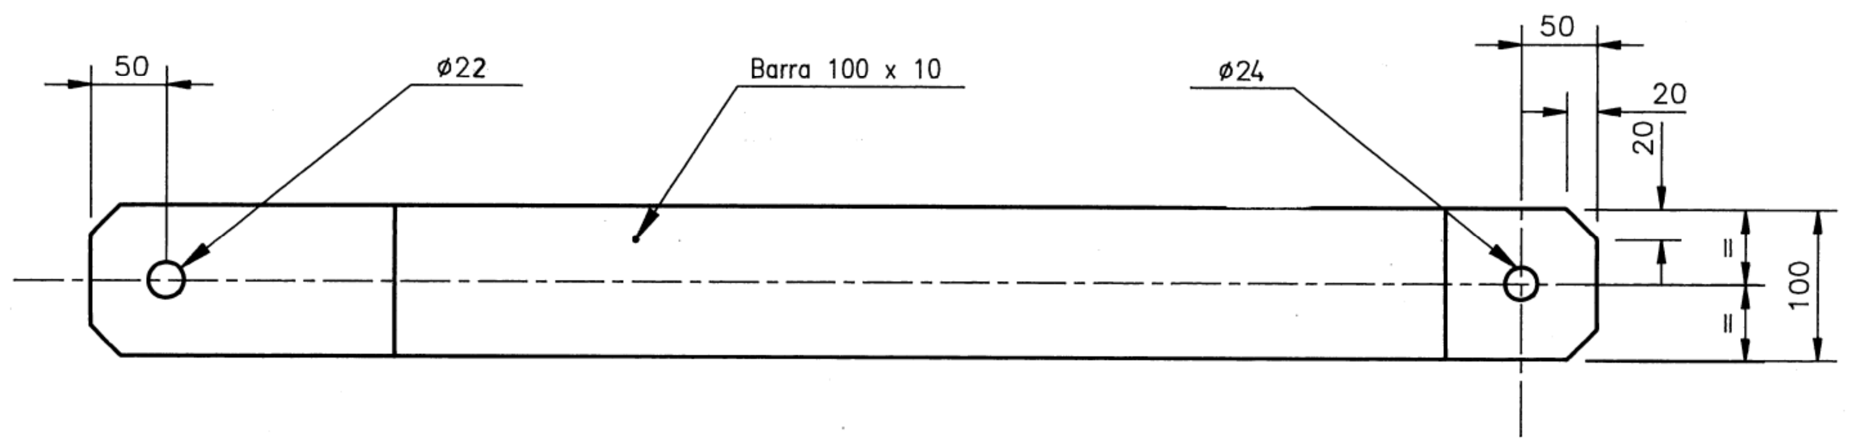

BRINCO DE AMARRAÇÃO

Normas:
Aço: S235JR NP EN 10025+A1
Galvanização: NF EN ISO 1461

g	f	e	d	c	b	a	Designação	Nº Desenho	Nomenclat.	Refa	Material	IT-C-46	Observações
2	–	–	–	–	–	–	Brinco de Amarração (X=210)		75113017	9		102g	**02.304.15**
–	2	–	–	–	–	–	Brinco de Amarração (X=185)		75113016	8		102f	**02.304.14**
–	–	2	–	–	–	–	Brinco de Amarração (X=155)		75113015	7		102e	**02.304.13**
–	–	–	2	–	–	–	Brinco de Amarração (X=135)		75113014	6		102d	**02.304.12**
–	–	–	–	2	–	–	Brinco de Amarração (X=115)		75113013	5		102c	**02.304.11**
–	–	–	–	–	2	–	Brinco de Amarração (X=95)		75113012	4		102b	**02.304.10**
–	–	–	–	–	–	2	Brinco de Amarração (X=75)		75113011	3		102a	**02.304.09**
–	2	2	2	2	2	2	Parafuso M20x60/46 c/porca Hu		33144437	2		16F3	**04.101.28**
1	1	1	1	1	1	1	Parafuso M22x75/46 c/porca Hu		33144462	1		16G	**04.100.16**
50	40	34 a 36	30 a 32	26 a 28	22 a 24	18 a 20							

POSTES

MONTAGEM

Projectou		
Desenhou	Nov. 95	A. Correia
Verificou		
Visto		

Escalas: 1:5

B Amarracão-Alt.da furação

Desenhos a consultar:

CATENÁRIA

POSTES ESPIADOS DOS DOIS LADOS

ESPIA DO LADO DO APARELHO TENSOR

O Chefe do Serviço

O Chefe de Divisão

Caminhos de Ferro Portugueses
DIRECÇÃO DE CONSERVAÇÃO

DIVISÃO DE CATENÁRIA E ENERGIA-SERVIÇO DE CATENÁRIA

Des. N. **E-6215**

SÉRIE

A	B	C
10/95	10/99	[illegible]

Substitui o Des. n.

Substituido pelo Des. n.