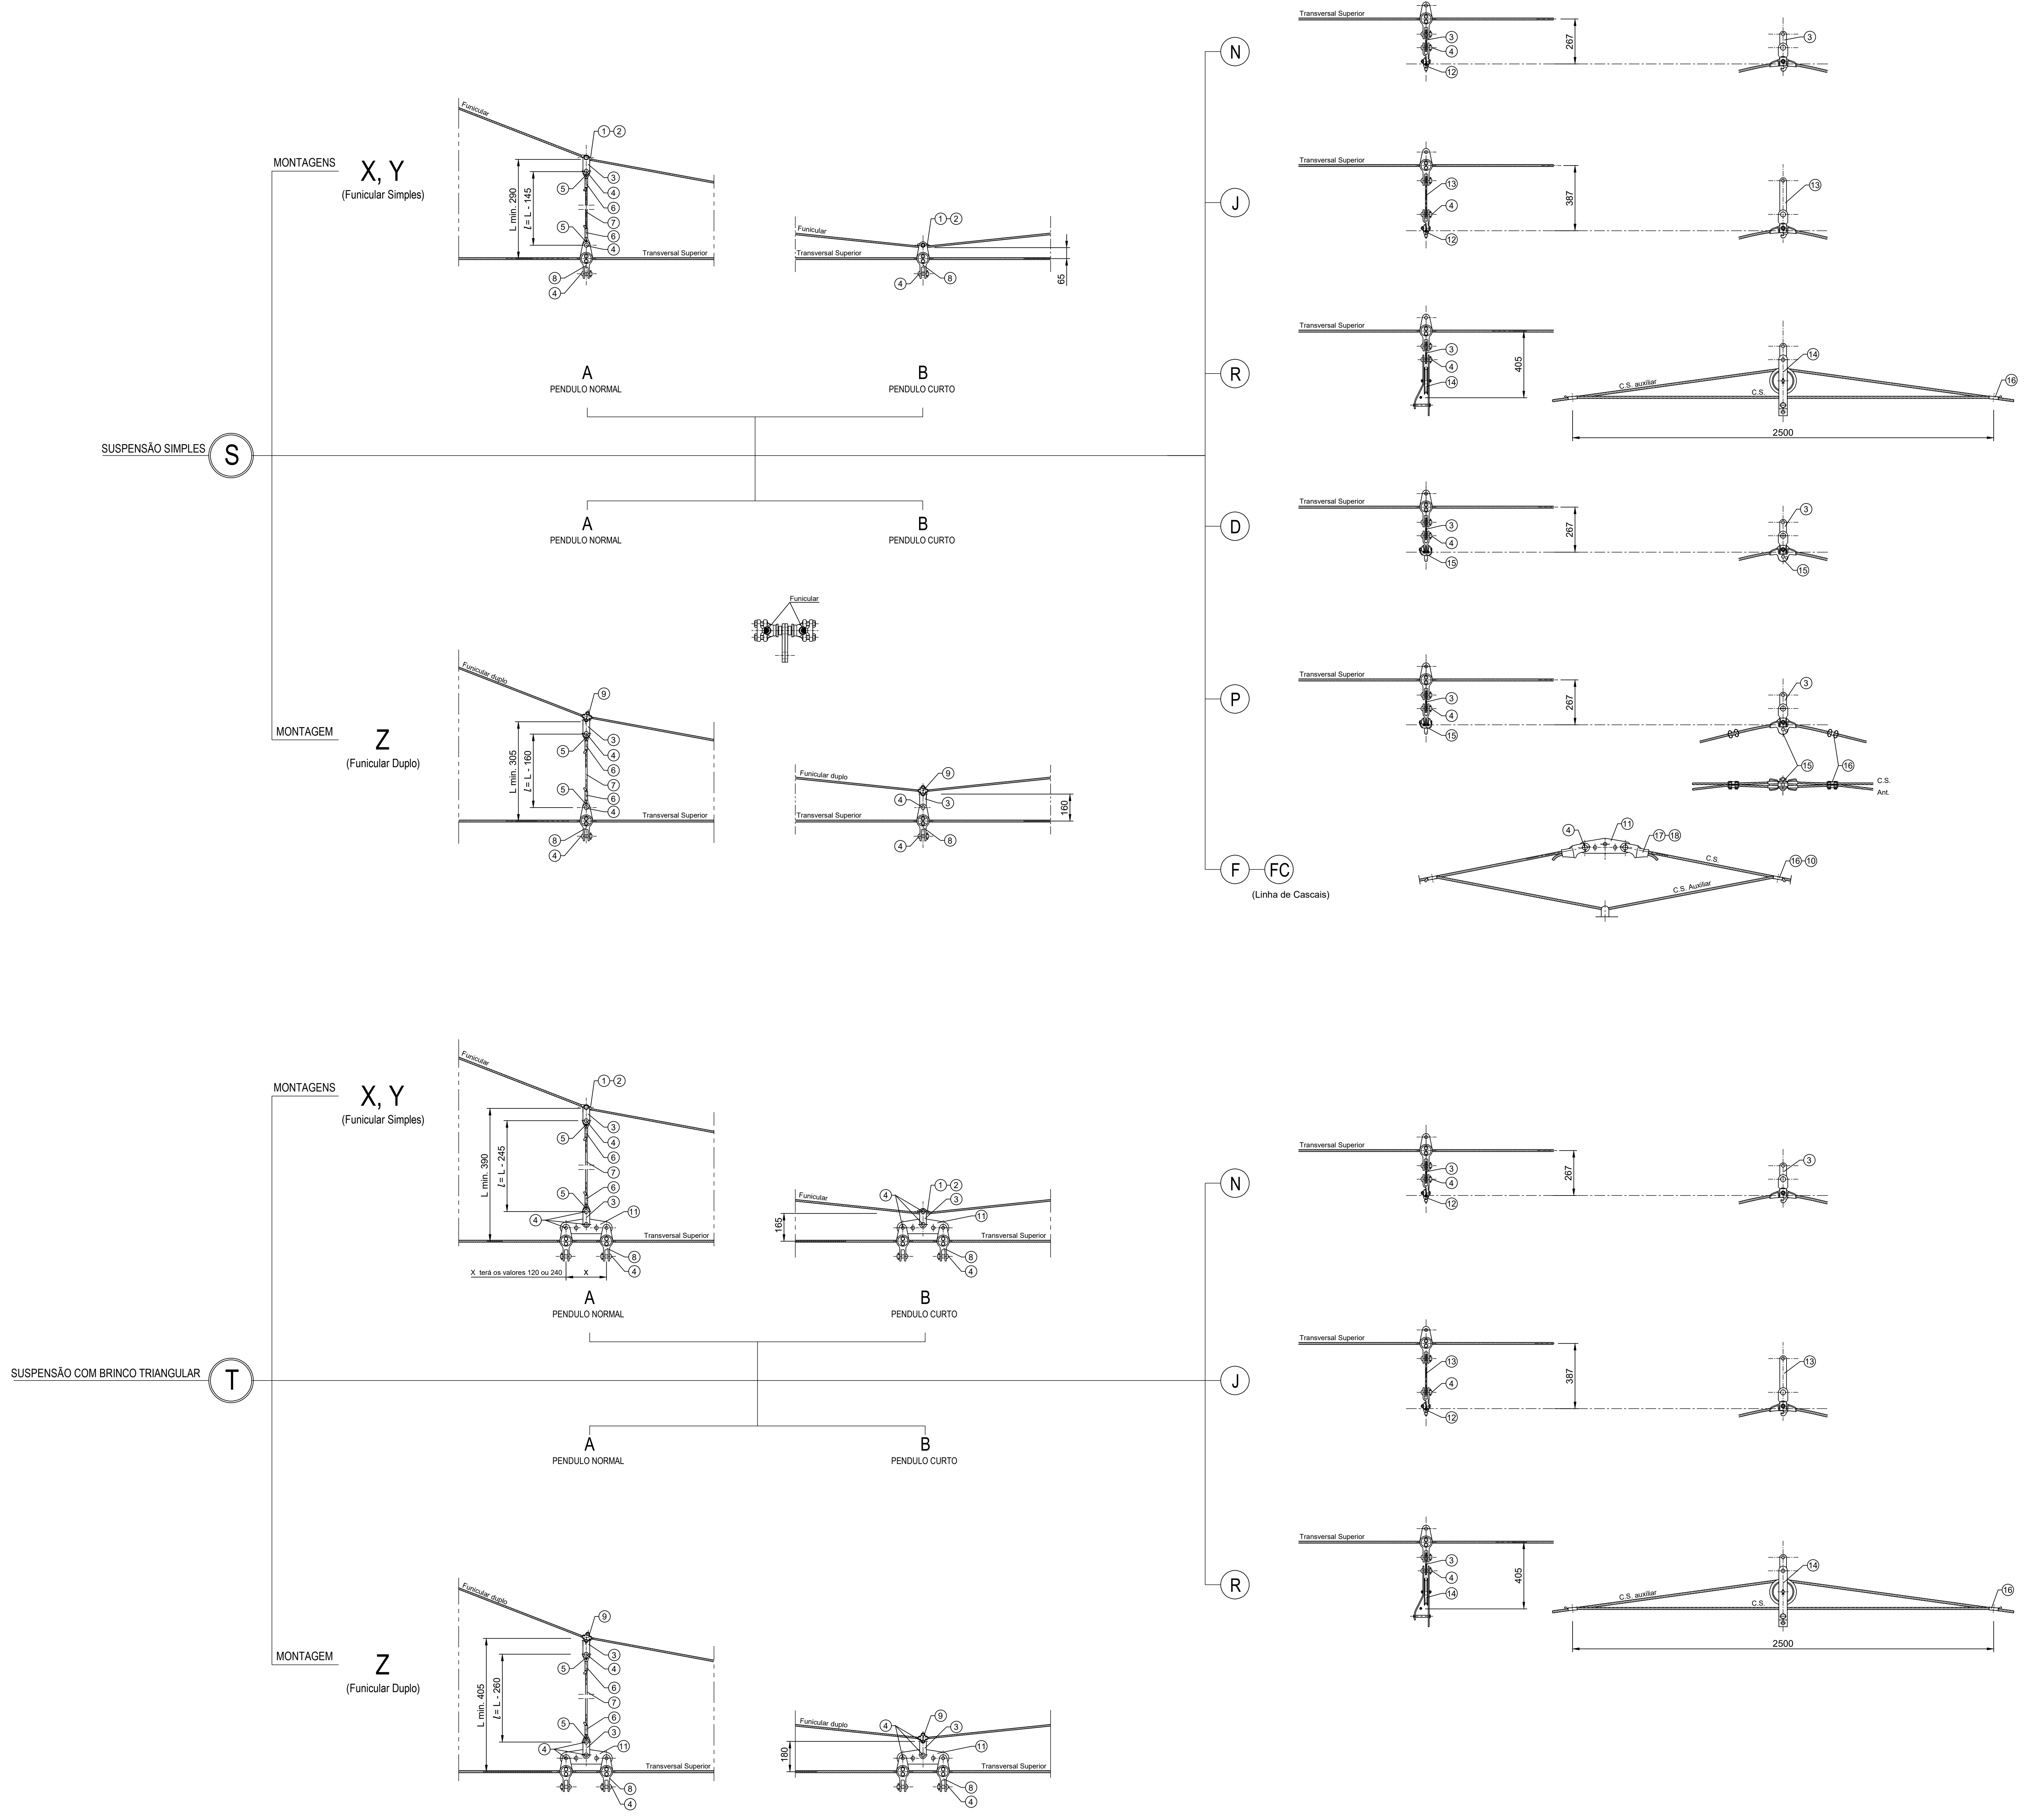

NOTA SOBRE AS REFERÊNCIAS DAS MONTAGENS

MONTAGEM

S

- X Funicular Bz 65
- Y Funicular Bz 95 e 120
- Z Funicular duplo
  - A Pêndulo normal
  - B Pêndulo curto
    - N Suspensão normal
    - J Suspensão com brinco
    - R Suspensão com roldana
    - D Suspensão com pinça dupla
    - P Antideslizamento (c/ cabo antid.)
    - F Antideslizamento de pórtico
    - FC Antideslizamento de pórtico (Linha de Cascais)

MONTAGEM

T

- X Funicular Bz 65
- Y Funicular Bz 95 e 120
- Z Funicular duplo
  - A Pêndulo normal
  - B Pêndulo curto
    - NJ Suspensão normal + Suspensão com brinco
    - NR Suspensão normal + Suspensão com roldana
    - JR Suspensão com brinco + Suspensão com roldana
    - RR Suspensão com roldana + Suspensão com roldana
    - NN Suspensão normal + Suspensão normal
    - JJ Suspensão com brinco + Suspensão com brinco

JJ	NN	RR	JR	NR	NJ	FC	F	P	D	R	J	N	TZB	TZA	TYB	TYA	TXB	TXA	SZB	SZA	SYB	SYA	SXB	SXA	DESIGNAÇÃO		DESENHO	NOMENCLAT.	REF.ª	CÓDIGO (GR.MN.CAT.003)	OBSERVAÇÕES
-	-	-	-	-	-	2	-	-	-	-	-	-	-	-	-	-	-	-	-	-	-	-	-	-	Peça de amarração para cabo 95	Cód. 541A Cód. 541B	45001	75111060 75113118	18	05.400.14 05.400.15	Ref 3 Ref 4
-	-	-	-	-	-	-	2	-	-	-	-	-	-	-	-	-	-	-	-	-	-	-	-	-	Peça de amarração para cabo Bz 65	Cód. 540A Cód. 540C		75111055 75113110	17	05.400.11 05.400.13	Ref 1 Ref 2
-	-	-	-	-	-	-	2	2	-	-	-	-	-	-	-	-	-	-	-	-	-	-	-	-	Aperta cabos de extremidade	Cód. 363	45007	75161011	16	05.101.03	Ref. 5 a 8
-	-	-	-	-	-	-	-	1	1	-	-	-	-	-	-	-	-	-	-	-	-	-	-	-	Pinça dupla de suspensão do cabo de suporte	Cód. 503	43010	75112076	15	05.200.06	Ref. 1 a 4
-	-	2	1	1	-	-	-	-	-	1	-	-	-	-	-	-	-	-	-	-	-	-	-	-	Roldana para pórtico flexível	Cód. 401	43011	75172011	14	05.101.09	
2	-	-	1	-	1	-	-	-	-	-	1	-	-	-	-	-	-	-	-	-	-	-	-	-	Brinco comprido (L=250)	Cód. 83A	45005/3	75113052	13	02.303.02	Ref. 6
2	2	-	1	1	2	-	-	-	-	-	1	1	-	-	-	-	-	-	-	-	-	-	-	-	Pinça de suspensão do cabo de suporte em pórtico	Cód. 502	43006	75112075	12	05.200.05	Ref. 1 a 3
-	-	-	-	-	-	1	1	-	-	-	-	-	1	1	1	1	1	1	-	-	-	-	-	-	Brinco triangular (Tipo A)	Cód. 82	45005/4	75113004	11	02.305.05	Ref. 4
-	-	-	-	-	-	4	-	-	-	-	-	-	-	-	-	-	-	-	-	-	-	-	-	-	Garra de união para cabos 65mm2/FC e 65/65	Cód. 361	44007		10	**05.100.03+04.201.08+04.300.08**	
-	-	-	-	-	-	-	-	-	-	-	-	-	-	1	-	1	-	1	-	-	-	-	-	-	Pinça de suspensão do funicular duplo	Cód. 508	E-6158	75168057	9	05.200.11	
-	-	-	-	-	-	-	-	-	-	-	-	-	2	2	2	2	2	2	1	1	1	1	1	1	Peça de suspensão das transversais	Cód. 527	43005	75164057	8	05.101.08	Ref. 5 a 9
-	-	-	-	-	-	-	-	-	-	-	-	-	-	1	-	1	-	1	-	1	-	1	-	1	Cabo Bz 25	Cód. 9D		75184415	7	01.100.04	
-	-	-	-	-	-	-	-	-	-	-	-	-	-	2	-	2	-	2	-	2	-	2	-	2	Manga de aperto 25	Cód. 295B	44021	75161265	6	05.102.02	Ref. 2
-	-	-	-	-	-	-	-	-	-	-	-	-	-	2	-	2	-	2	-	2	-	2	-	2	Sapatiho 25	Cód. 294B		75167015	5	05.701.03	Ref. B
2	2	2	2	2	2	2	2	-	-	-	1	1	5	7	5	7	5	7	2	3	1	3	1	3	Cavilha 19x52 + chaveta V5	Cód. 406B Cód. 291A	45008		4	**05.600.03 05.601.03**	Mont. a/4
-	2	2	1	1	1	-	-	1	1	1	-	1	2	4	2	4	2	4	2	2	-	2	-	2	Brinco curto	Cód. 81	45005/1	75113055	3	02.303.01	Ref. 1
-	-	-	-	-	-	-	-	1	1	1	-	-	-	-	1	1	-	-	-	-	1	1	-	-	Pinça de suspensão do funicular (Bz 95 ou Bz 120)	Cód.506B	43005	75164013	2	05.200.10	Ref. 3 e 4
-	-	-	-	-	-	-	-	-	-	-	-	-	-	-	-	-	1	1	-	-	-	-	1	1	Pinça de suspensão do funicular (Bz 65)	Cód.506A		75164007	1	05.200.09	Ref. 1 e 2

QUANTIDADES

Suspensão com brinco triangular (JJ, NN, RR, JR, NR, NJ)

Suspensão com brinco simples (FC, F, P, D, R, J, N)

Notas e historial de alterações

Alterações	Designação	Assinatura	Data
C	Correção na tabela de peças, mudança da Ref. 19 para a Ref. 10 e introdução de códigos	Feliciano Fernandes	05-2020
B	Introdução da montagem FC, códigos e nomenclaturas	Feliciano Fernandes	04-2008

MONTAGEM

Logótipos e informação complementar
Projetista
Data
20-05-2020
N.º Projetista
E-7092

Levantou
Desenhou Feliciano Fernandes
Projetou
Verificou Marco Santos

Infraestruturas de Portugal
Direção de Engenharia e Ambiente
Unidade de Catenária e Energia de Tração

Especialidade Técnica
CATENÁRIA E ENERGIA DE TRAÇÃO

Título do Desenho

SUSPENSÃO DO CABO DE SUPORTE EM PÓRTICOS TIPO C

ESTE DESENHO APENAS SE CONSIDERA VÁLIDO DESDE QUE ESTEJAM PREENCHIDOS OS CAMPOS DE APROVAÇÃO E INSERIDO O RESPETIVO NUMERO SAP

O Responsável por
Catenária e Energia de Tração
Marco Santos

O Responsável por
Estudos e Projetos Ferroviários
Fernando Vendas

Escalas	Tipo	N.º SAP	N.º de Ordem no Projeto	Versão
1:20	222	10002000932	-	02

O Diretor de Engenharia e Ambiente
José Santinho Faísca
Data
20-05-2020