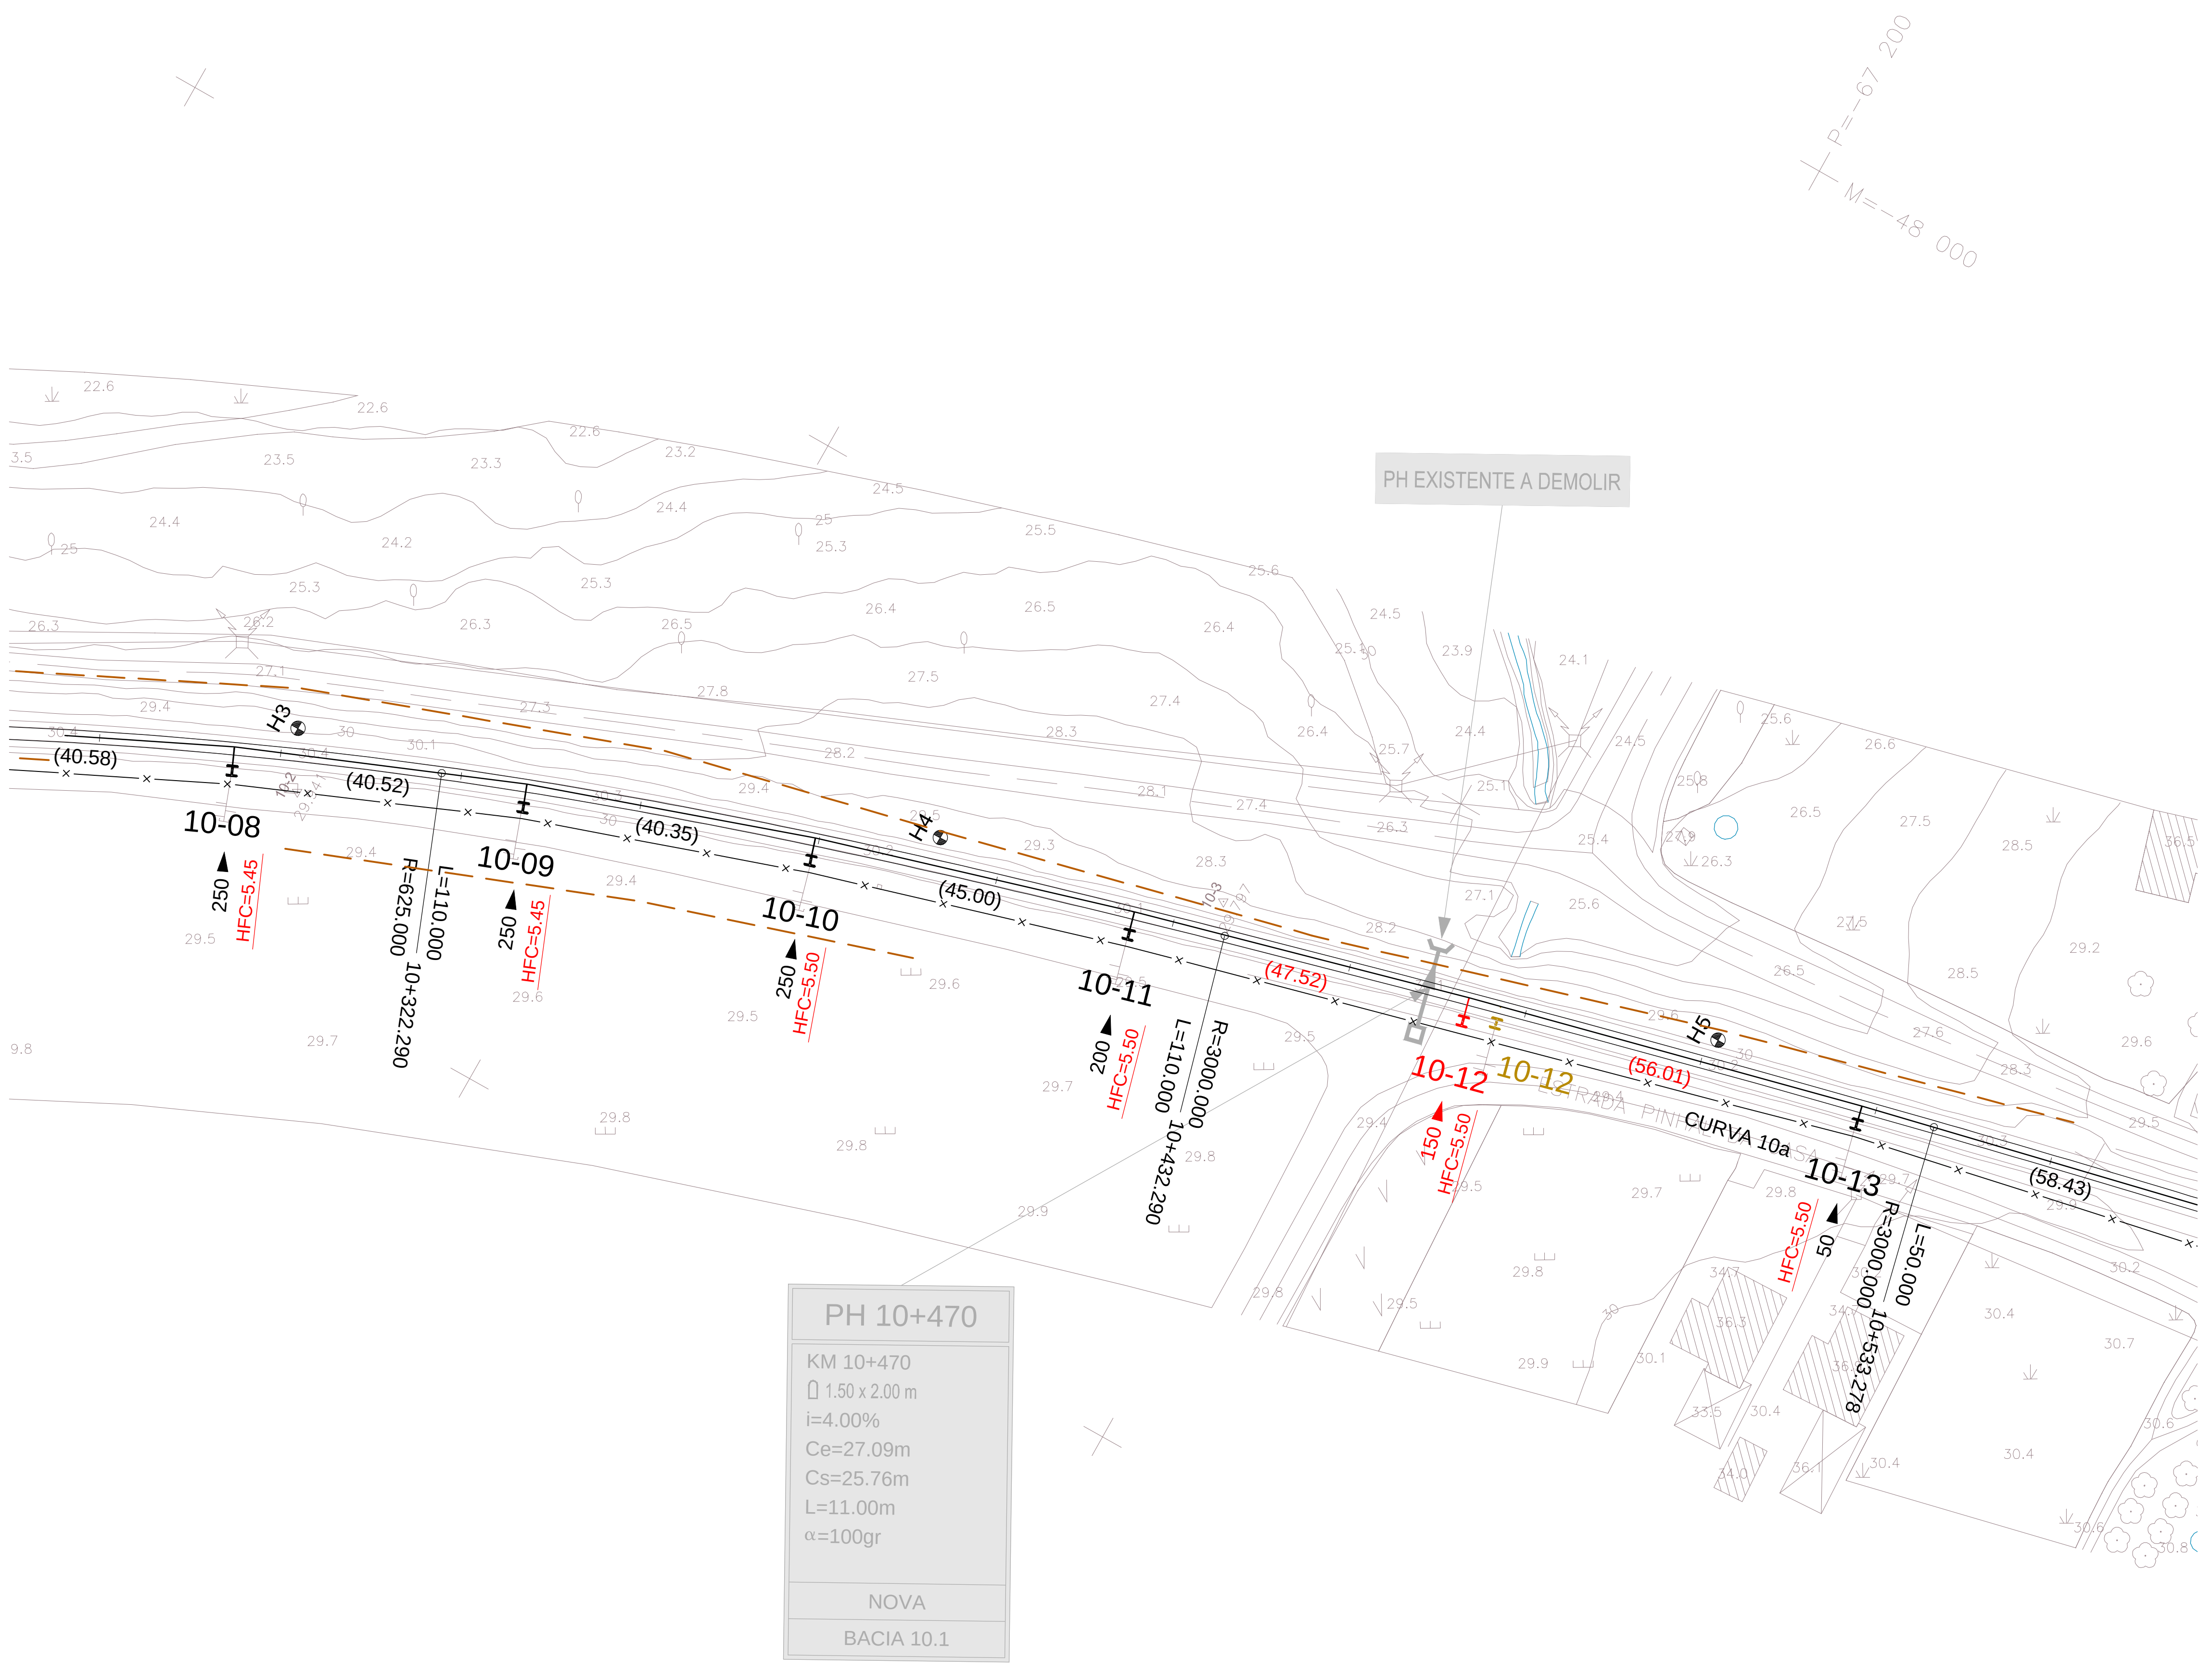

LEGENDA

━━	Existente
🟥 ━━	a instalar / regular
- - -	a remover / desmontar
XX-XX *XX-XX	Poste existente renumerado
XX-XX	Poste projeto

10/I

T8/I

Notas e historial de Alterações

02 - Set. 2020 - Revisão de acordo com comentários do parecer (Versão 01)

01 - Jan. 2020 - Revisão de acordo com comentários do parecer DMS 007- 2581030 de 2019-12-05

Logótipos e informação complementar

Projetista

PROFICO

FULCRUM

Geoárea

Data
Julho 2019

N.º Projetista
42517.PE.09.IFT.00.102

Levantou

Desenhou Joana Girbal

Projetou Paulo Lopes

Verificou Carlos Lopes

Infraestruturas de Portugal

Direção de Empreendimentos Ferroviários

Linha
Linha de Vendas Novas

Local
Setil - Vendas Novas

Fase do Projeto
Projeto de Execução

Especialidade Técnica
Volume 09 - Instalações Fixas de Tração Elétrica

Nome do Empreendimento
Modernização da Linha de Vendas Novas

Título do Desenho
km 10
Planta de Piquetagem
Pk 10.300 a Pk 10.500

ESTE DESENHO APENAS SE CONSIDERA VÁLIDO DESDE QUE ESTEJAM PREENCHIDOS OS CAMPOS DE APROVAÇÃO E INSERIDO O RESPETIVO NUMERO SAP

O Responsável por

O Diretor de Engenharia

Data

Escalas	Tipo		N.º SAP		N.º de Ordem no Projeto		Versão
1/1000	317	-	10003833482	-	102	-	02

RE.FR.AGR.002 | V00

297 x 631