



LEGENDA

- Existente
- a instalar / regular
- a remover / desmontar
- XX-XX / YY-YY — Poste existente renumerado
- XX-XX — Poste projeto

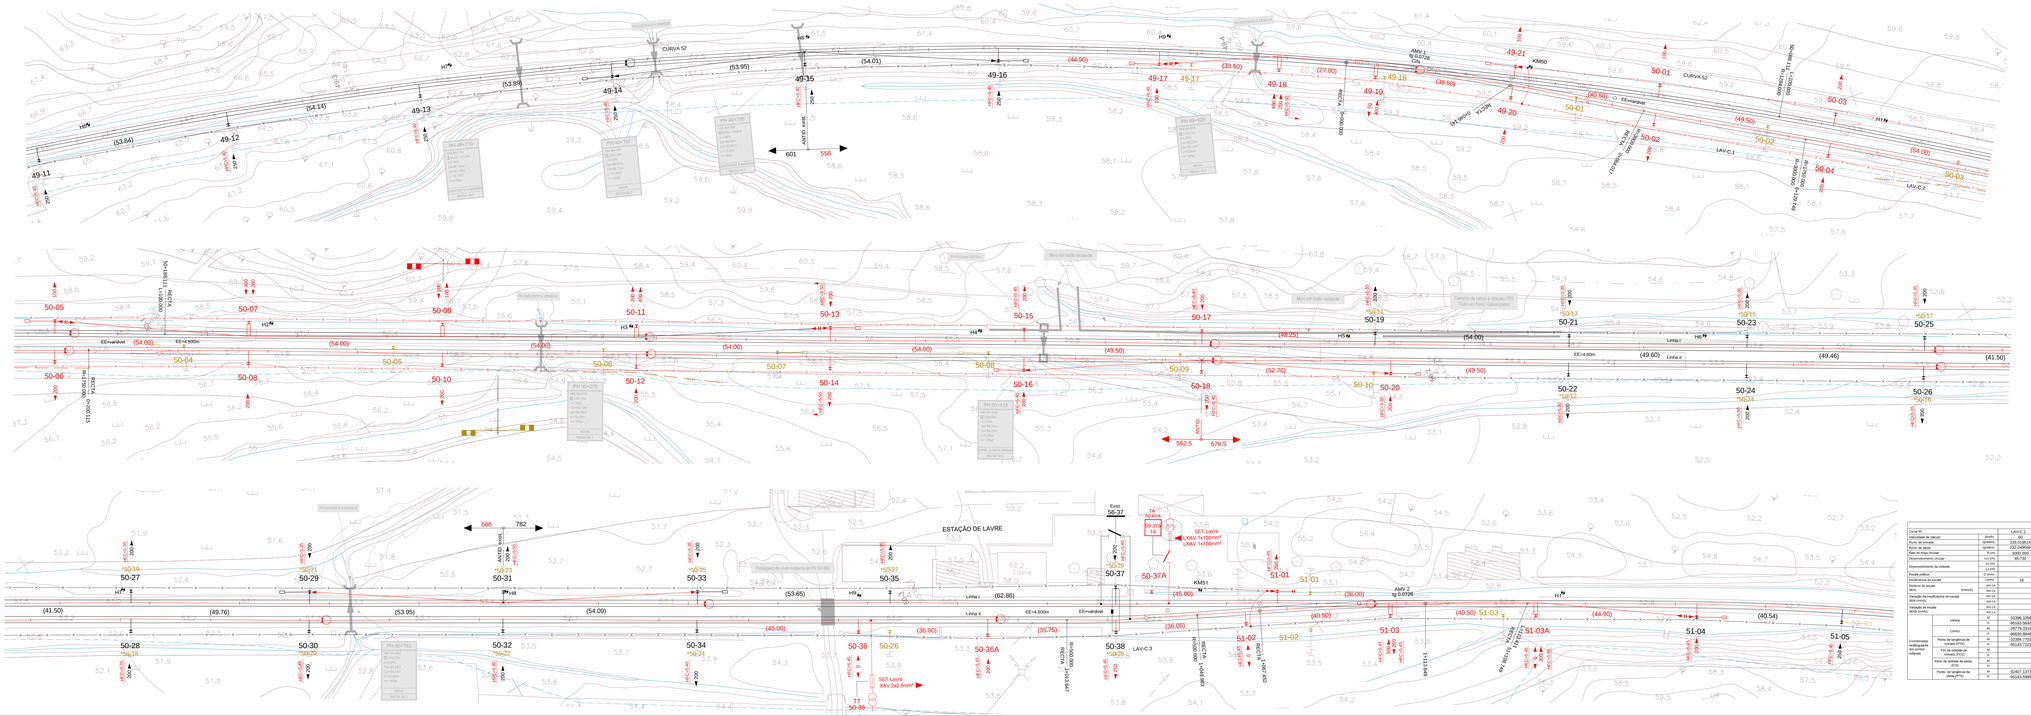


## Elementos dos lanços

| VIA | Nº LANÇO | POSTES EXTREMOS | | | | | COMPRIMENTOS | | | | | | OBSERVAÇÕES |
|---|---|---|---|---|---|---|---|---|---|---|---|---|---|
| | | Nº POSTE | F.C. | C.S. | Nº POSTE | F.C. | LANÇO | C.S. | F.C. | Cabo AAC 1x150mm² | Cabo AAC 1x95mm² | C.S.T. | |
| I | 49/3 | 49-04 | AT | AT | 50-13 | AT | AT | 1155,0 | 1155,0 | 1114,0 | | 41,0 | | Lanço existente com comprimento revisto |
| II | 49/3 | 49-17 | AT | AT | 51-04 | AT | AT | 1242,0 | 1242,0 | 1197,0 | | 70,0 | | Lanço de catenária nova |
| I | 50/3 | 50-05 | AT | AT | 51-04 | AT | AT | 1448,0 | 1448,0 | 1373,0 | | 75,0 | | Lanço de catenária nova |
| II | 51/3 | 51-11 | AT | AT | 51-21 | AT | AT | Exist. | Exist. | Exist. | Exist. | | | Existente |
| I | 75/3 | 49-21 | | | 51-01 | | | | | | | | 1516,0 | Lanço existente com comprimento revisto |

| Curva Nº | | LAV-C.1 | Curva1 | LAV-C.2 | LAV-C.3 |
|---|---|---|---|---|---|
| Velocidade de cálculo | (km/h) | 80 | | 80 | 80 |
| Ponto de entrada | (grados) | 210,018514 | | 232,040046 | 234,609021 |
| Ponto de saída | (grados) | 232,040046 | | 234,609021 | 237,967190 |
| Raio de curvatura | (m) | 3000,000 | | 1750,000 | 500,000 |
| Sobreelevação circular | (cm) | 45,00 | | 72,900 | 36,935 |
| Sobreelevação de cálculo | (cm) | | | | |
| Escala política | (cm) | | | | |
| Insuficiência de escala | (cm/s) | 15 | | 28 | 99 |
| Défice de escala | (cm/s) | | | | |
| (cumulo) | (m) | | | | |
| Variação da insuficiência de escala | (m/s) | | | | |
| (cumulo) | (m/s) | | | | |
| Variação de escala | (m/s) | | | | |
| (cumulo) | (m/s) | | | | |
| Coordenadas dos vértices | Vértice | M | -32366,1058 | -32424,1127 | -32872,5139 |
| | | P | -45143,5830 | -45224,4298 | -45656,3206 |
| | Centro | M | -29775,5015 | -33940,0240 | -32435,1951 |
| | | P | -46420,8648 | -44239,3467 | -46199,4589 |
| | Ponto de tangência de entrada (PCE) | M | -32584,7703 | -32407,1373 | -32863,1124 |
| | | P | -45473,7371 | -45183,5988 | -45960,7842 |
| | Ponto de tangência de saída (PTS) | M | | | |
| | | P | | | |
| | Inicio do cilindro de saída | M | | | |
| | | P | | | |
| | Ponto de tangência de saída (PTS) | M | -32457,1373 | -32442,2134 | -32880,7512 |
| | | P | -45183,5988 | -45244,5305 | -45972,5369 |

Notas e Historial de Alterações

| | | |
|---|---|---|
| 02 | - | Set. 2020 - Revisão de acordo com comentários do parecer (Versão 01) |
| 01 | - | Jan. 2020 - Revisão de acordo com comentários do parecer DMS 007- 2581030 de 2019-12-05 |

Cópias e informação complementar

Projetista: PROTICO, Qe2Área

Data: Julho 2019

Nº Projetista: 42517.PE.09.IFT.00.106

Infraestruturas de Portugal — Direção de Empreendimentos Ferroviários

Linha: Linha de Vendas Novas

Local: Setil - Vendas Novas

Fase do Projeto: Projeto de Execução

Especialidade Técnica: Volume 09 - Instalações Fixas de Tração Elétrica

Nome do Empreendimento: Modernização da Linha de Vendas Novas

Título do Desenho: Lavre — Planta de Piquetagem PK 49.600 a PK 51.200

Escalas: 1/500

Tipo: 317 - 10003833486 - 106 - 02

Nº Ordem do Projeto / Versão

Elaborou: Joana Grilo

Desenhou:

Projetou: Paulo Lopes

Verificou: Carlos Lopes

AVISO SOLICITAMENTE VERIFICAR AS COTAS ANTES DE QUALQUER TRABALHO. EM CASO DE DÚVIDA CONTACTAR O AUTOR DO PROJETO

O Responsável por

O Diretor de Empreitada

Data