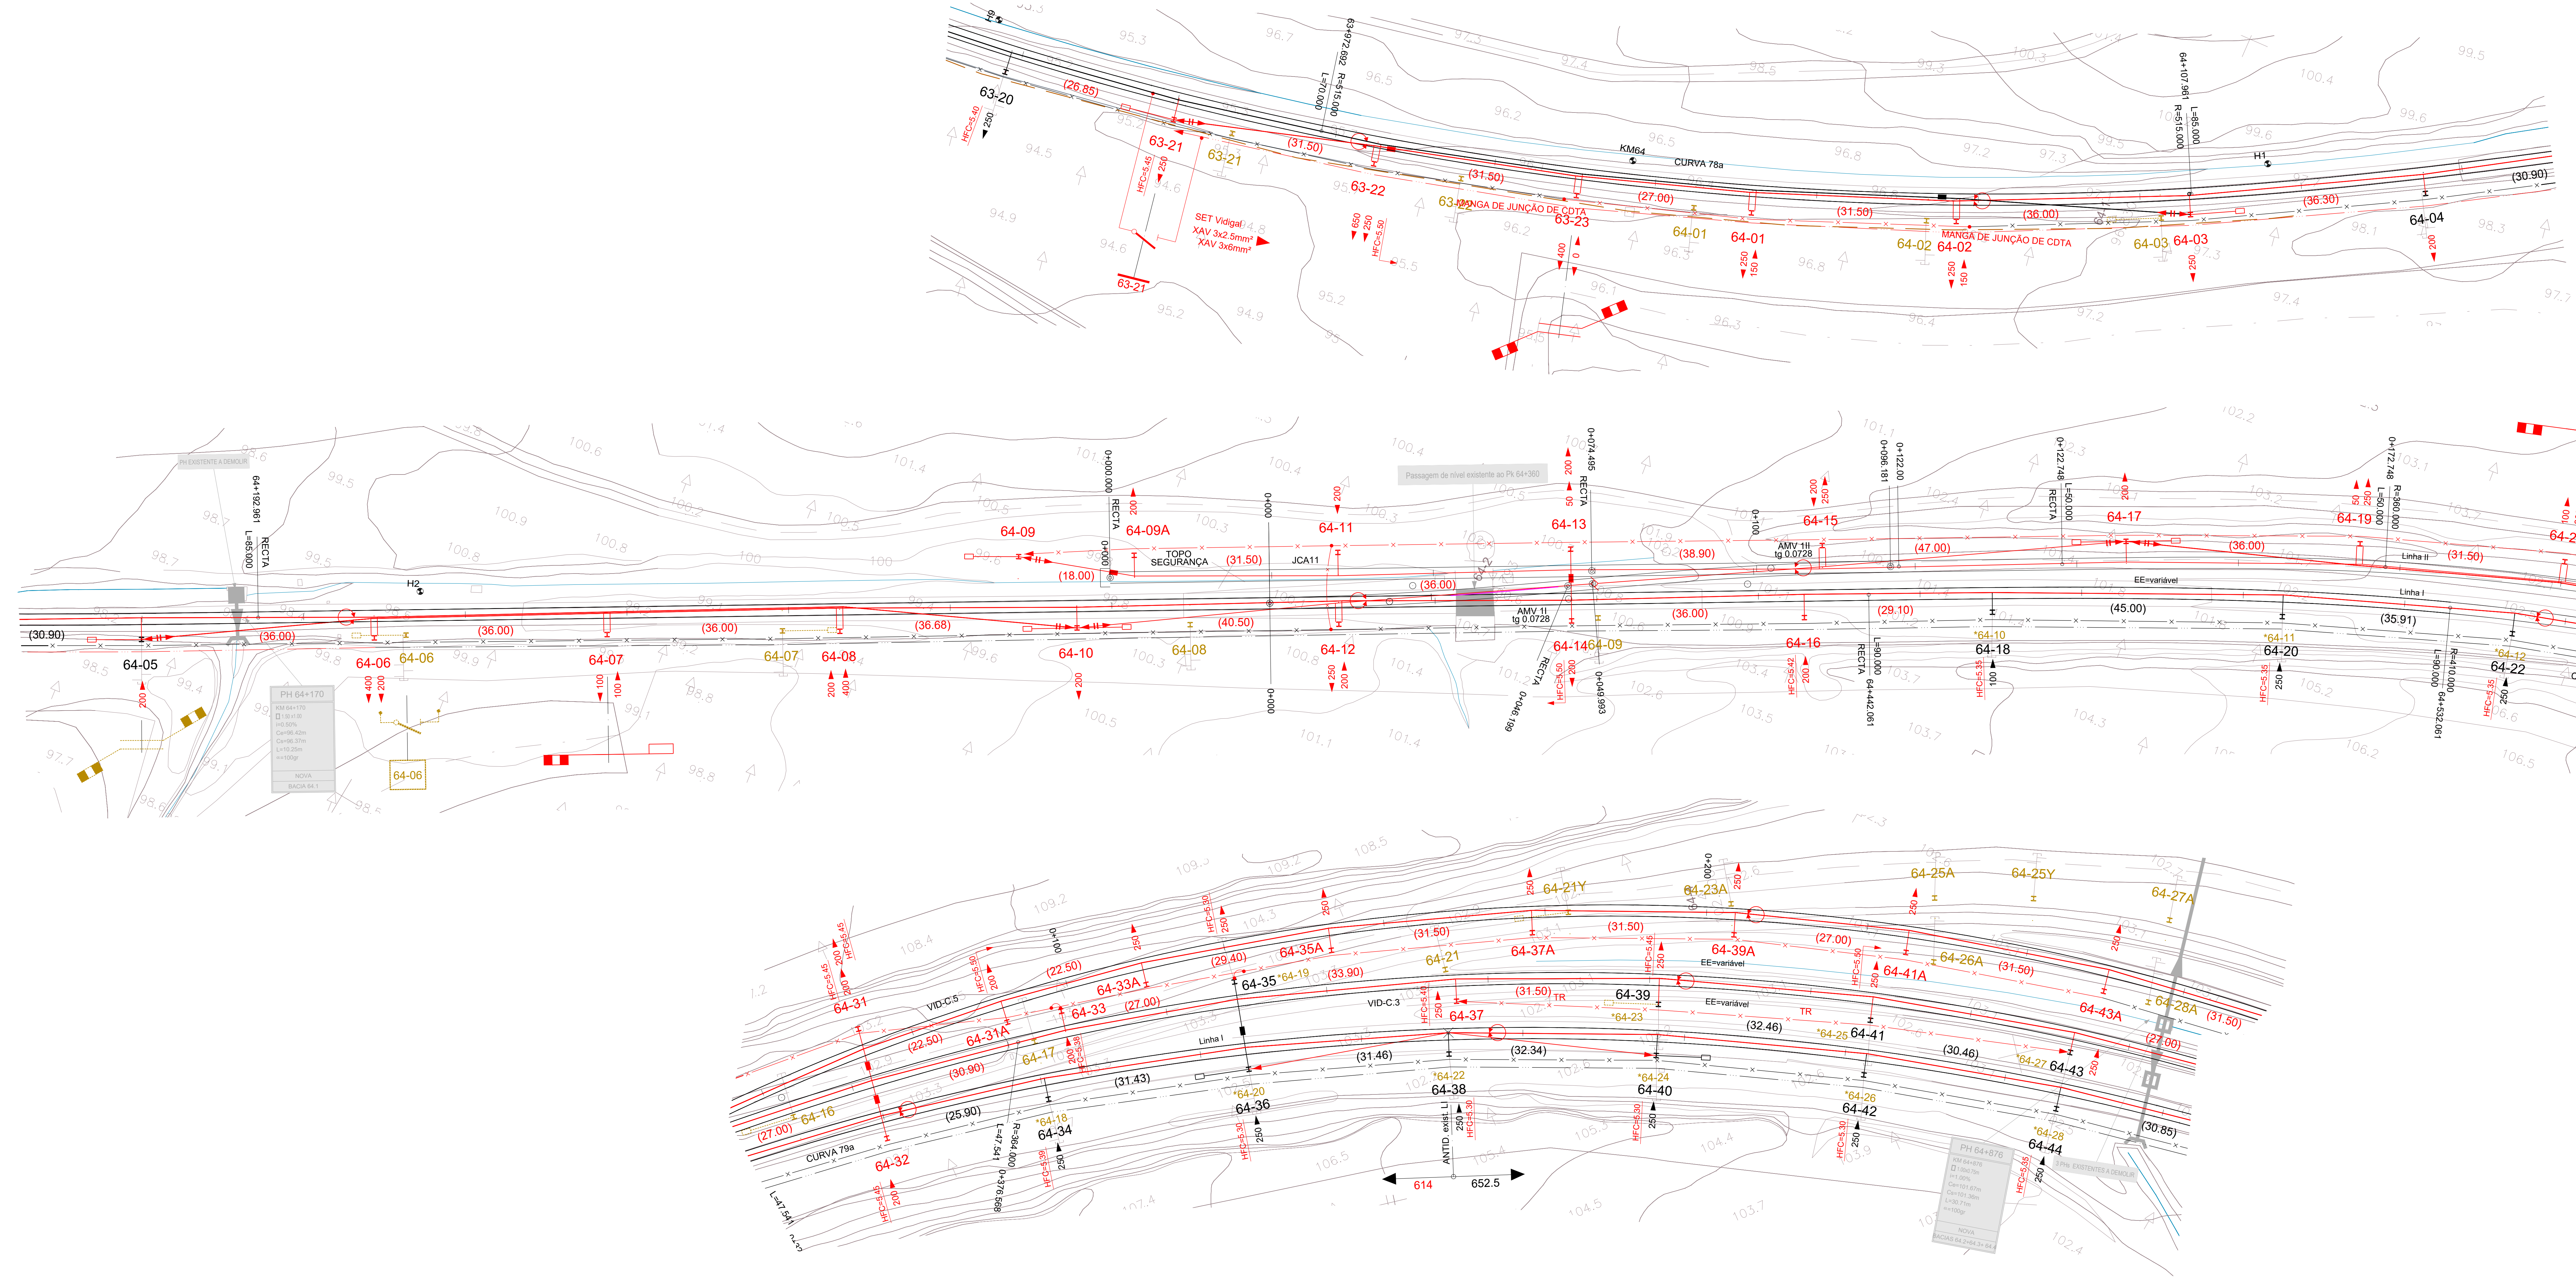

CURVAS								
Curva Nº		VID-C.1	VID-C.2	VID-C.3	VID-C.4	VID-C.5	VID-C.6	VID-C.7
Velocidade de cálculo	(km/h)	60	60	60	60	45	45	45
Rumo de entrada	(grados)	164.826434	187.556807	193.240305	248.717894	185.563083	248.717894	255.692670
Rumo de saída	(grados)	187.556807	193.240305	248.717894	247.758945	248.717894	255.692670	254.733722
Raio do troço circular	R (m)	360.000	600.000	364.000	1500.000	320.000	350.000	500.000
Desenvolvimento circular	Lcc (m)	128.537	53.566	259.013	22.595	297.451	38.346	7.532
Desenvolvimento da clotoide	Le (m)			47.541				
	Ls (m)			40.000		40.000		
Escala prática	D (mm)							
Insuficiencia de escala	I (mm)	137	82	135	33	87	79	27
Disfarce de escala dD/d l(mm/m)	em Le							
	em Ls							
Variação da insuficiencia de escala dI/dt (mm/s)	em Le			19				
	em Ls			56		27		
Variação de escala dD/dt (mm/s)	em Le							
	em Ls							
Coordenadas rectângulares dos pontos notáveis – Vértice	M	-29786.0227	-29768.2014	-29746.4109	-30198.7442	-29724.5086	-30158.8875	-30213.1302
	P	-106586.0097	-106676.0233	-106880.4715	-107351.4011	-106867.2525	-107326.2560	-107371.5722
Centro	M	-30126.5517	-30361.9818	-30126.6060	-29109.1135	-30075.3052	-30398.0138	-29889.6721
	P	-106719.6504	-106766.2620	-106750.5708	-108382.3389	-106770.2258	-107069.9612	-107752.8714
Ponto de tangência de entrada (PTE)	M	-29820.1152	-29773.4064	-29765.3610	-30190.9181	-29763.4983	-30145.5927	-30210.2402
	P	-106530.7148	-106649.7330	-106702.6730	-107343.2533	-106698.2783	-107312.4145	-107369.1578
Fim da clotóide de entrada (FCE)	M			-29762.6063				
	P			-106750.1121				
Início da clotóide de saída (ICS)	M			-29850.6368		-29831.1254		
	P			-106987.9249		-106977.0499		
Ponto de tangência de saída (PTS)	M	-29773.4064	-29765.3610	-29877.8091	-30206.4466	-29858.2227	-30173.6161	-30215.9835
	P	-106649.7330	-106702.6730	-107017.2717	-107359.6659	-107006.4639	-107338.5607	-107374.0299

LEGENDA

▬	Existente
🟥	a instalar / regular
– – – – –	a remover / desmontar
XX-XX *XX-XX I	Poste existente renumerado
XX-XX I	Poste projeto

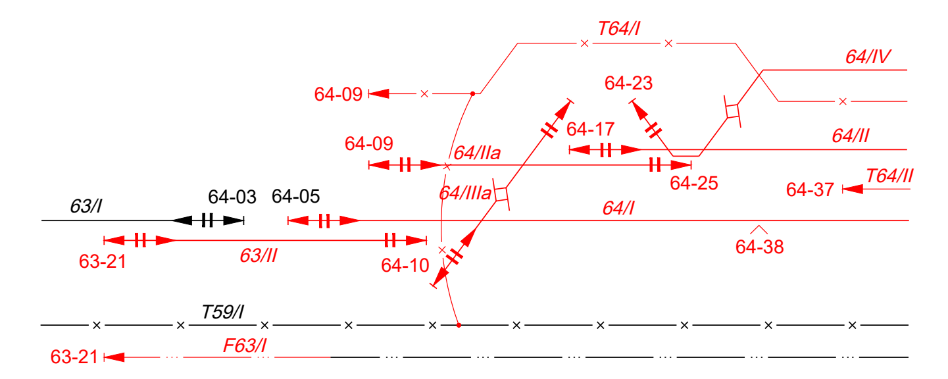

Elementos dos lanços

VIA	Nº LANÇO	POSTES EXTREMOS						COMPRIMENTOS							OBSERVAÇÕES
		Nº POSTE	F.C.	C.S.	Nº POSTE	F.C.	C.S.	LANÇO	C.S.	F.C.	Cabo Bz65 Subst. F.C.	Cabo Bz120 Subst. CAT	C.d.T.	FEEDER	
	63/II	63-21	AT	AT	64-10	FX	FX	370,0	370,0	318,0		52,0			Lanço de catenária nova
I	64/I	64-05	AT	AT	65-16	AT	AT	1266,5	1266,5	1196,5		70,0			Lanço de catenária nova
II	64/IIa	64-09	AT	AT	64-25	FX	FX	302,5	302,5	263,5		39,0			Lanço de catenária nova
II	64/II	64-17	AT	AT	65-24	AT	AT	1139,0	1139,0	1055,0		84,0			Lanço de catenária nova
S	64/IIIa	64-10	AT	AT	64-17	FX	FX	163,0	163,0	95,0		68,0			Lanço de catenária nova
III	64/IV	64-23	AT	AT	65-21	AT	AT	985,0	985,0	924,0		61,0			Lanço de catenária nova
II/III	T64/I	64-09			65-15								1146,0		Lanço existente com comprimento revisto
II	T64/II	64-37			64-43								159,0		Lanço CdTA novo
I	F63/I	63-21			2-21									1762,5	Lanço existente (antigo F64/I)com comprimento revisto

Notas e historial de Alterações

03 - Jun. 2026 - Instalação de CDTA novo entre os postes 63-23 e 64-02
02 - Set. 2020 - Revisão de acordo com comentários do parecer (Versão 01)
01 - Jan. 2020 - Revisão de acordo com comentários do parecer DMS 007- 2581030 de 2019-12-05

Logótipos e informação complementar
Projetista
PROFICO
PULCRUM
Geoárea

Data
Julho 2019
N.º Projetista
42517.PE.09.IFT.00.107_03

Levantou

Desenhou
Joana Girbal

Projetou
Paulo Lopes

Verificou
Carlos Lopes

Infraestruturas de Portugal
Direção de Empreendimentos Ferroviários

Linha
Linha de Vendas Novas

Local
Setil - Vendas Novas

Fase do Projeto
Projeto de Execução

Especialidade Técnica
Volume 09 - Instalações Fixas de Tração Elétrica

Nome do Empreendimento
Modernização da Linha de Vendas Novas

Título do Desenho
Vidigal
Planta de Piquetagem (1/2)
Pk 63.900 a Pk 64.900

ESTE DESENHO APENAS SE CONSIDERA VÁLIDO DESDE QUE ESTEJAM PREENCHIDOS OS CAMPOS DE APROVAÇÃO E INSERIDO O RESPETIVO NUMERO SAP

O Responsável por

O Diretor de Engenharia

Data

Escalas
1/500

Tipo	N.º SAP	N.º de Ordem no Projeto	Versão
317	10003833487	107	03

RE.FR.AGR.002 | V00