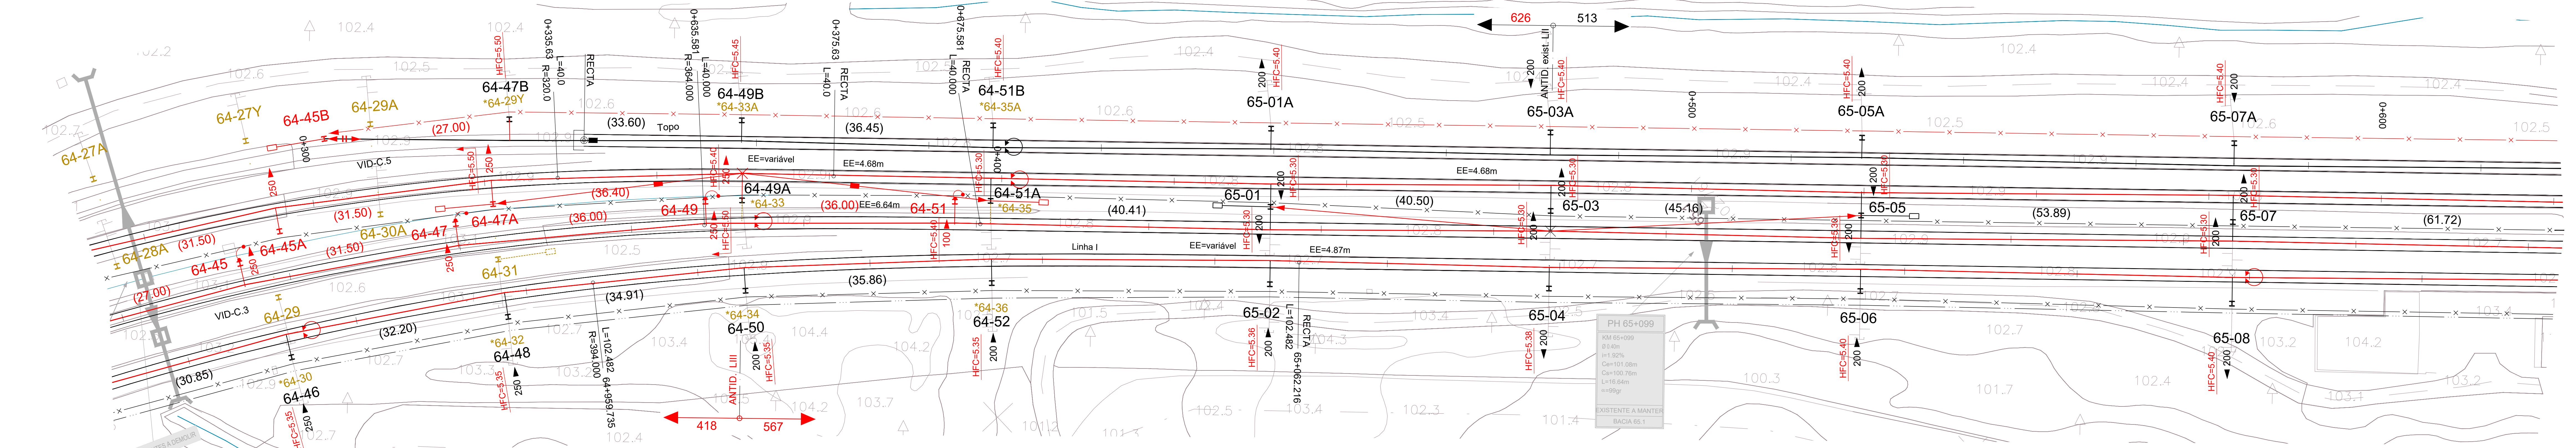

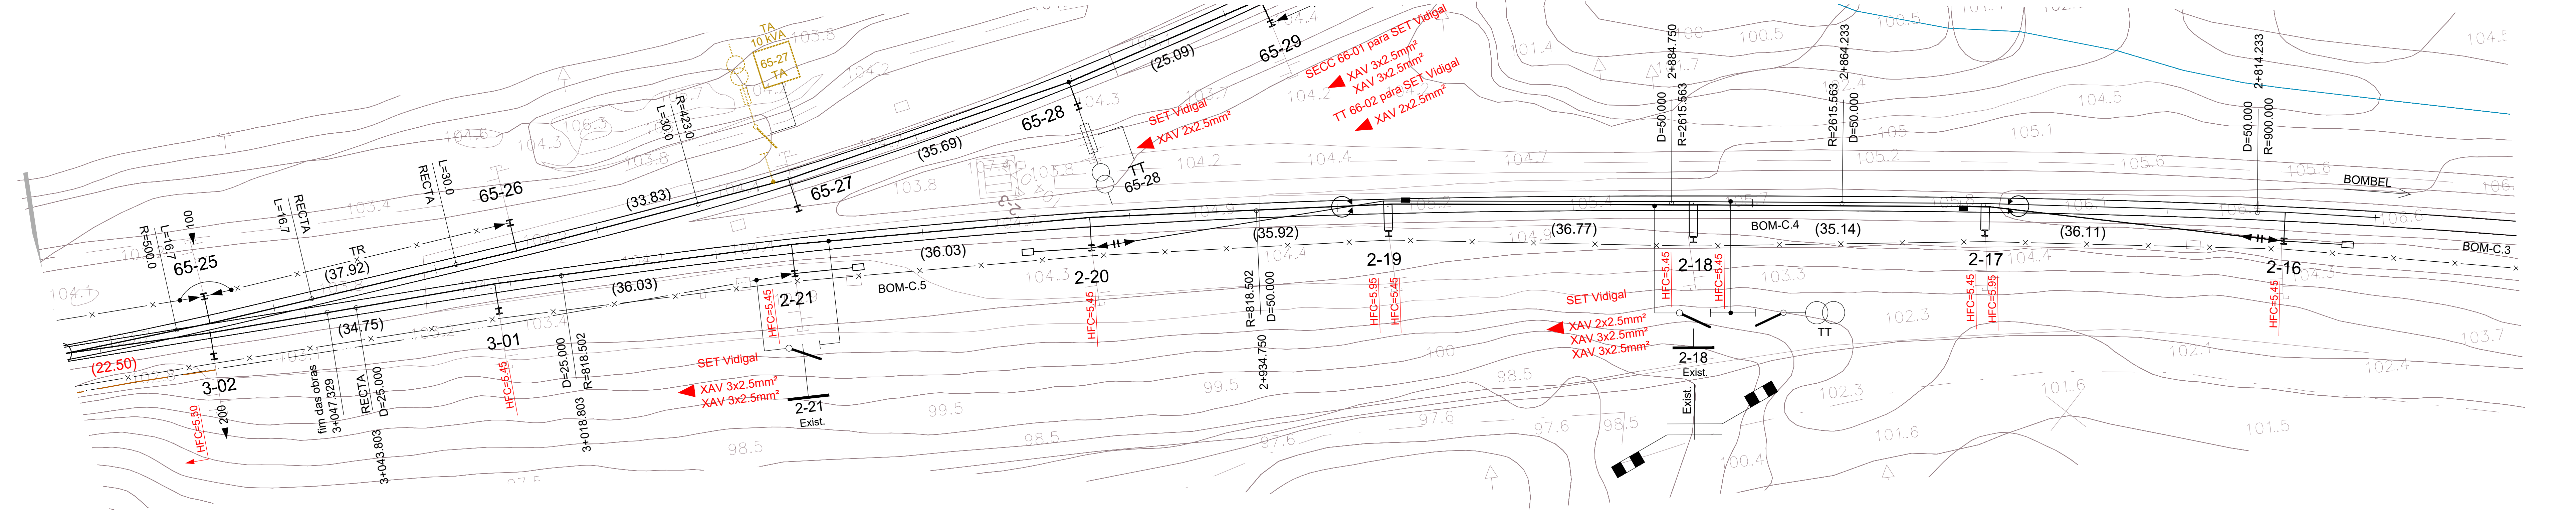

CURVAS									
Curva Nº			VID-C.1	VID-C.2	VID-C.3	VID-C.4	VID-C.5	VID-C.6	VID-C.7
Velocidade de cálculo		(km/h)	60	60	60	60	45	45	45
Rumo de entrada		(grados)	164.826434	187.556807	193.240305	248.717894	185.563083	248.717894	255.692670
Rumo de saída		(grados)	187.556807	193.240305	248.717894	247.758945	248.717894	255.692670	254.733722
Raio do troço circular		R (m)	360.000	600.000	364.000	1500.000	320.000	350.000	500.000
Desenvolvimento circular		Lcc (m)	128.537	53.566	259.013	22.595	297.451	38.346	7.532
Desenvolvimento da clotoide		Le (m)			47.541				
		Ls (m)			40.000		40.000		
Escala prática		D (mm)							
Insuficiencia de escala		I (mm)	137	82	135	33	87	79	27
Disfarce de escala dD/d l(mm/m)		em Le							
		em Ls							
Variação da insuficiencia de escala dI/dt (mm/s)		em Le			19				
		em Ls			56		27		
Variação de escala dD/dt (mm/s)		em Le							
		em Ls							
Coordenadas rectângulares dos pontos notáveis	Vértice	M	-29786.0227	-29768.2014	-29746.4109	-30198.7442	-29724.5086	-30158.8875	-30213.1302
		P	-106586.0097	-106676.0233	-106880.4715	-107351.4011	-106867.2525	-107326.2560	-107371.5722
	Centro	M	-30126.5517	-30361.9818	-30126.6060	-29109.1135	-30075.3052	-30398.0138	-29889.6721
		P	-106719.6504	-106766.2620	-106750.5708	-108382.3389	-106770.2258	-107069.9612	-107752.8714
	Ponto de tangência de entrada (PTE)	M	-29820.1152	-29773.4064	-29765.3610	-30190.9181	-29763.4983	-30145.5927	-30210.2402
		P	-106530.7148	-106649.7330	-106702.6730	-107343.2533	-106698.2783	-107312.4145	-107369.1578
	Fim da clotóide de entrada (FCE)	M			-29762.6063				
		P			-106750.1121				
	Início da clotóide de saída (ICS)	M			-29850.6368		-29831.1254		
		P			-106987.9249		-106977.0499		
	Ponto de tangência de saída (PTS)	M	-29773.4064	-29765.3610	-29877.8091	-30206.4466	-29858.2227	-30173.6161	-30215.9835
		P	-106649.7330	-106702.6730	-107017.2717	-107359.6659	-107006.4639	-107338.5607	-107374.0299

LEGENDA

—	Existente
—	a instalar / regular
– – – – –	a remover / desmontar
XX-XX *XX-XX I	Poste existente renumerado
XX-XX I	Poste projeto

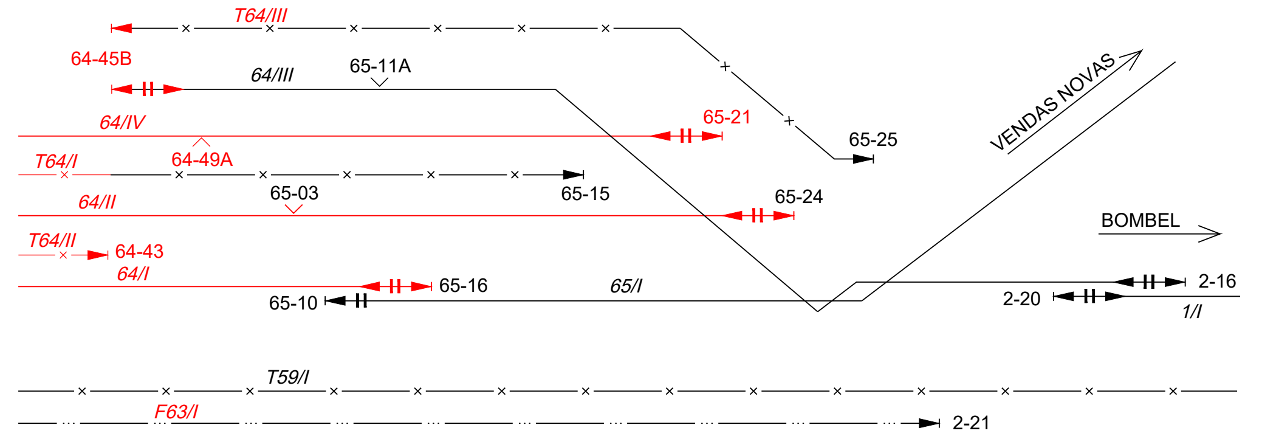

Elementos dos lanços

VIA	Nº LANÇO	POSTES EXTREMOS						COMPRIMENTOS							OBSERVAÇÕES
		Nº POSTE	F.C.	C.S.	Nº POSTE	F.C.	C.S.	LANÇO	C.S.	F.C.	Cabo Bz65 Subst. F.C.	Cabo Bz120 Subst. CAT	C.d.T.	FEEDER	
IV	64/III	64-45B	AT	AT	2-16	AT	AT	978,5	978,5	904,5		74,0			Lanço existente com comprimento revisto
I	65/I	65-10	FX	FX	65-32	AT	AT	Exist.	Exist.	Exist.	Exist.				Existente
IV	T64/III	64-45B			65-25								720,5		Lanço existente (antigo T65/I) com comprimento revisto

Notas e historial de Alterações

04 - Jun. 2026 - Instalação de CDTA novo entre os postes 64-45B e 65-15A
03 - Jul. 2025 - Demolição do PC do Vidigal e instalação de novos cabos de telecomando para SET Vidigal
02 - Set. 2020 - Revisão de acordo com comentários do parecer (Versão 01)
01 - Jan. 2020 - Revisão de acordo com comentários do parecer DMS 007- 2581030 de 2019-12-05

Logótipos e informação complementar

Projetista

PROFICO
PROJETOS, FISCALIZAÇÃO E CONSULTORIA
FULCRUM
Geoárea

Data
Julho 2019
N.º Projetista
42517.PE.09.IFT.00.108_04

Levantou

Desenhou
Joana Girbal

Projetou
Paulo Lopes

Verificou
Carlos Lopes

Infraestruturas de Portugal
Direção de Empreendimentos Ferroviários

Linha
Linha de Vendas Novas

Local
Setil - Vendas Novas

Fase do Projeto
Projeto de Execução

Especialidade Técnica
Volume 09 - Instalações Fixas de Tração Elétrica

Nome do Empreendimento
Modernização da Linha de Vendas Novas

Título do Desenho
Vidigal
Planta de Piquetagem (2/2)
Pk 64.900 a Pk 65.600

ESTE DESENHO APENAS SE CONSIDERA VÁLIDO DESDE QUE ESTEJAM PREENCHIDOS OS CAMPOS DE APROVAÇÃO E INSERIDO O RESPETIVO NUMERO SAP

O Responsável por

O Diretor de Engenharia
Data

Escalas	Tipo	N.º SAP	N.º de Ordem no Projeto	Versão
1/500	317 -	10003833488 -	108 -	04

RE.FR.AGR.002 \| V00