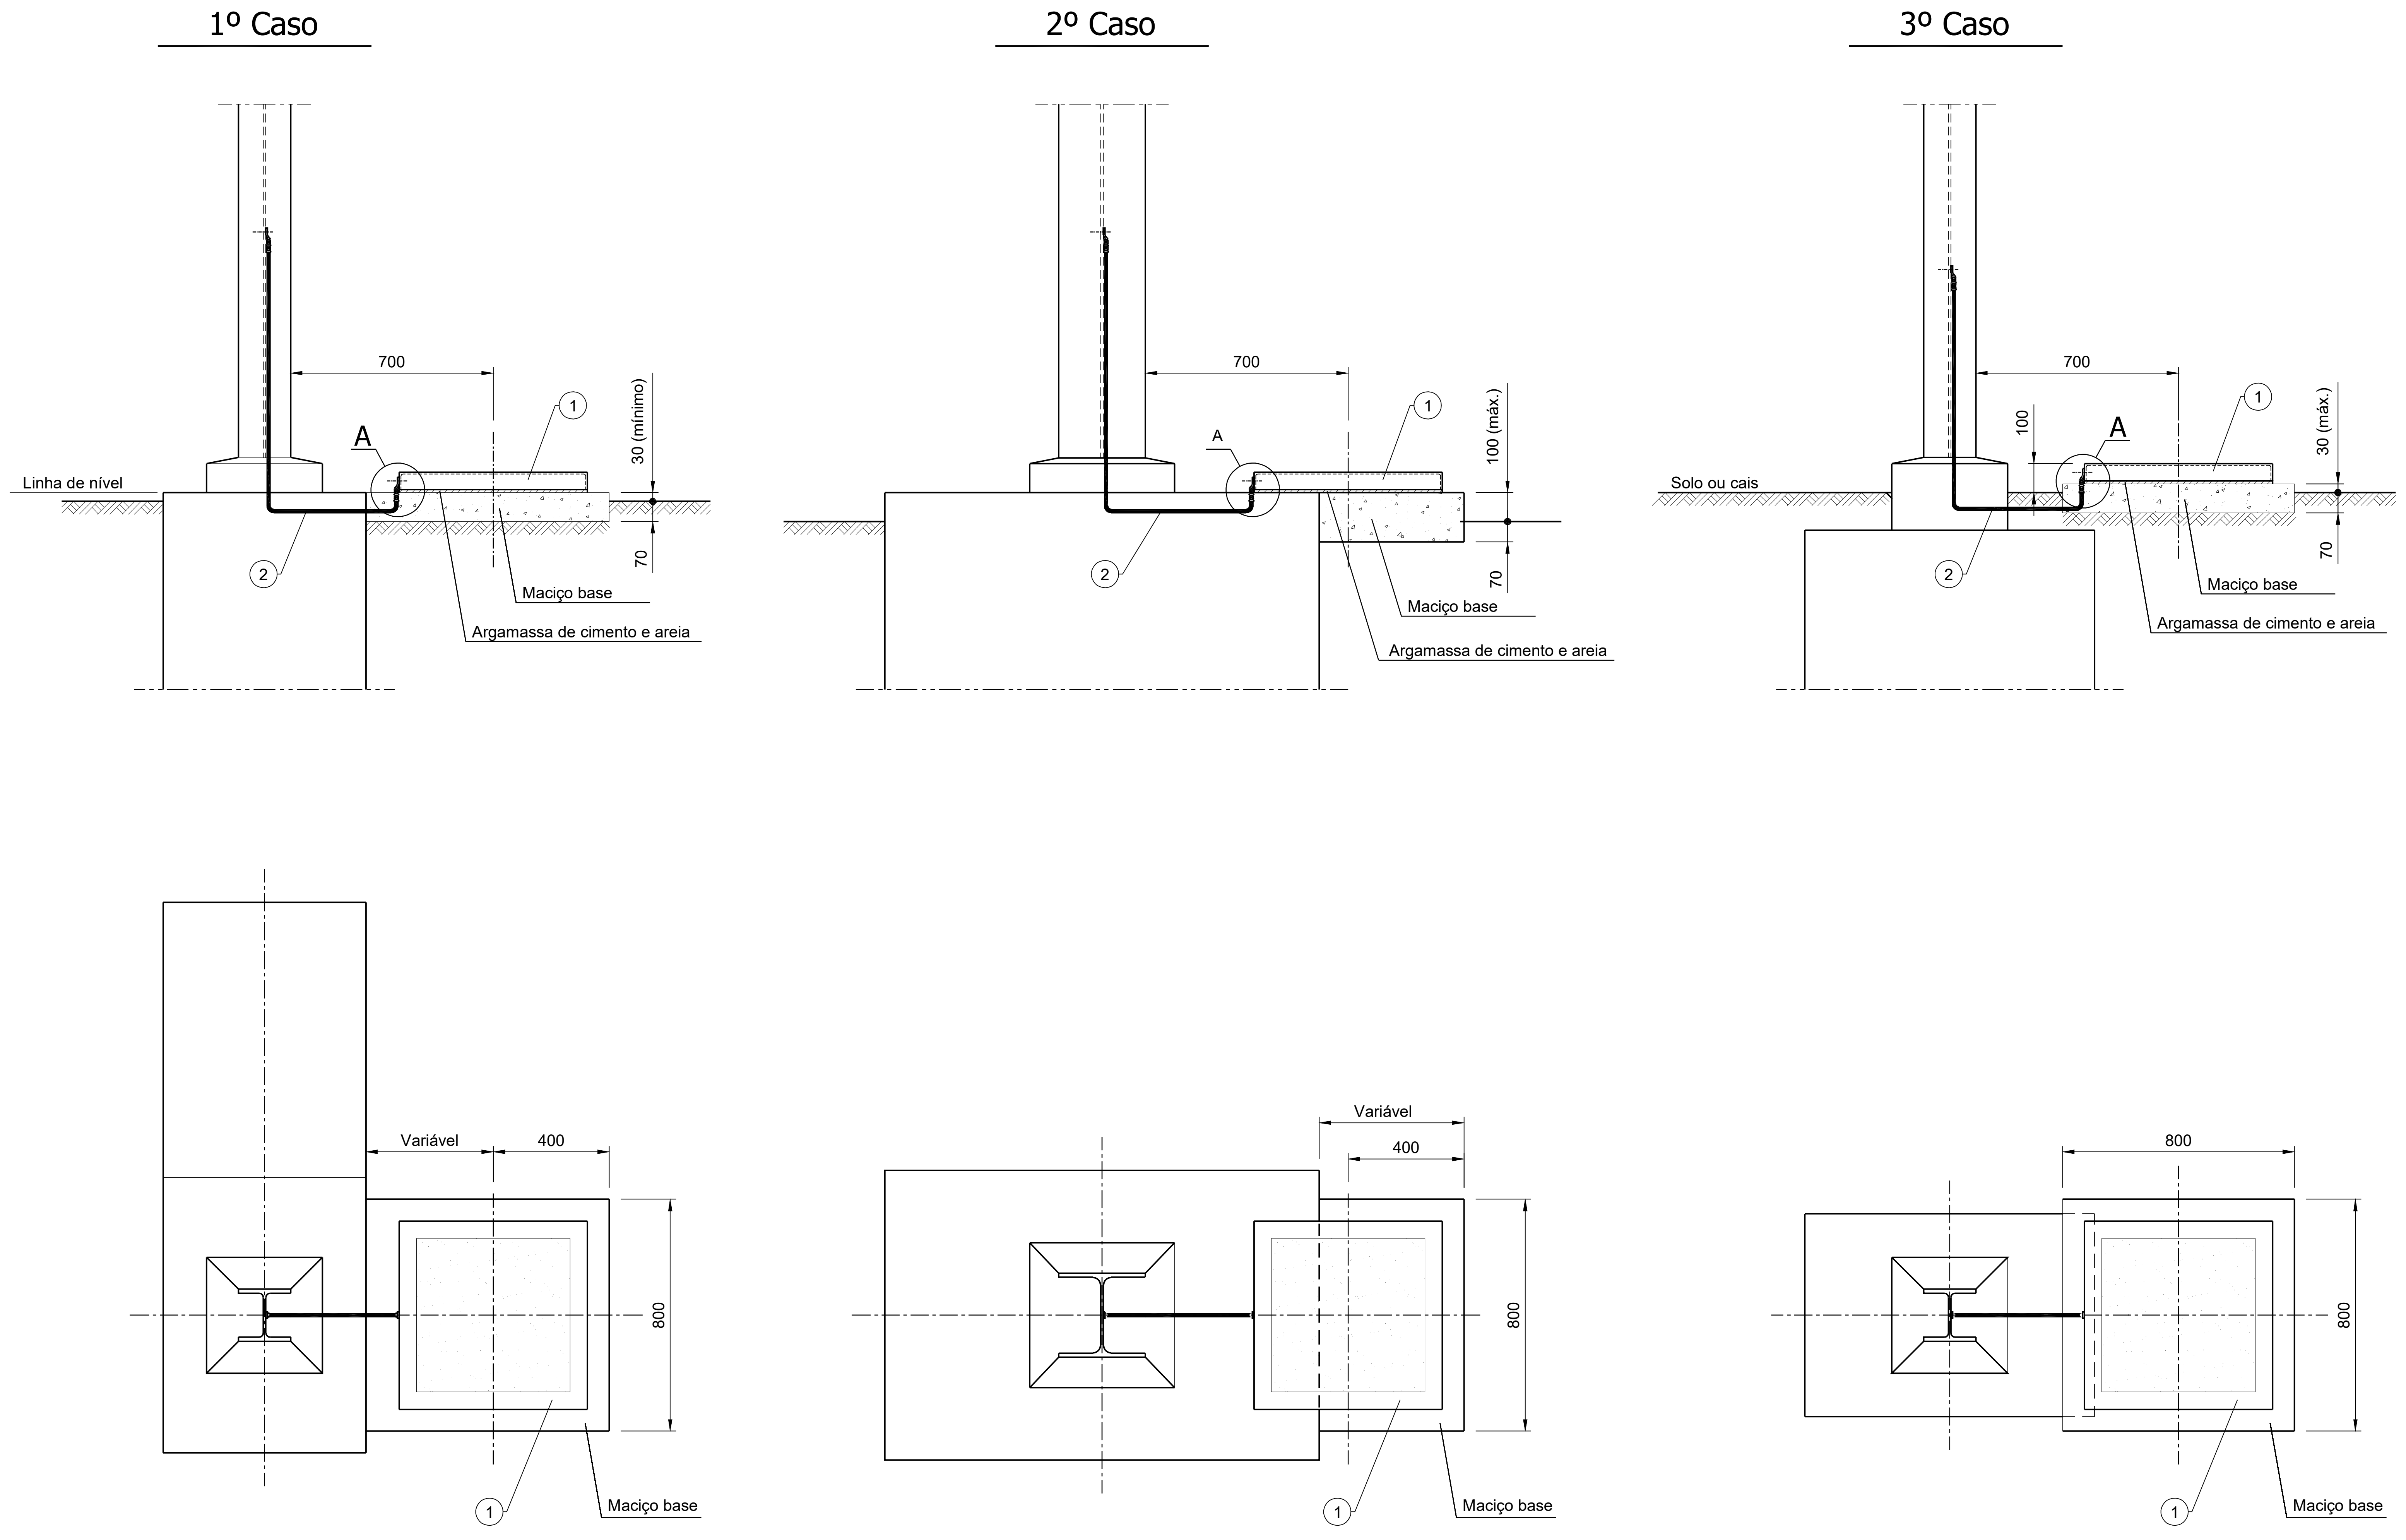
1º Caso

2º Caso

3º Caso


Pormenor "A"

(Ligação na plataforma de manobra)

(Esc.1:5)

Notas:

- Em princípio a plataforma de manobra será montada sobre a linha de nível do maciço do poste (1º e 2º casos). Assim os maciços dos postes com seccionadores, não deverão ter mais de 0,10 m acima do solo;

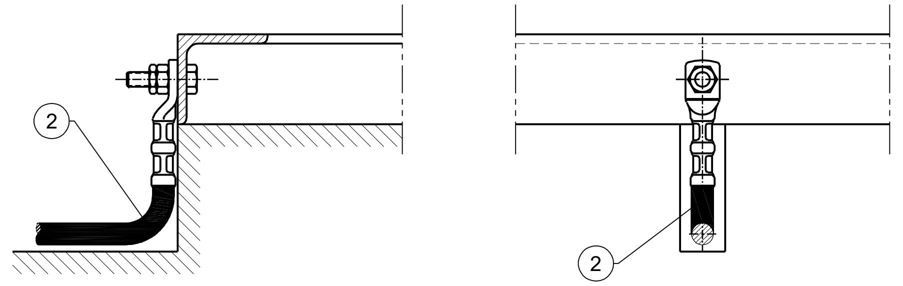- Nos casos em que o maciço do poste esteja a nível inferior do solo (ou cais), a plataforma de manobra será montada a 0,10 m acima do nível destes (3º caso);

- O assentamento da plataforma deve ser sempre feito sobre um maciço base em betão simples, quando montada total ou parcialmente fora do maciço do poste (1º, 2º, e 3º casos);

- A ligação da plataforma ao maciço base ou ao maciço do poste é feita por uma argamassa de cimento e areia.

Quant.	DESIGNAÇÃO	DESENHO	NOMENCLAT.	REF.ª	CÓDIGO (GR.MN.CAT.003)	OBSERVAÇÕES
1	Ligação de Terra do Poste à Plataforma de Manobra	EC-176		2		Montagem L
1	Plataforma de Manobra Cód. 716	C-7238	75185005	1	07.300.15	

Notas e historial de alterações

Alterações	Designação	Assinatura	Data
B	Alteração nas referências	Hugo Serieiro	11/2019
A	Sistema de terras universal	Feliciano Fernandes	12/2003

Logótipos e informação complementar
Projetista
Data
08-11-2019
N.º Projetista
C-7239

Levantou
Desenhou
Feliciano Fernandes
Projetou
Hugo Serieiro
Verificou
Marco Santos

Infraestruturas
de Portugal

Direção de Engenharia e Ambiente

Unidade de Catenária e Energia de Tração

Especialidade Técnica
CATENÁRIA E ENERGIA DE TRAÇÃO

Título do Desenho
MONTAGEM DA PLATAFORMA DE MANOBRA

ESTE DESENHO APENAS SE CONSIDERA VÁLIDO DESDE QUE ESTEJAM PREENCHIDOS OS CAMPOS DE APROVAÇÃO E INSERIDO O RESPETIVO NUMERO SAP

O Responsável por
Catenária e Energia de tração
Marco Santos

O Responsável por
Estudos e Projetos Ferroviários
Fernando Vendas

O Diretor de Engenharia e Ambiente
José Santinho Faísca
Data
08-11-2019

Escalas
1:5 e 1:20

Tipo		N.º SAP		N.º de Ordem no Projeto		Versão
222	-	10002001013	-	-	-	01