MONTAGEM I

Esc. 1:30

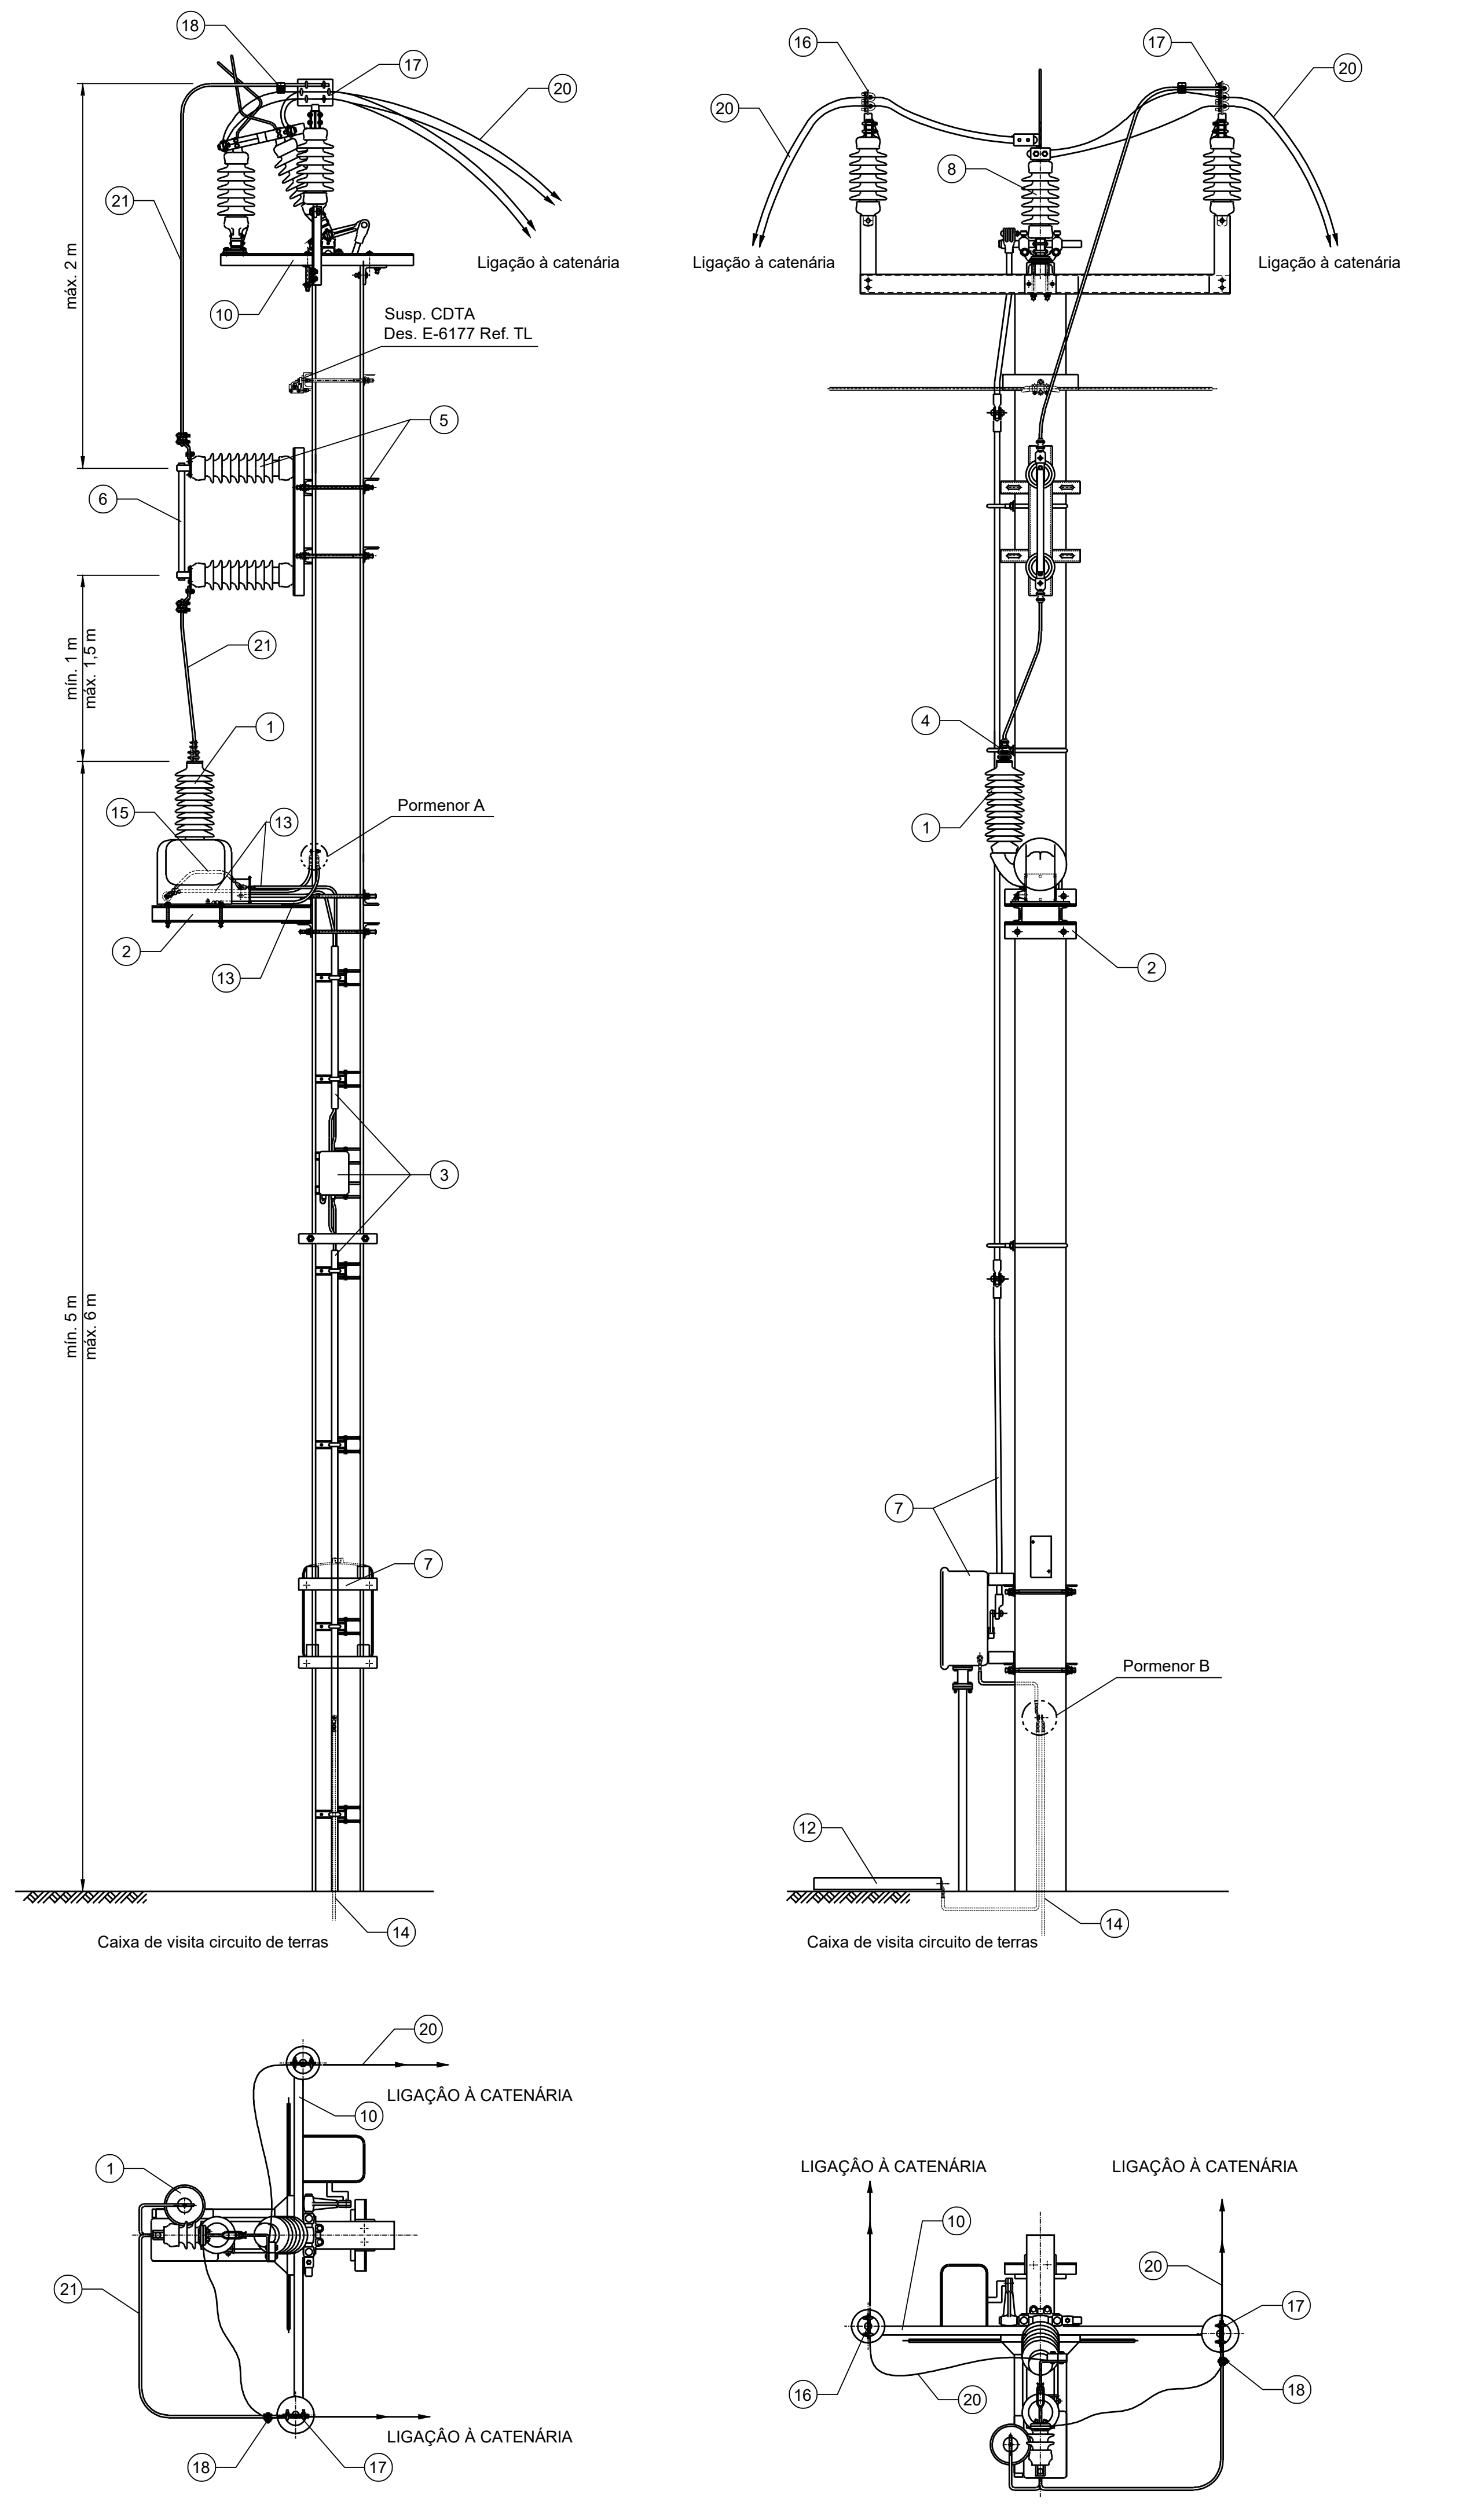
18
17
20
21
10
Susp. CDTA
Des. E-6177 Ref. TL
5
6
21
1
15
13
Pormenor A
2
13
3
7
máx. 2 m
mín. 1 m
máx. 1,5 m
mín. 5 m
máx. 6 m
Ligação à catenária
16
17
20
8
4
1
2
7
12
Pormenor B
14
Caixa de visita circuito de terras
Ligação à catenária
LIGAÇÃO À CATENÁRIA
LIGAÇÃO À CATENÁRIA
LIGAÇÃO À CATENÁRIA
10
21
18
17

MONTAGEM II

Esc. 1:30

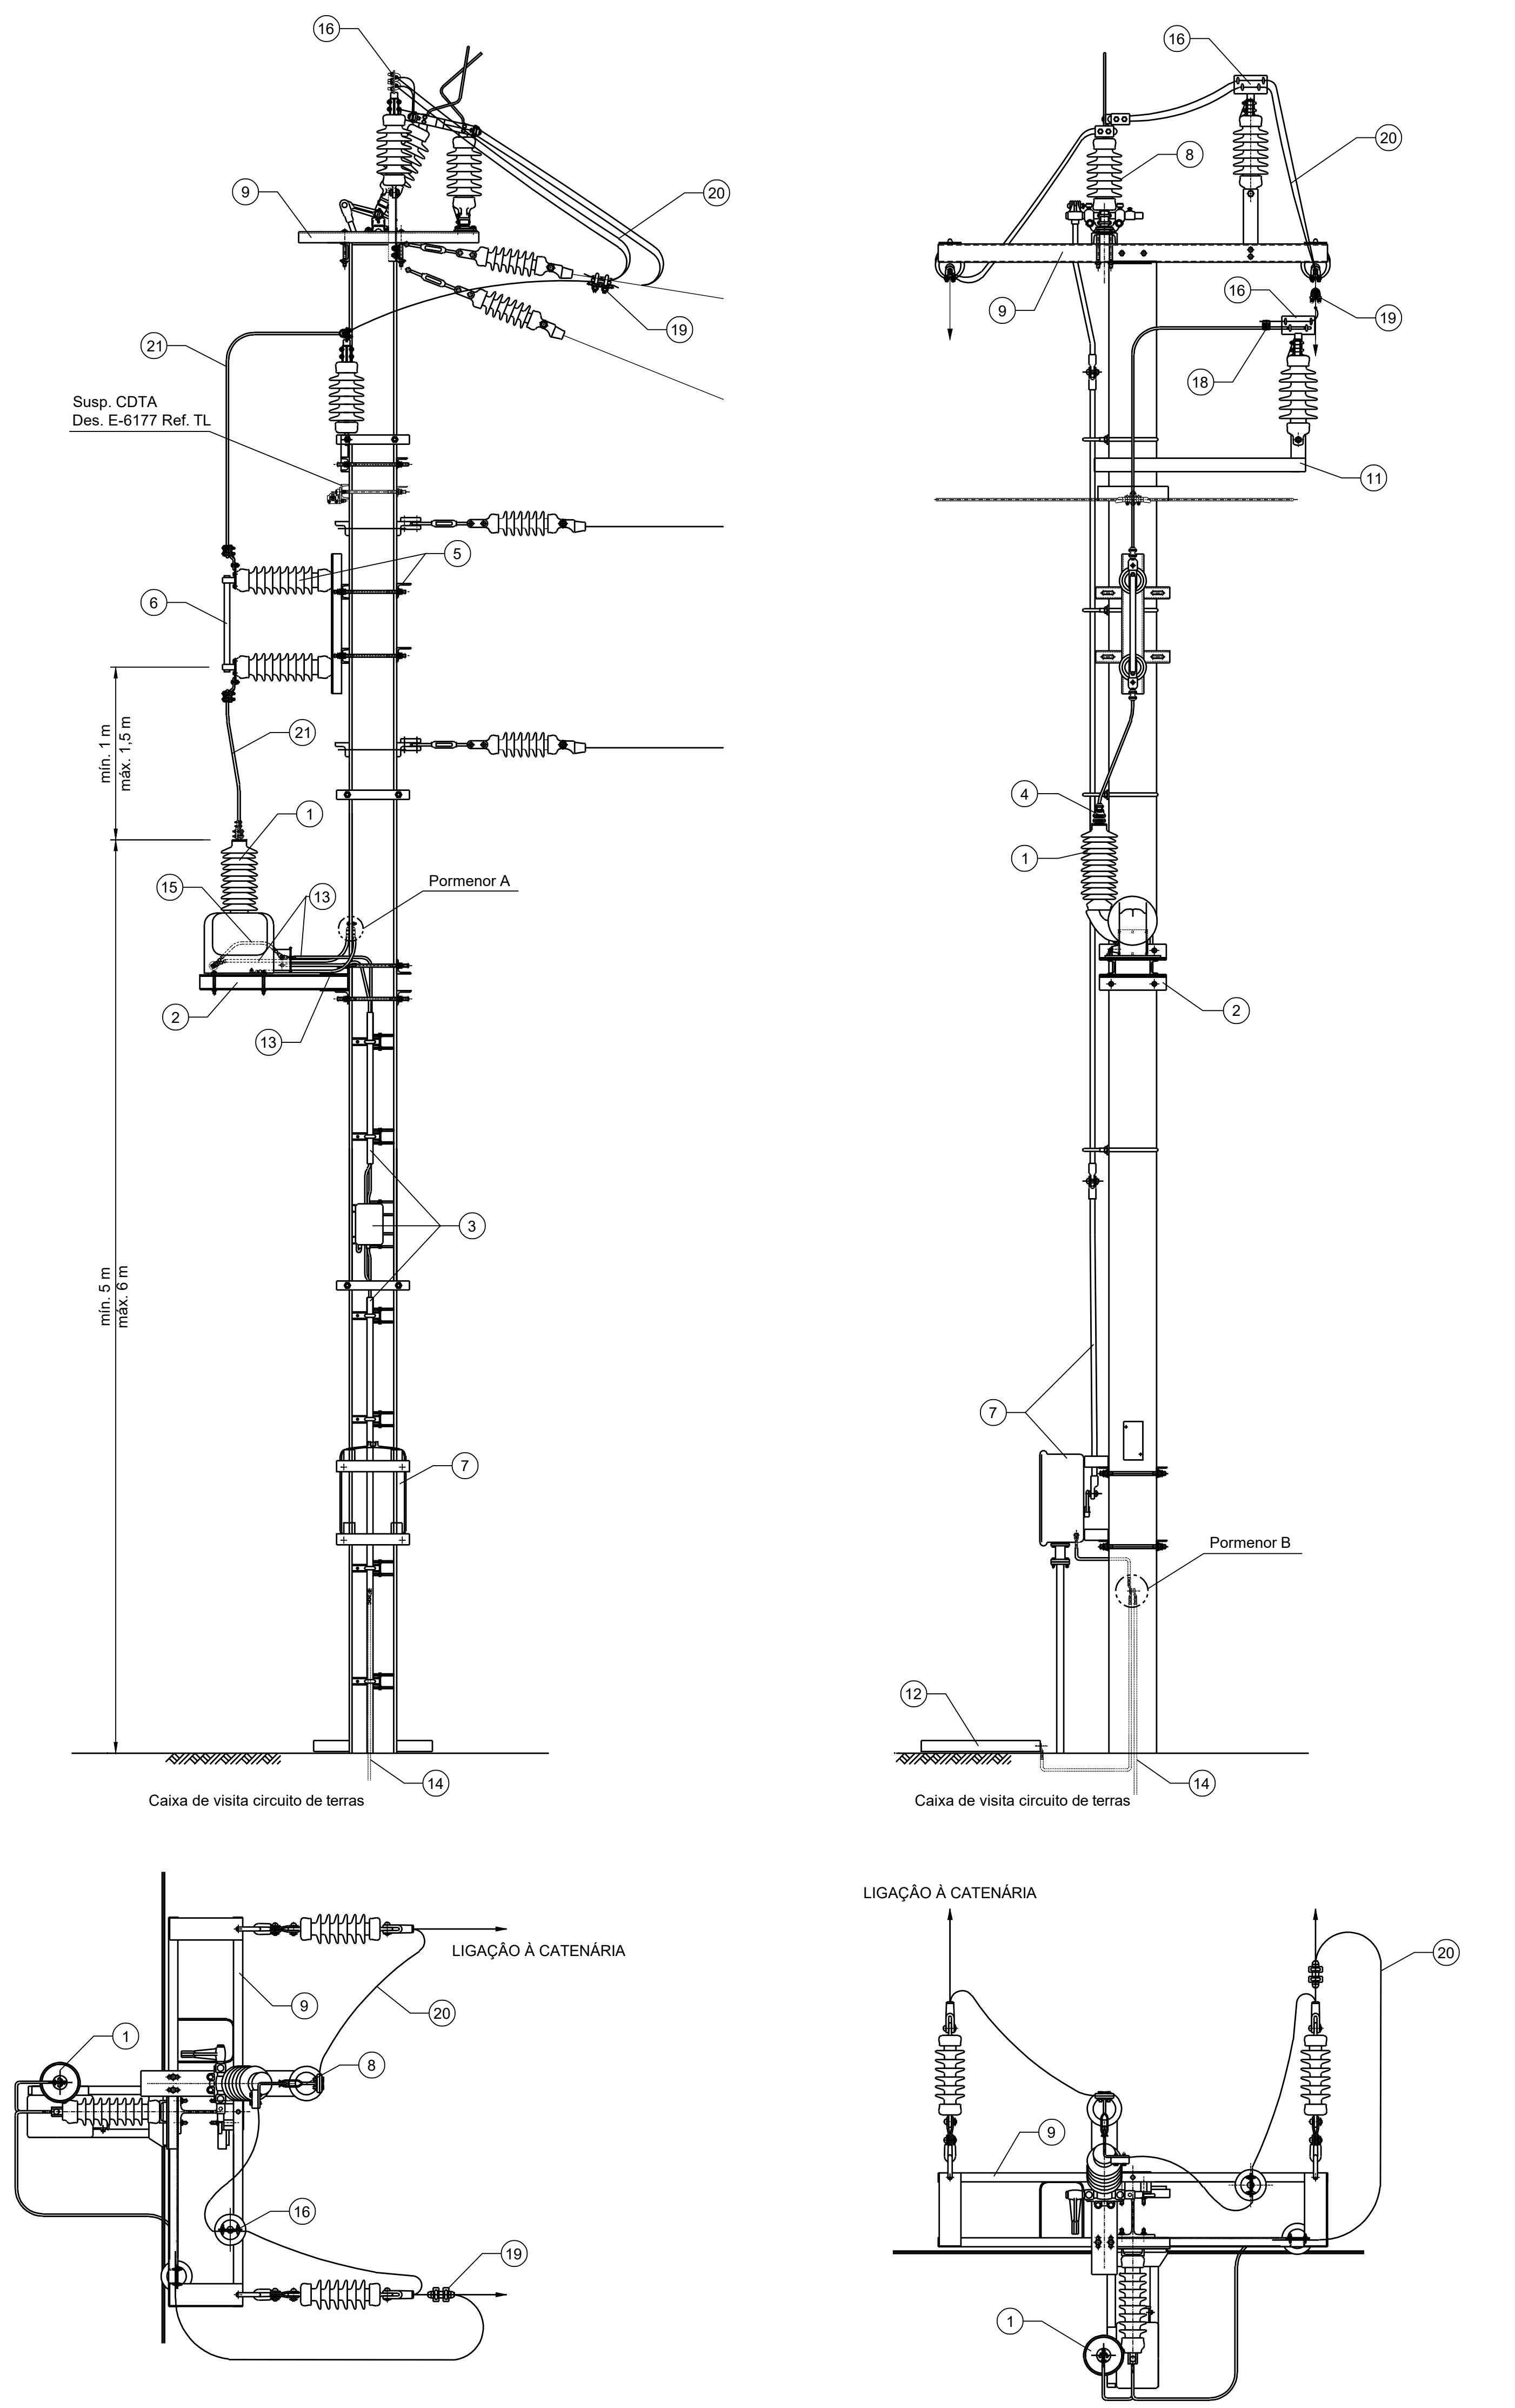
16
9
20
19
21
Susp. CDTA
Des. E-6177 Ref. TL
5
6
21
1
15
13
Pormenor A
2
13
3
7
mín. 1 m
máx. 1,5 m
mín. 5 m
máx. 6 m
Caixa de visita circuito de terras
14
16
8
20
9
19
16
18
11
4
1
2
7
12
Pormenor B
LIGAÇÃO À CATENÁRIA
LIGAÇÃO À CATENÁRIA
1
9
8
16
19
20

POSTO AUXILIAR

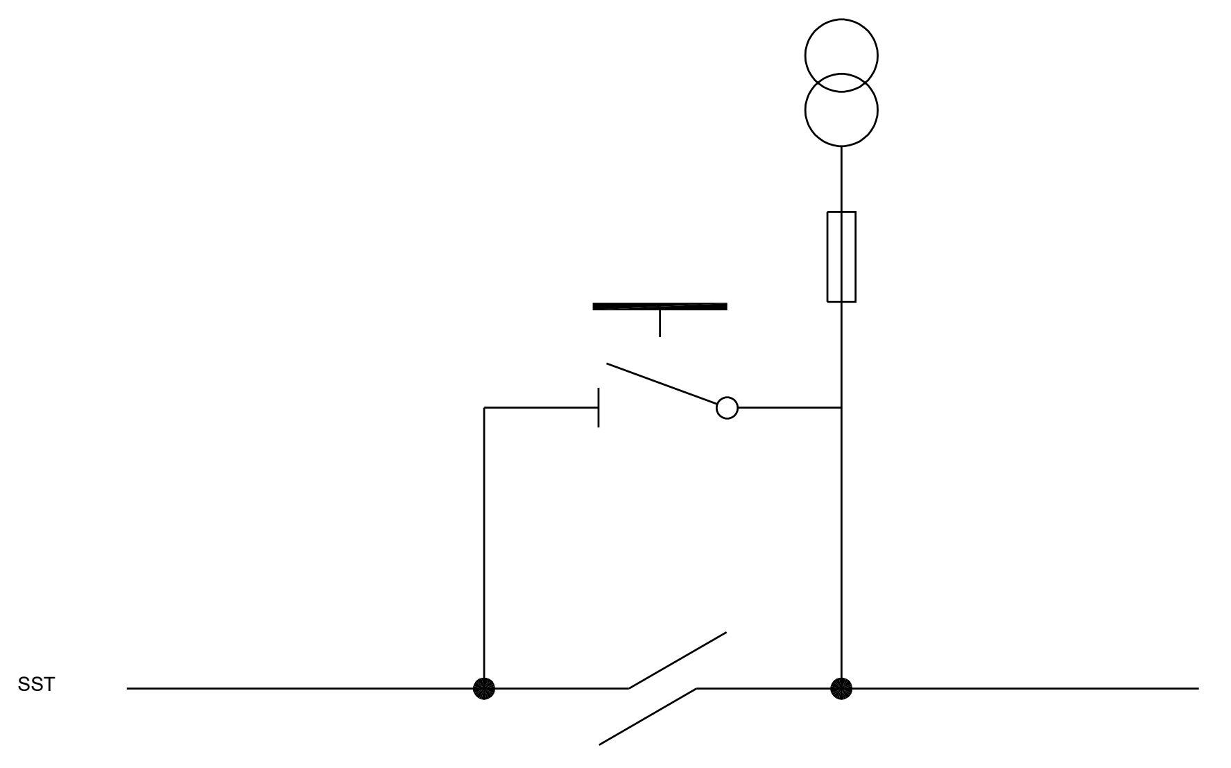

PORMENOR A

Esc. 1:2.5

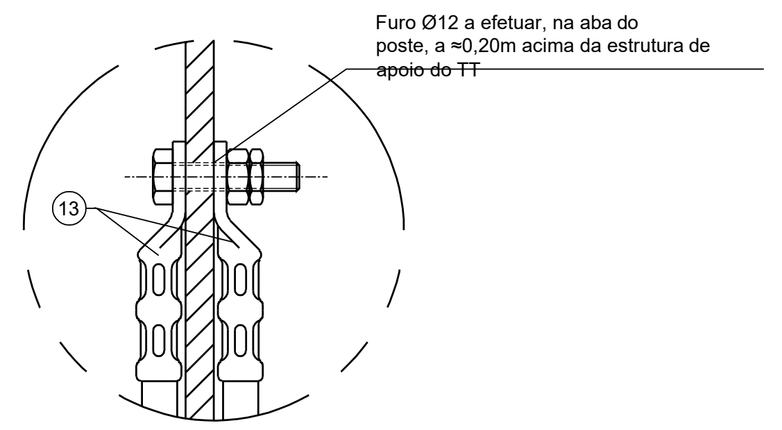
Furo Ø12 a efetuar, na aba do poste, a ≈0,20m acima da estrutura de apoio do TT
13

PORMENOR B

Esc. 1:2.5

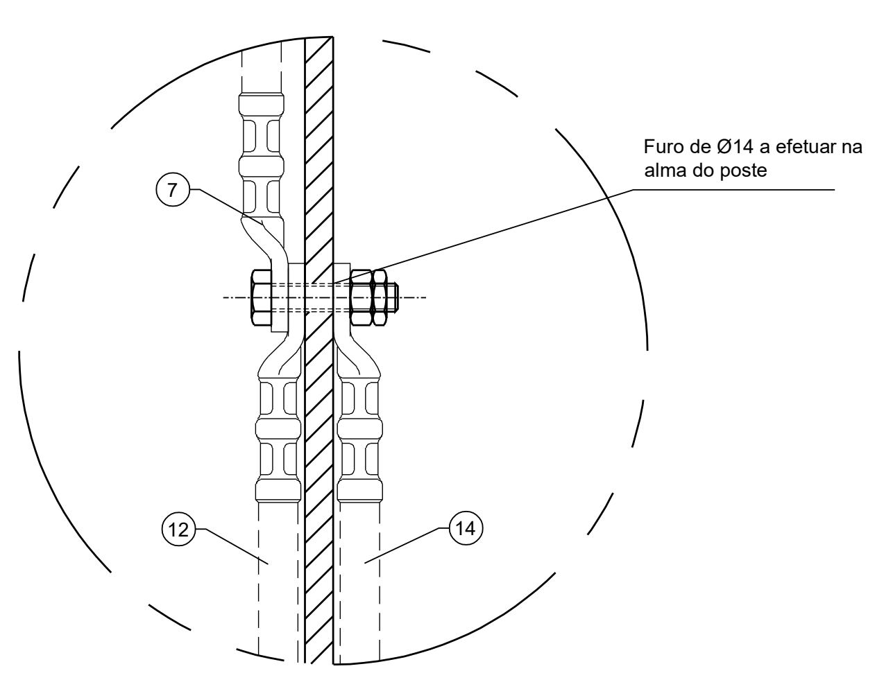
Furo de Ø14 a efetuar na alma do poste
7
12
14

TIPO TT	DESENHO TT	NOMENCLAT. TT	CÓDIGO TT (GR.MN.CAT.003)
RS ISOLEC E52CV	EC-319	75426311	08.101.02
SADTEM BBY2-1330	EC-290	75426310	08.101.01

ESQUEMA DE LIGAÇÃO DO TRANSFORMADOR DE TENSÃO EM SISTEMA DE TERRA UNIVERSAL

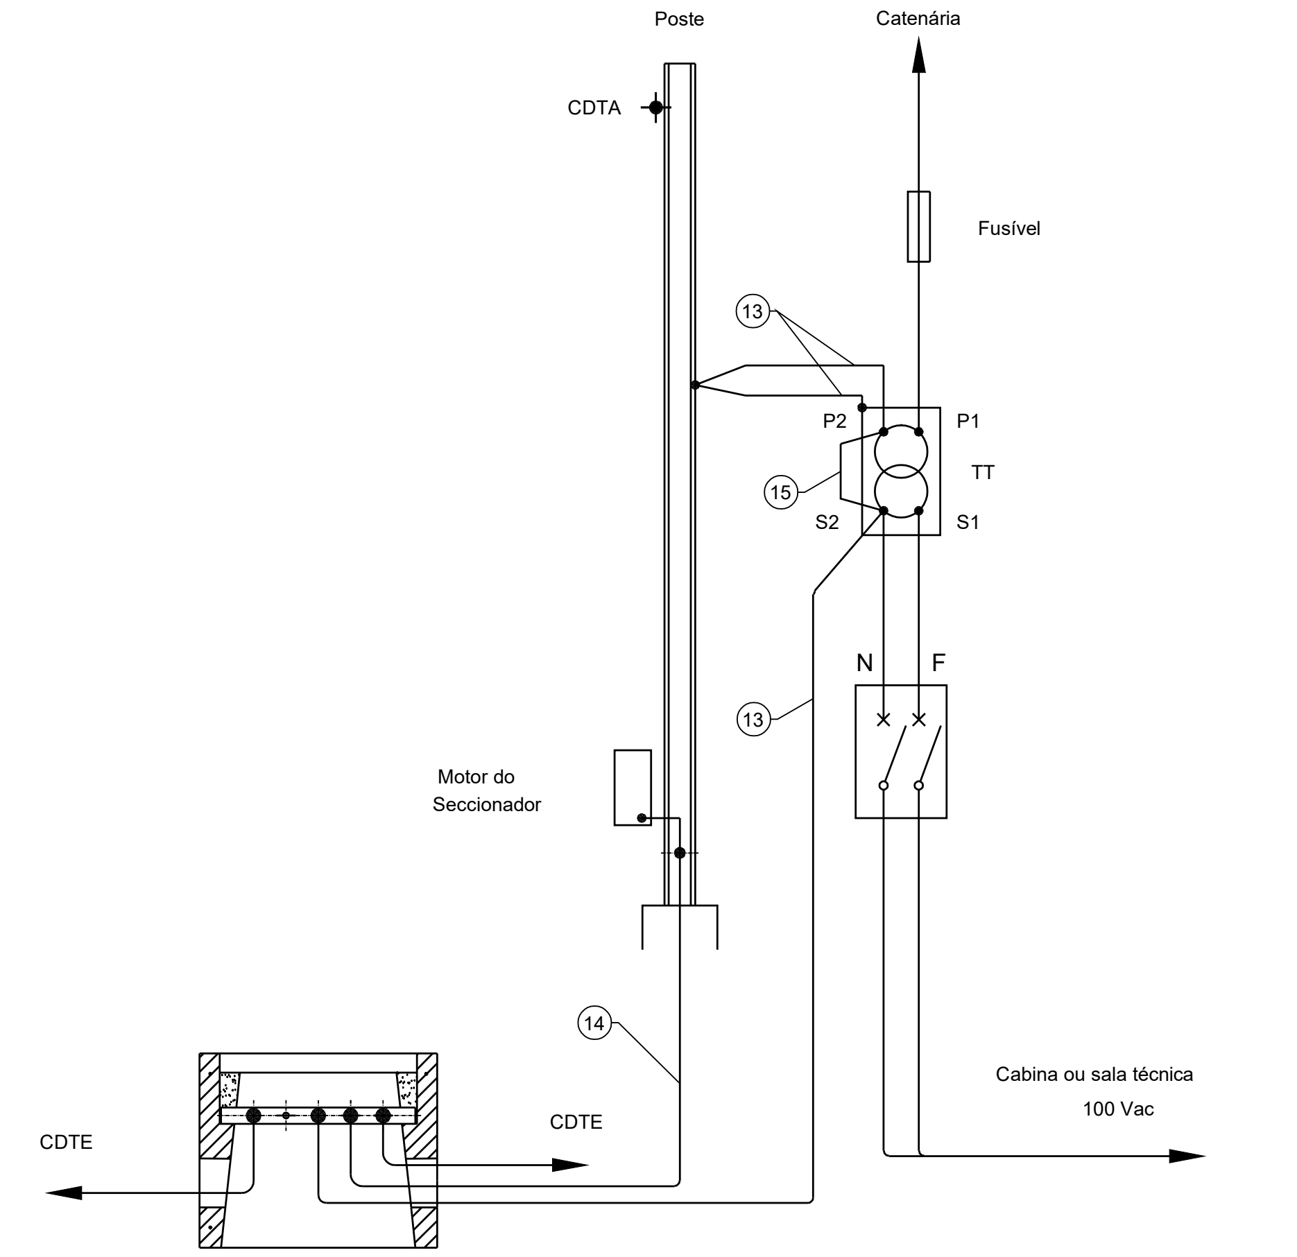
Poste
Catenária
CDTA
Fusível
13
P2
P1
15
TT
S2
S1
N
F
13
Motor do Seccionador
14
Cabina ou sala técnica
100 Vac
CDTE
CDTE

NOTA:

Para pormenores do atravessamento dos cabos no maciço, ver GR.IT.CAT.004 Capítulo 12.

a) Nas ligações alumínio/cobre serão utilizados terminais bimetálicos.

Quant. II	Quant. I	DESIGNAÇÃO	DESENHO	NOMENCLAT.	REF.ª	CÓDIGO (GR.MN.CAT.003)	OBSERVAÇÕES
qb	qb	Fio de contacto Cód. 9S		75184160	21	01.100.12	
qb	qb	Cabo flexível Cu 95mm2 Cód. 9P		75184021	20	01.100.11	
1	-	Ligador bifilar Cód. 552	EC-285	75114275	19	05.101.04	
1	1	Garra de aperto para cabos Cód. 360	44009	75162005	18	05.100.02	Ref. 1 a 5
-	1	Suporte de apoio para 3 cabos	EC-212		17		Mont. IV
2	1	Suporte de apoio para 2 cabos			16		Mont. I
1	1	Ligação entre neutros do TT	EC-176		15		Mont. LBB, a)
1	1	Ligação poste/caixa de visita			14		Mont. AC
3	3	Ligação do neutro do TT ao poste e caixa de visita			13		Mont. LB, a)
1	1	Plataforma de manobra	C-7239		12		
1	-	Suporte de fixação para 1 isolador de apoio	EC-120		11		Mont. I
-	1	Estrutura p/ 1 seccionador	E-7181		10		
1	-	Estrutura p/ 1 seccionador c/ transversal de alimentação	C-942		9		Mont. I
1	1	Seccionador (ZT ou ZM) Cód. 623E ou 623F	E-6145	75190047 75190048	8	07.300.01 07.300.02	Mont. I ou III
1	1	Comando do seccionador	C-3393		7		Mont. IIC
1	1	Fusível 36 kV com Percutor de 2,0 A		75426210	6	08.101.09	
1	1	Montagem do porta fusível	EC-278		5		Mont. I, II ou III
1	1	Terminal para transformador de tensão	EC-279	75426230	4	08.200.03	
1	1	Ligação do transformador (Lado BT)	C-12136		3		Mont. II
1	1	Estrutura de apoio do T.T.	E-3309		2		Mont. A, B ou C
1	1	Transformador de medida de tensão			1		Ver quadro

II: Ligação à Catenária c/ Trasv. de Alimentação

I: Ligação à Catenária s/ Trans. de Alimentação

Notas e historial de alterações

Alterações	Designação	Assinatura	Data
D	Alterações nas referências e introdução de códigos e nomenclaturas	Hugo Serieiro	12/2019
C	Correção do número SAP	Feliciano Fernandes	01/2014

Logótipos e informação complementar

Projetista

Data
30-12-2019
N.º Projetista

EC-258

Levantou

Desenhou
Feliciano Fernandes

Projetou
Hugo Serieiro

Verificou
Marco Santos

MONTAGEM

Infraestruturas de Portugal

Direção de Engenharia e Ambiente

Unidade de Catenária e Energia de Tração

Especialidade Técnica

CATENÁRIA E ENERGIA DE TRAÇÃO

Título do Desenho

POSTO AUXILIAR
(SEM SECCIONADOR NO T.T.)

ESTE DESENHO APENAS SE CONSIDERA VÁLIDO DESDE QUE ESTEJAM PREENCHIDOS OS CAMPOS DE APROVAÇÃO E INSERIDO O RESPETIVO NUMERO SAP

O Responsável por
Catenária e Energia de Tração
Marco Santos

O Responsável por
Estudos e Projetos Ferroviários
Fernando Vendas

Escalas	Tipo	N.º SAP	N.º de Ordem no Projeto	Versão
1:2,5 e 1:30	222 -	10002001570 -	- -	04

O Diretor de Engenharia e Ambiente
José Santinho Faísca
Data
30-12-2019